

| DRAWING INDEX | |
|------------------|--|
| GENERAL DRAWINGS | |
| XC-001 | COVER SHEET AND DRAWING INDEX |
| PLAN DRAWINGS | |
| XC-A101 | EAST BOWL PLAN |
| XC-D101 | 360 PLAN VIEW |
| ELEVATIONS | |
| XC-A201 | EAST BOWL WEST ELEVATION |
| DETAILS | |
| XC-A501 | EAST BOWL - SECTION & DETAILS @ CANOPY ROOF |
| XC-A502 | EAST BOWL - WING WALL PLAN DETAILS |
| XC-A503 | EAST BOWL - WING WALL ZEPP DETAILS |
| XC-A504 | EAST BOWL - TYP ZEPP DETAILS |
| XC-A505 | EAST BOWL - BACK KNIFE EDGE DETAIL |
| XC-A506 | EAST BOWL - ANCHOR DETAILS |
| XC-D501 | 360 - TYPICAL CANOPY CROSS SECTION & DETAILS |
| XC-D502 | 360 - CANOPY CROSS SECTION AT WALKING PATH |


miispel


CITY OF SCOTTSDALE CIVIC CENTER PLAZA

RITOCH-POWELL
RPA & Associates
602-263-1177
WWW.RPAENG.COM

LAKE | FLATO
© 2021 Lake|Flato Architects, Inc.
311 THIRD STREET
SAN ANTONIO, TEXAS 78205
P 210.227.3335 F 210.224.9515
www.lakeflato.com

ZAHNER
ARCHITECTURAL METAL
1400 EAST NINTH STREET
KANSAS CITY, MO 64106
TEL: (816) 474-8882
FAX: (816) 474-7994
WWW.AZAHNER.COM
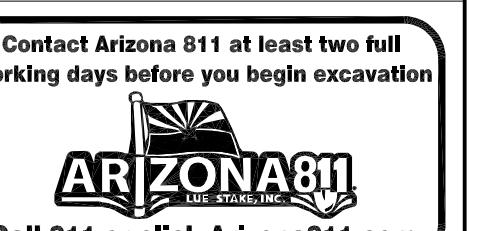
| SET ISSUE DATES | | | | |
|---|-------------|--|-------------------------|--------|
| DATE | ISSUE | | | |
| 01/20/22 100% DRAWINGS | | | | |
| <hr/> <hr/> <hr/> | | | | |
| REVISIONS | | | | |
| NO. | DATE | DESCRIPTION | | |
| <hr/> <hr/> <hr/> | | | | |
| Contact Arizona 811 at least two full working days before you begin excavation | | | | |
|  Call 811 or click Arizona811.com | | | | |
| DATE: 01/20/2022 | | REVISION: | | |
| BY: | | | | |
|  | | PUBLIC WORKS | | |
| | | CAPITAL PROJECT MANAGEMENT | | |
| | | 7447 E. INDIAN SCHOOL RD. SCOTTSDALE, ARIZONA 85251 | | |
| SHEET TITLE | | | | |
| COVER SHEET AND DRAWING INDEX | | | | |
| PROJECT TITLE | | | | |
| CITY OF SCOTTSDALE CIVIC CENTER PLAZA | | | | |
| THIS SHEET SCALED FOR 24X36" BORDER | SCALE | DESIGNED | BID NO. | XC-001 |
| | DRAWN DS | AS-BUILT | COS PROJECT NO. DG04 | |

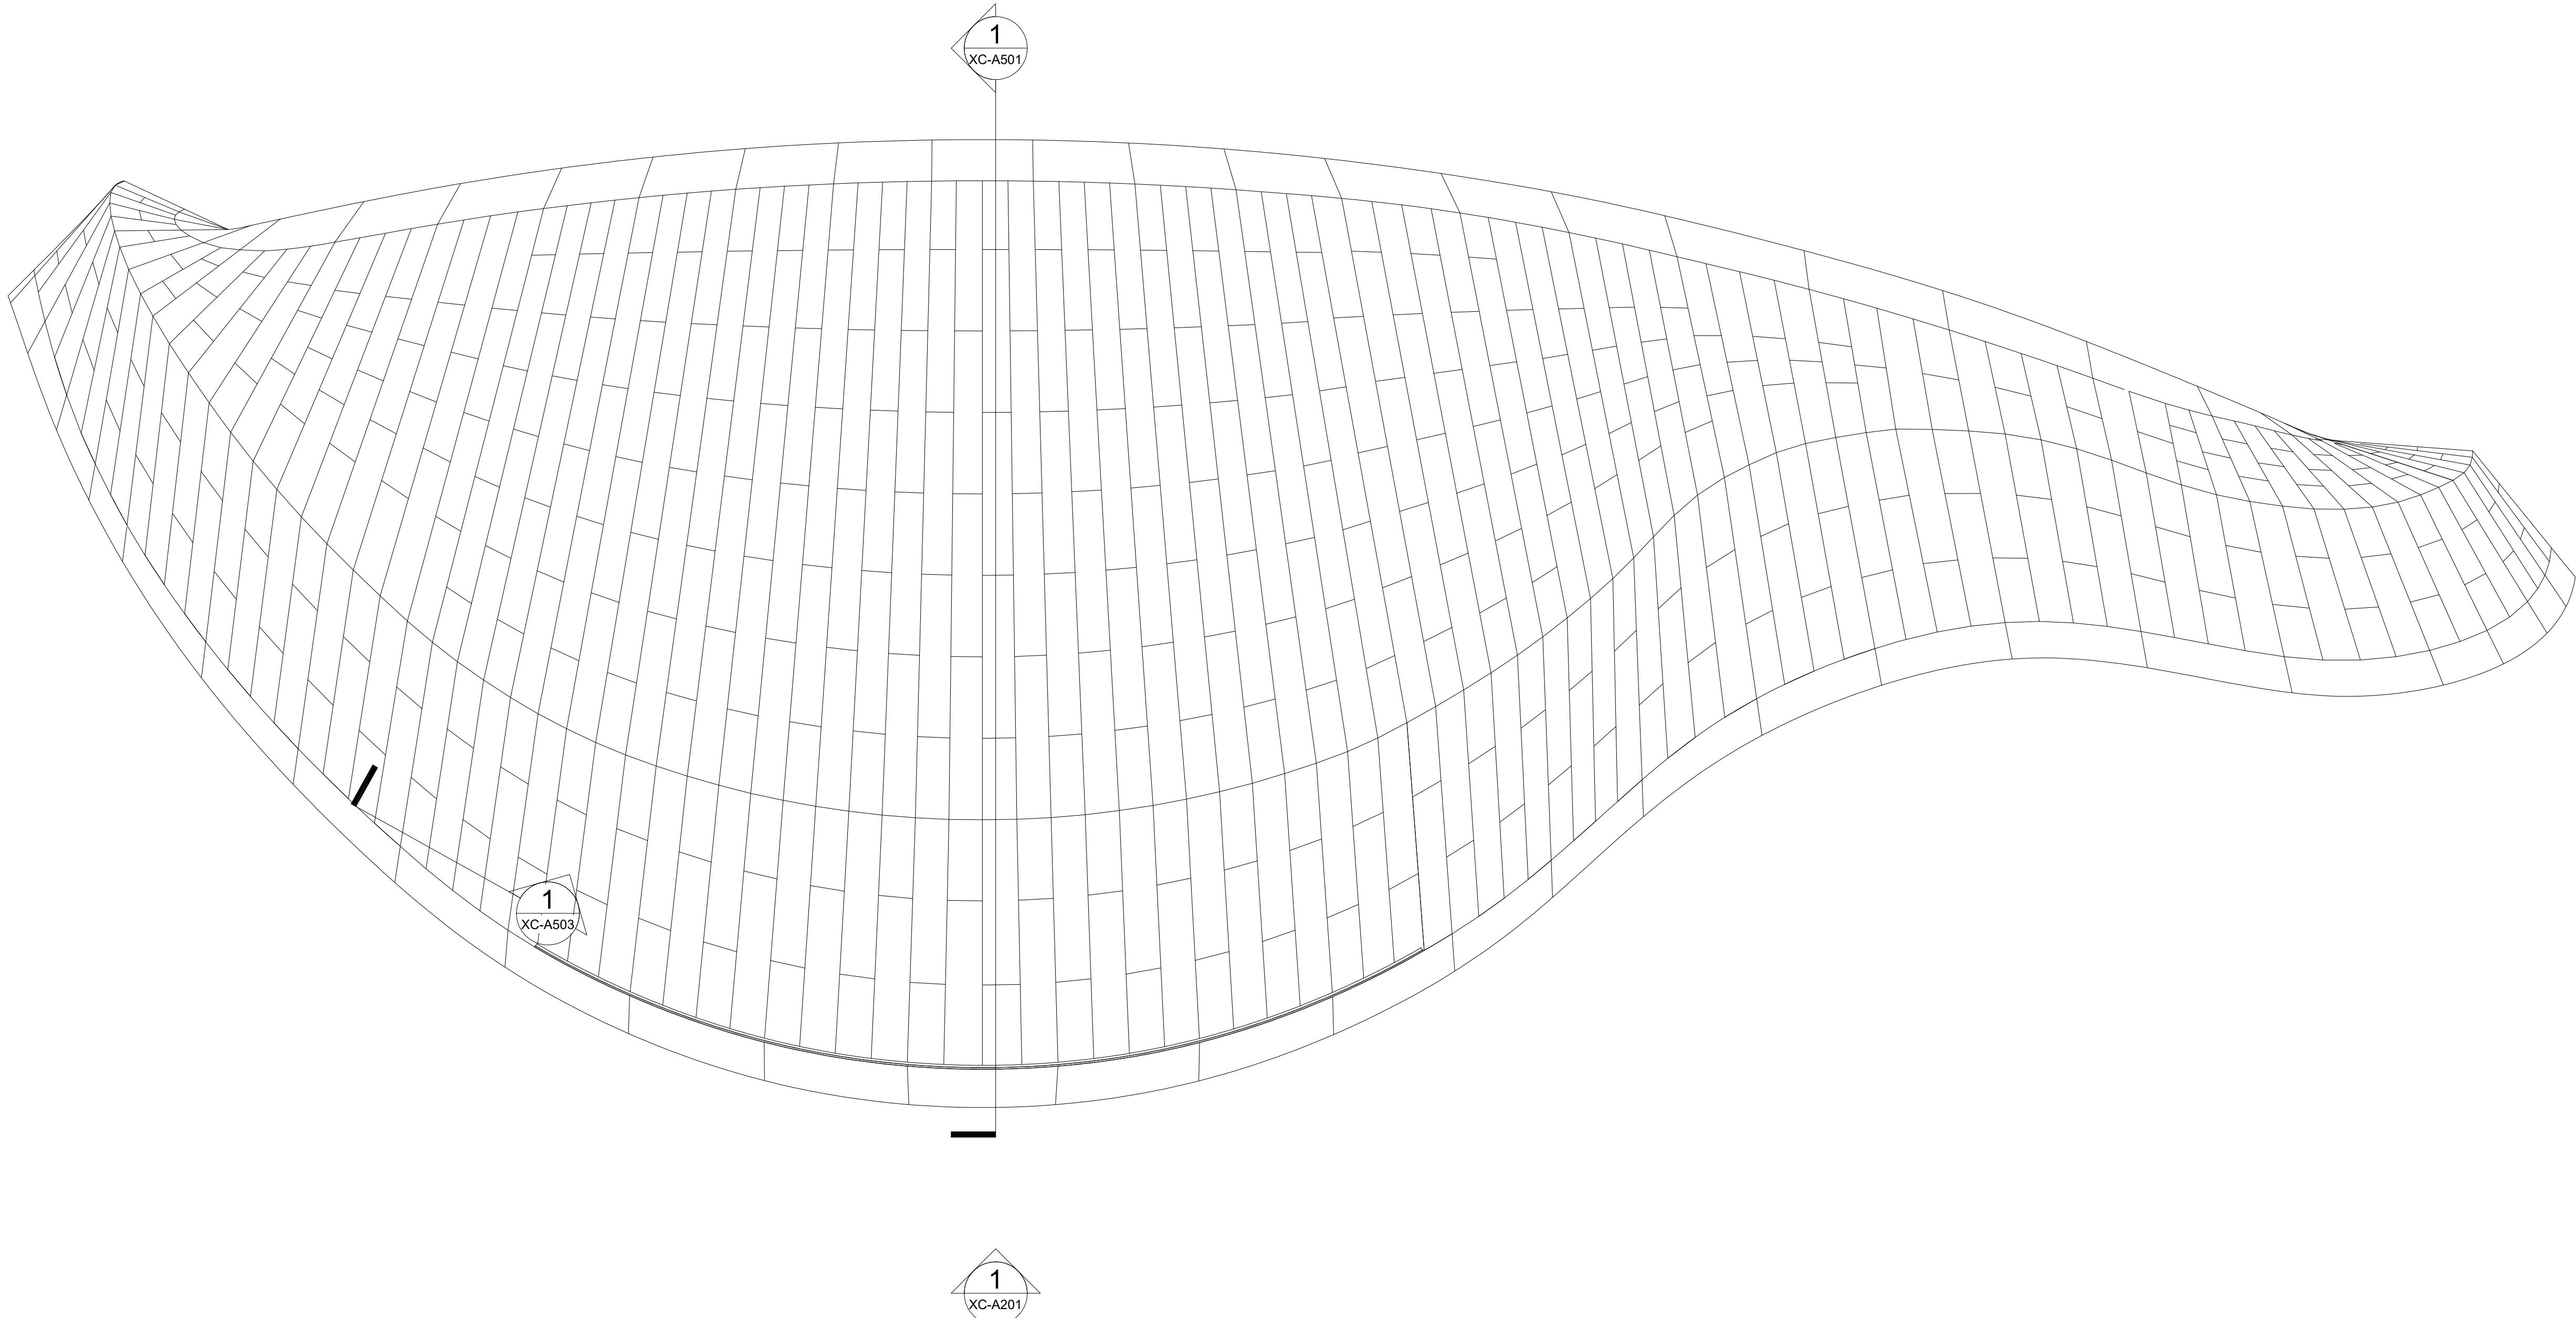


EAST BOWL PLAN VIEW

SCALE: 3/16" = 1'-0"

ZAHNER REF: N/A
ARCH REF: N/A


SET ISSUE DATES
DATE: ISSUE:
01/20/22 100% DRAWINGS

REVISIONS
NO. DATE DESCRIPTION

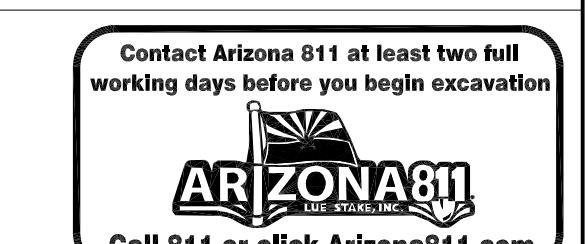

| | | | |
|--|--|---|-----|
| DATE: 01/20/2022 | | REVISION: | BY: |
| ENGINEER | | PUBLIC WORKS | |
| | | CAPITAL PROJECT MANAGEMENT | |
| | | 7447 E. INDIAN SCHOOL RD., SCOTTSDALE, ARIZONA 85251 | |
| SHEET TITLE | | | |
| EAST BOWL PLAN | | | |
| PROJECT TITLE | | | |
| CITY OF SCOTTSDALE CIVIC CENTER PLAZA | | | |

| THIS SHEET SCALED FOR 24X36" BORDER | SCALE | DESIGNED | BID NO. | XC-A101 |
|--|-------------|----------|-------------------------|---------|
| | DRAWN DS | AS-BUILT | COS PROJECT NO. DG04 | |

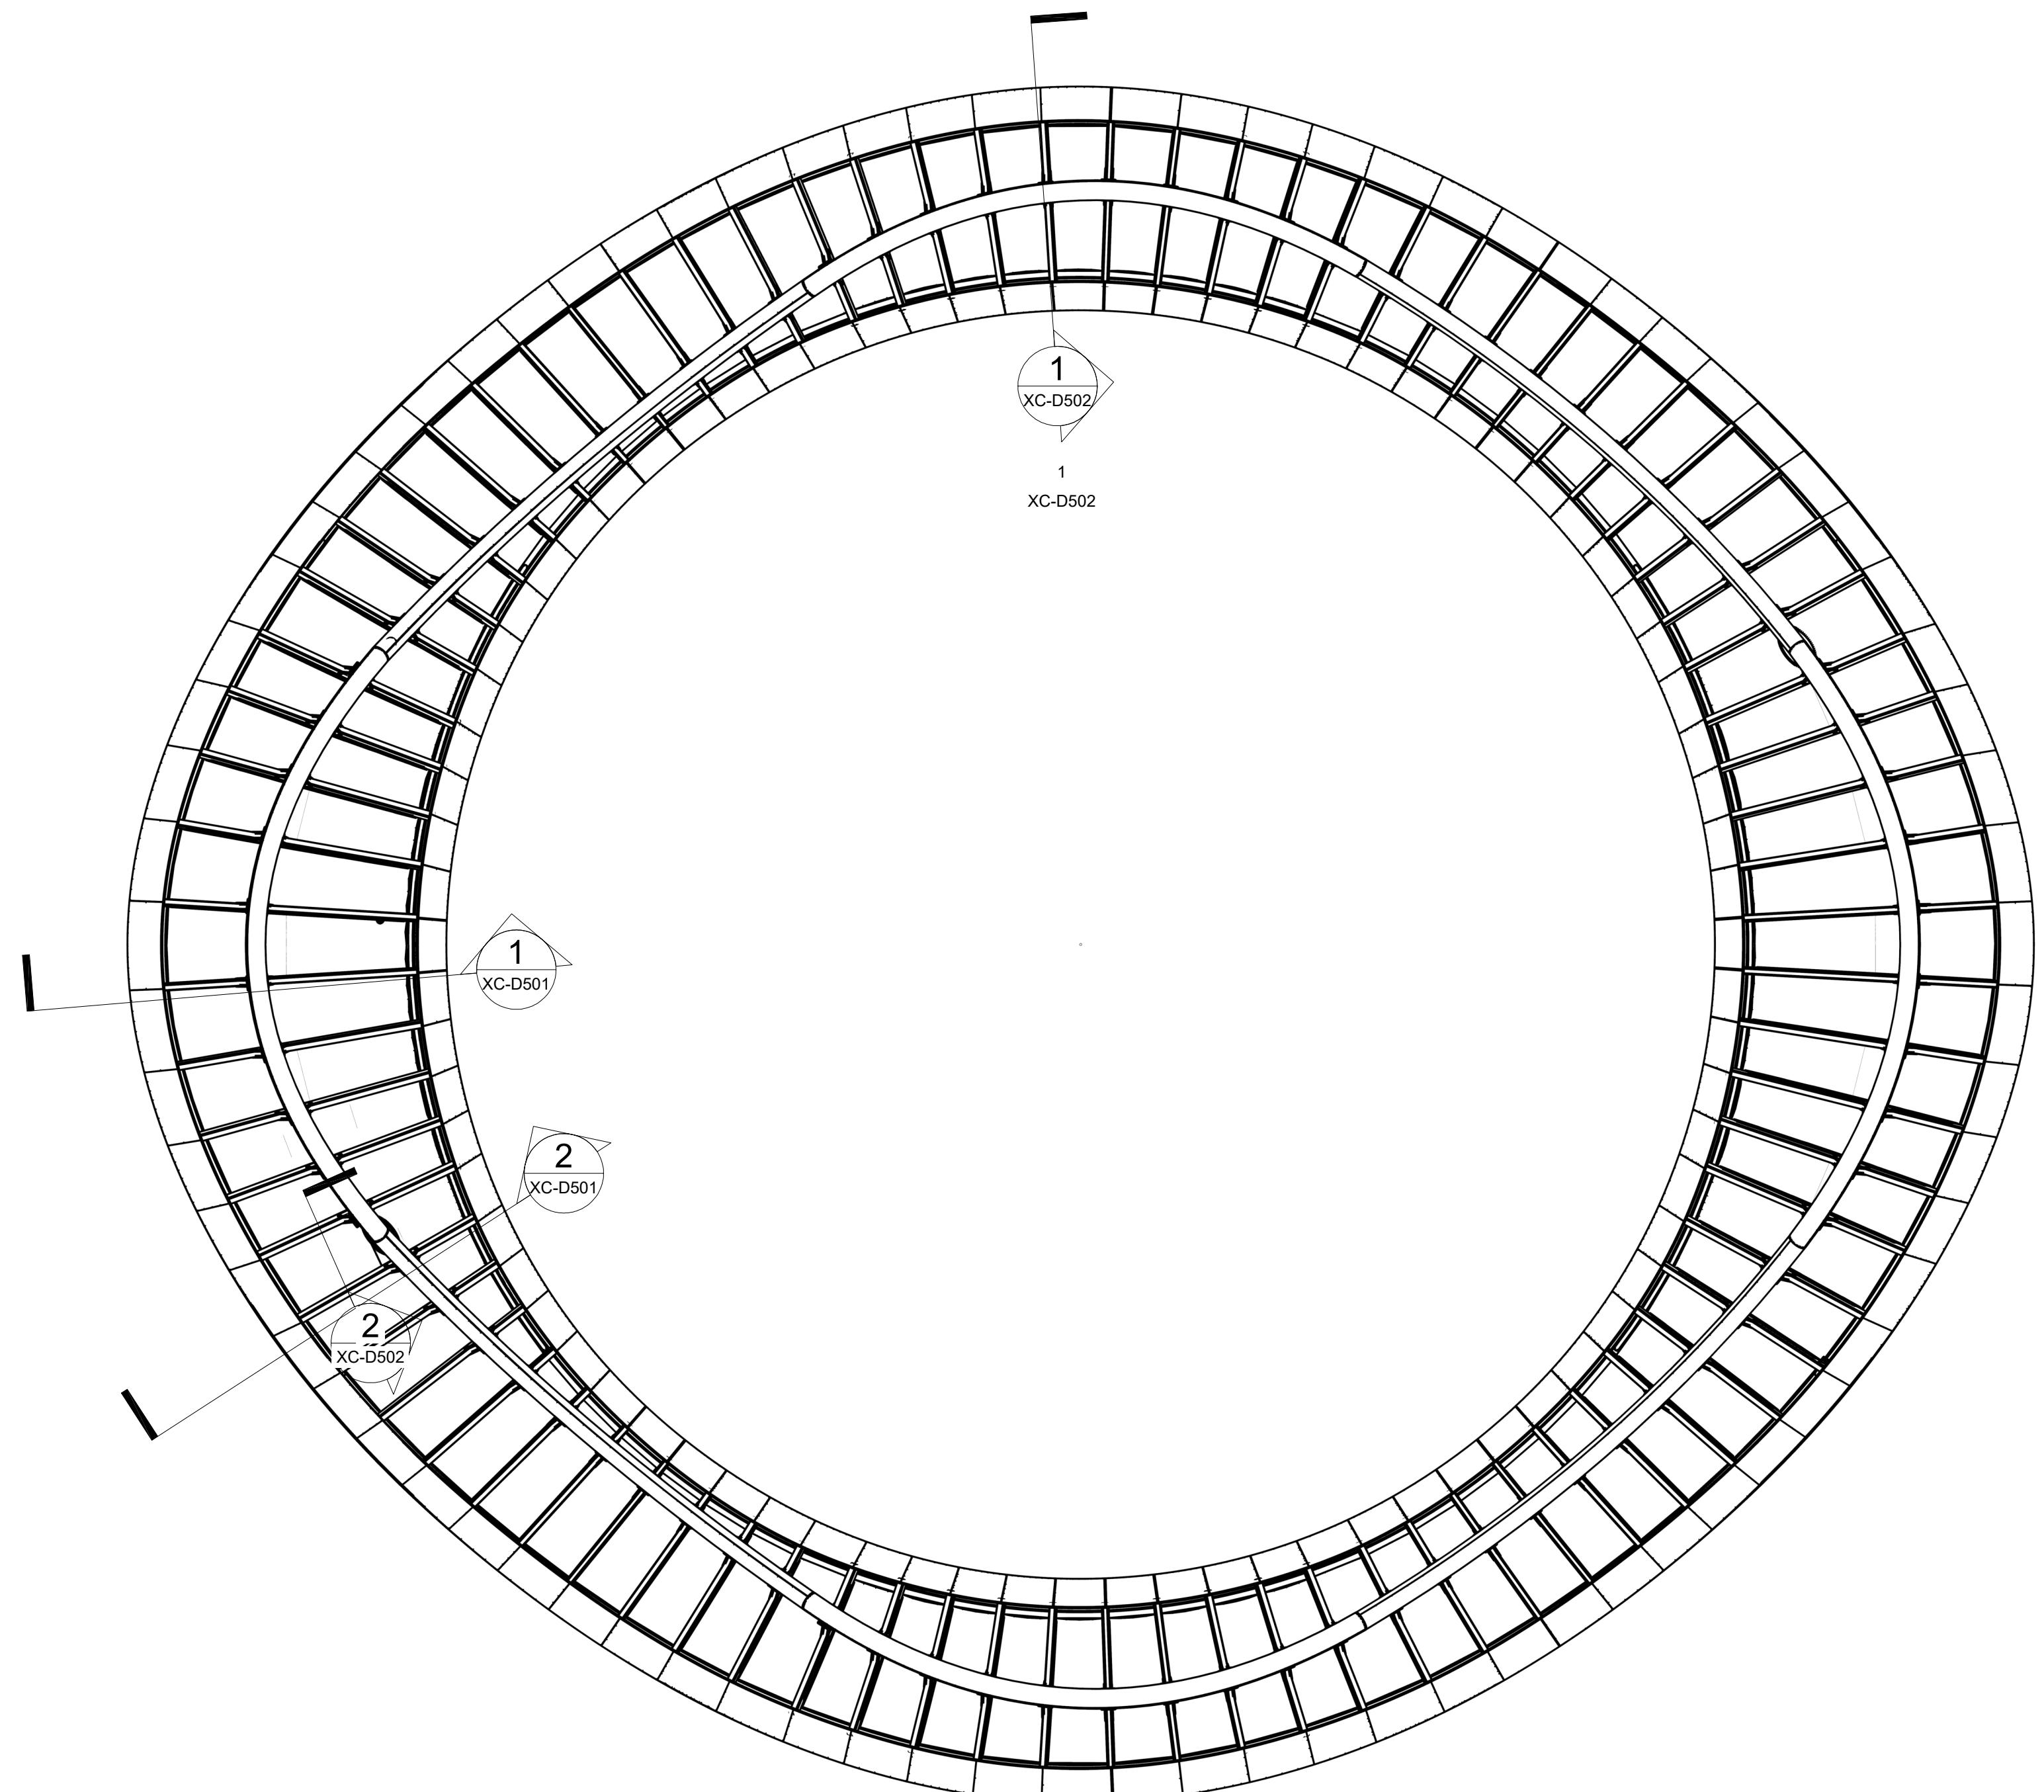

1 360 CANOPY - PLAN VIEW

SCALE: 1/8" = 1'-0"


ZAHNER REF: XX
ARCH REF: XX

360 CANOPY PLAN


PROJECT TITLE CITY OF SCOTTSDALE
CIVIC CENTER PLAZA


| THIS SHEET SCALED FOR 24X36" BORDER | SCALE | DESIGNED | BID NO. | XC-D101 |
|--|-------|-------------|----------|-------------------------|
| | | DRAWN DS | AS-BUILT | COS PROJECT NO. DG04 |

| | | |
|------------------------|-------|-------------|
| SET ISSUE DATES | | |
| DATE | ISSUE | |
| 01/20/22 100% DRAWINGS | | |
| <hr/> <hr/> <hr/> | | |
| REVISIONS | | |
| NO. | DATE | DESCRIPTION |
| <hr/> <hr/> <hr/> | | |

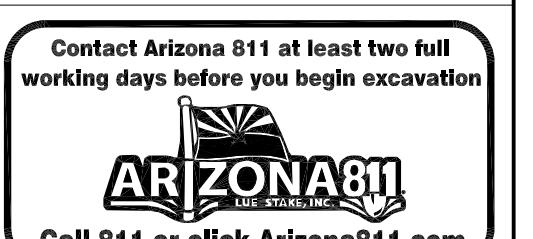


| | | |
|------------------|-----------|--|
| DATE: 01/20/2022 | REVISION: | BY: |
| ENGINEER | | PUBLIC WORKS |
| | | CAPITAL PROJECT MANAGEMENT |
| | | 7447 E. INDIAN SCHOOL RD. SCOTTSDALE, ARIZONA 85251 |
| SHEET TITLE | | |

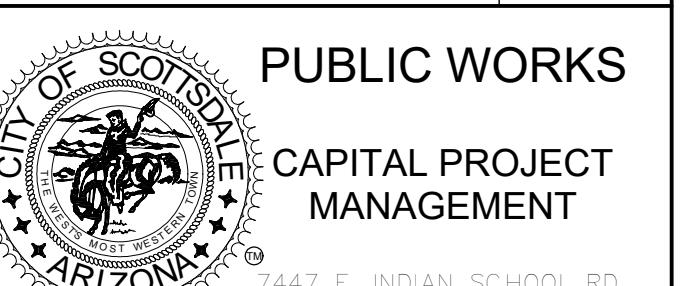

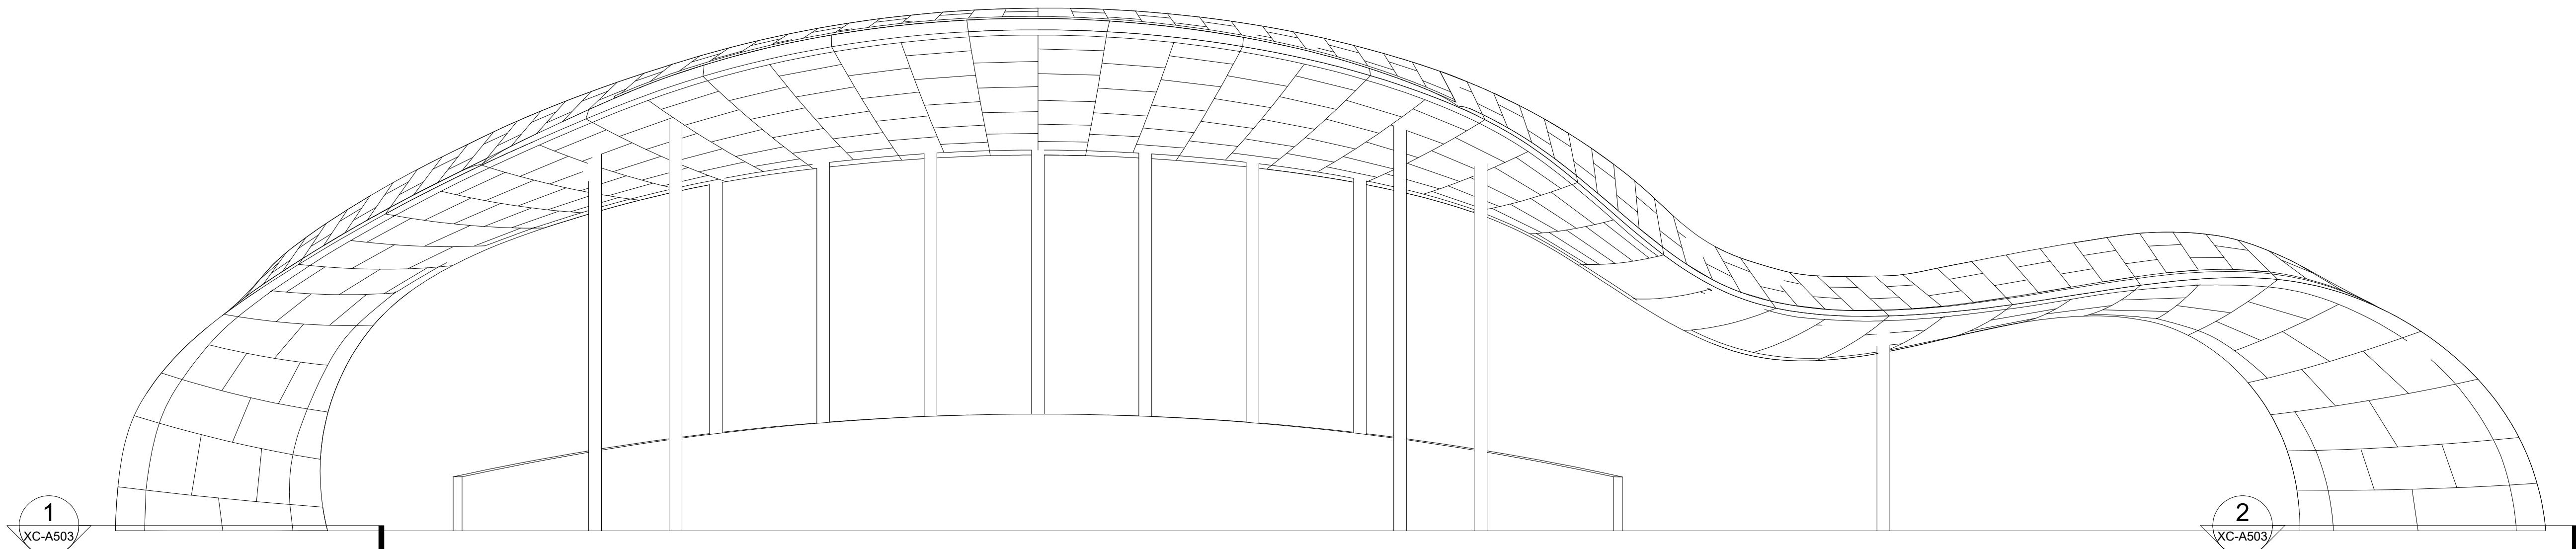


① EAST BOWL WEST ELEVATION
SCALE: 3/16" = 1'-0"
ZAHNER REF: N/A
ARCH REF: N/A

| | | |
|------------------------|-------|-------------|
| SET ISSUE DATES | | |
| DATE | ISSUE | BY: |
| 01/20/22 100% DRAWINGS | | |
| REVISIONS | | |
| NO. | DATE | DESCRIPTION |
| | | |
| | | |
| | | |
| | | |

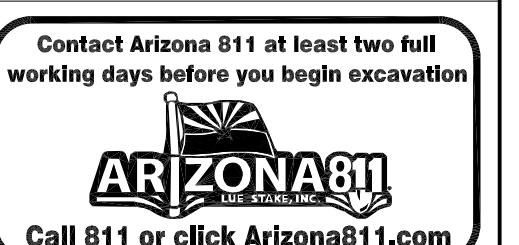


| | | |
|---------------------------------------|-----------|----------------------------|
| DATE: 01/20/2022 | REVISION: | BY: |
| ENGINEER | | PUBLIC WORKS |
| | | CAPITAL PROJECT MANAGEMENT |
| SHEET TITLE | | |
| EAST BOWL WEST ELEVATION | | |
| PROJECT TITLE | | |
| CITY OF SCOTTSDALE CIVIC CENTER PLAZA | | |

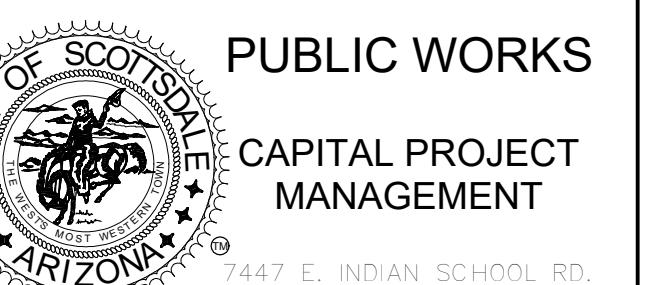

7447 E. INDIAN SCHOOL RD.
SCOTTSDALE, ARIZONA 85251

| THIS SHEET SCALED FOR 24X36" BORDER | SCALE | DESIGNED | BID NO. | XC-A201 |
|--|-------------|----------|-------------------------|---------|
| | DRAWN DS | AS-BUILT | COS PROJECT NO. DG04 | |

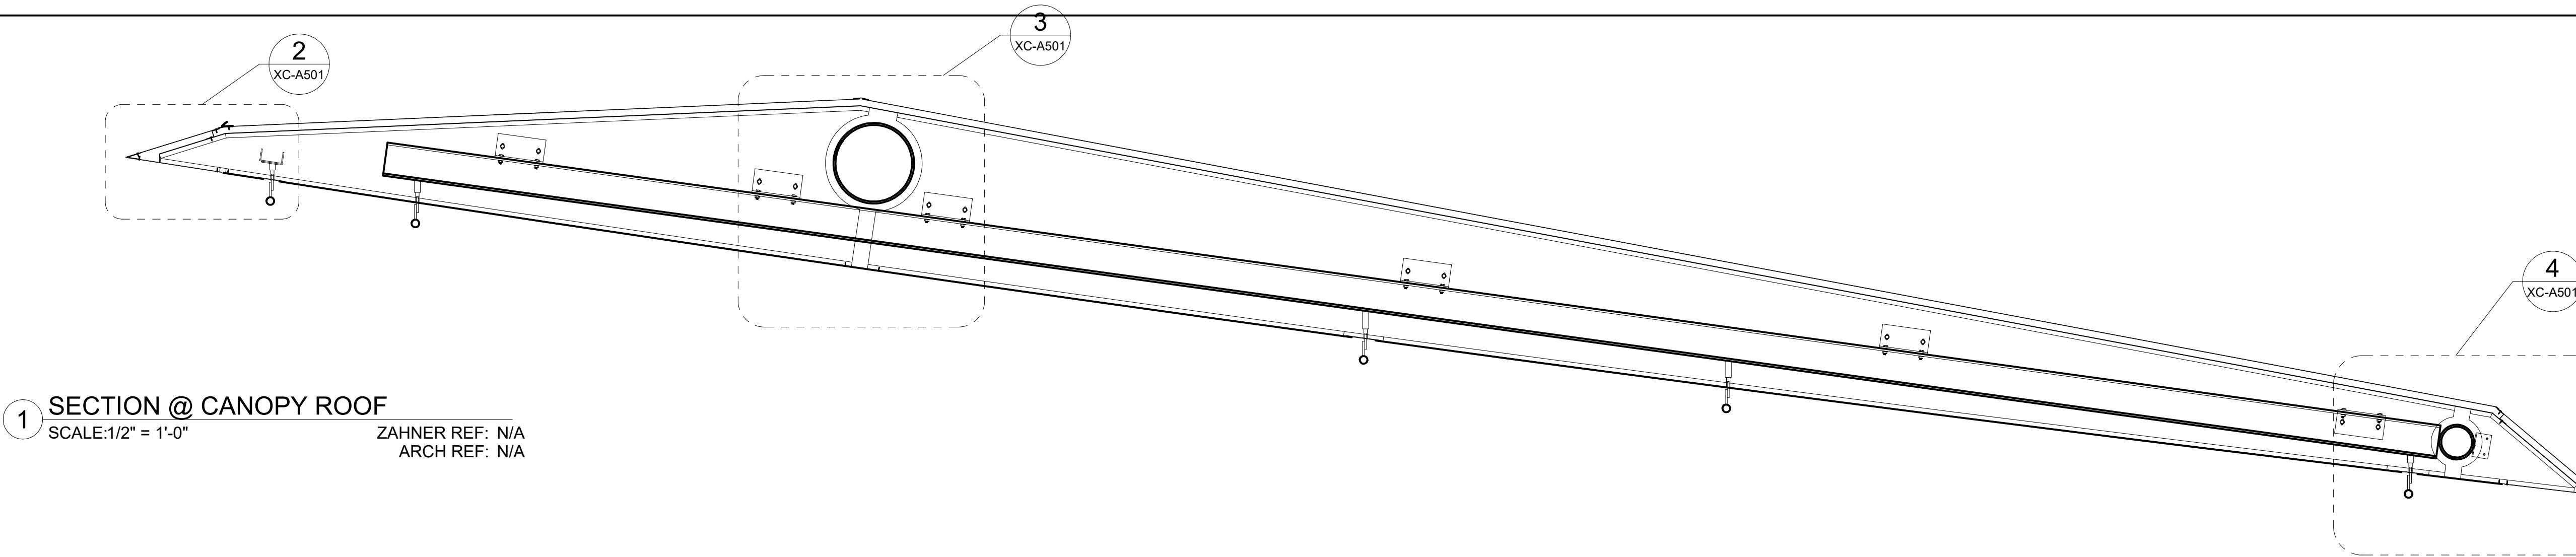


1 SECTION @ CANOPY ROOF

SCALE: 1/2" = 1'-0"
 ZAHNER REF: N/A
 ARCH REF: N/A


2 SECTION DETAIL @ DOWNSTAGE CANOPY

SCALE: 1 1/2" = 1'-0"
 ZAHNER REF: N/A
 ARCH REF: N/A

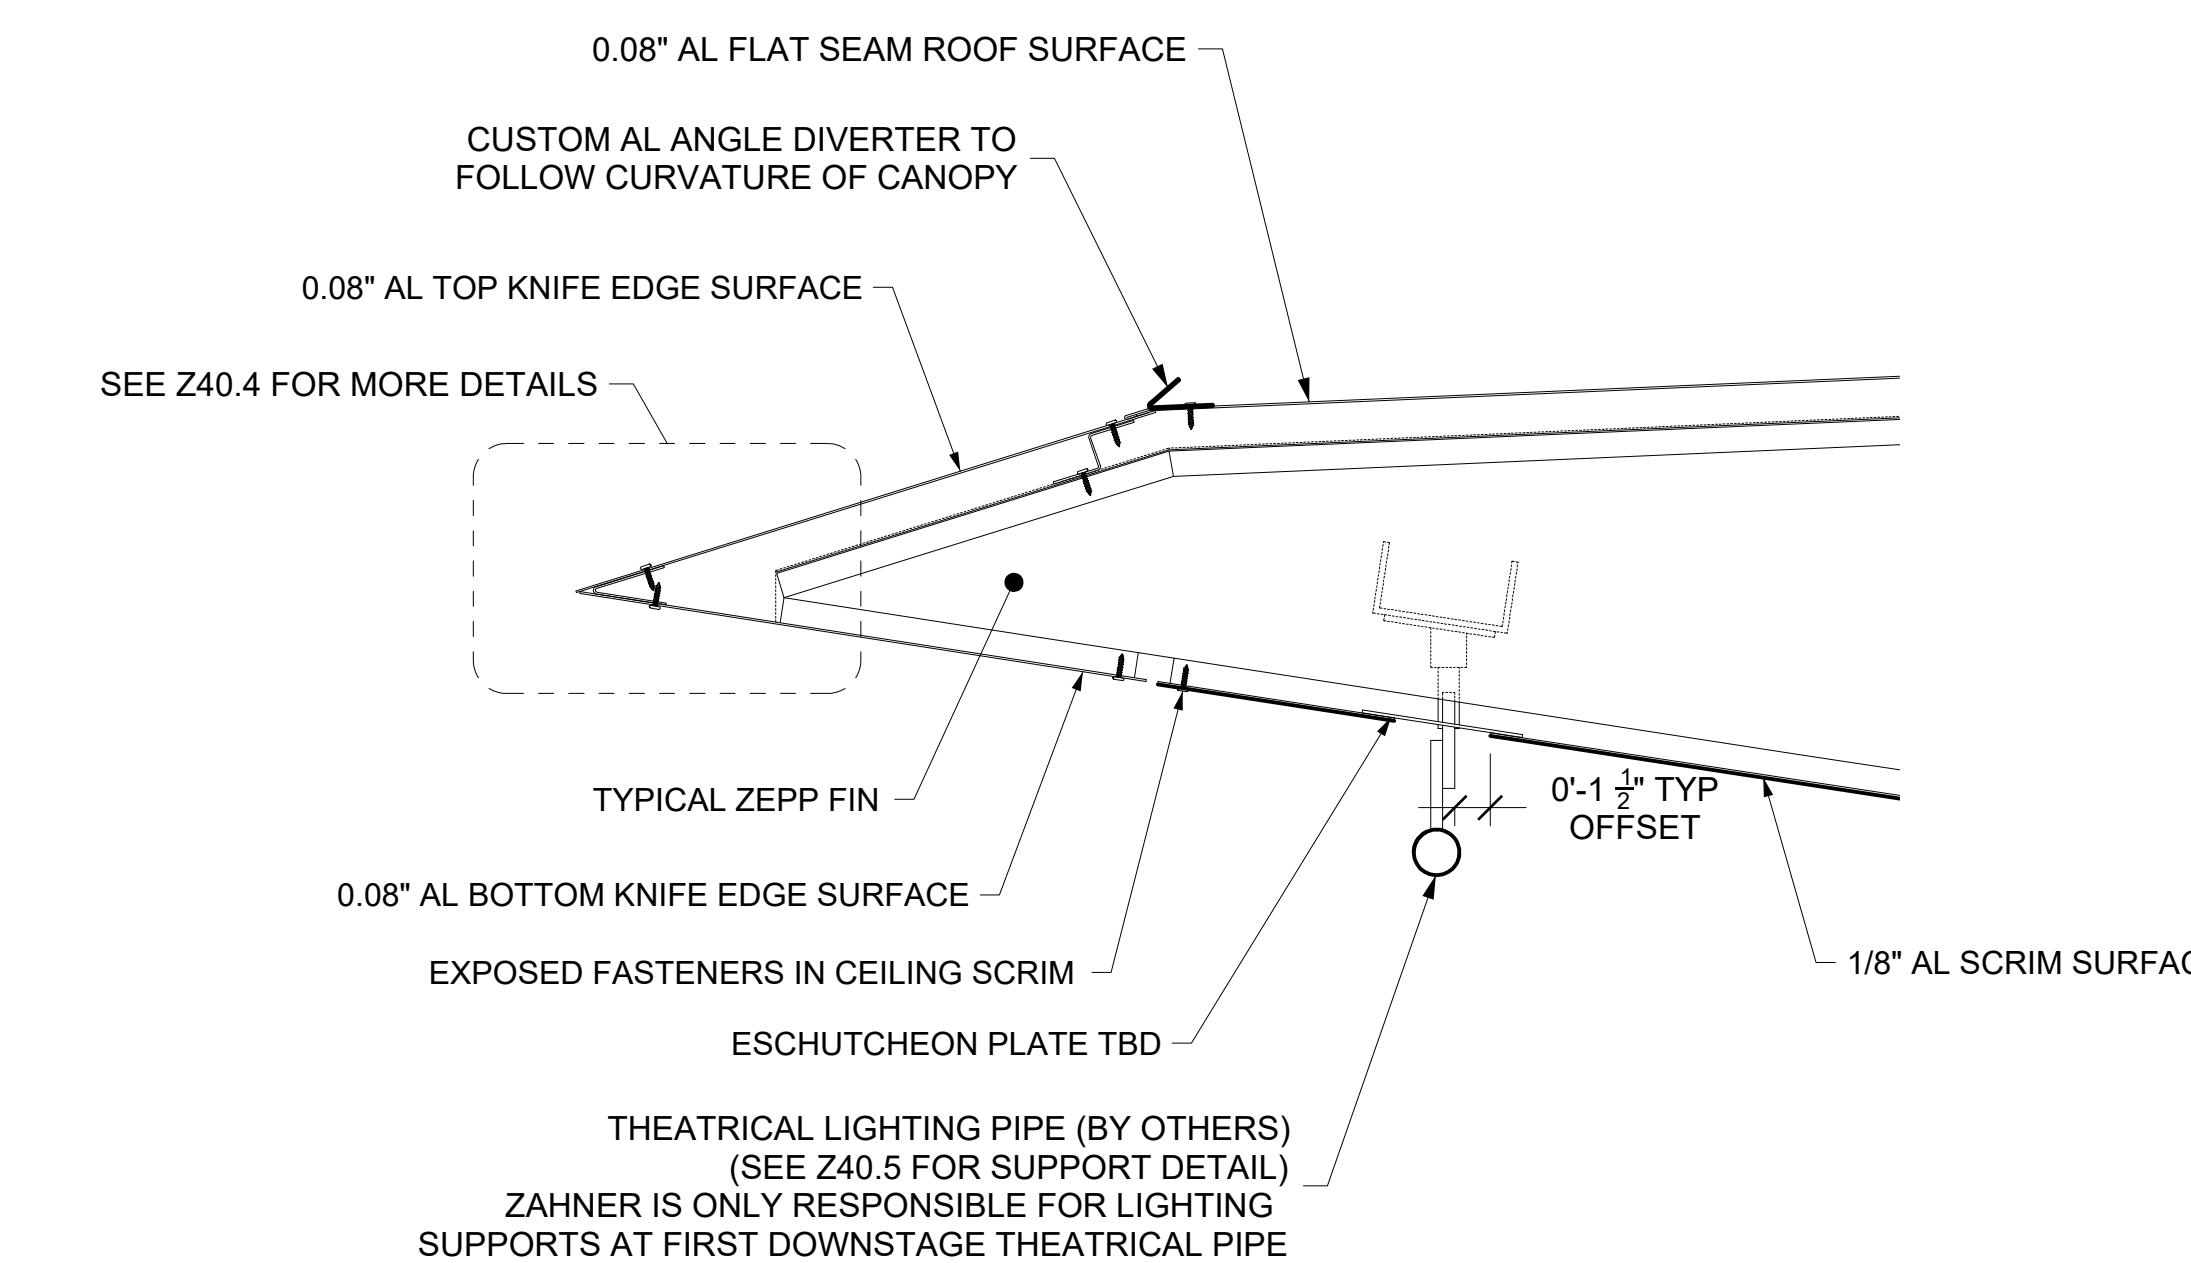


3 SECTION DETAIL @ DOWNSTAGE CANOPY

SCALE: 1 1/2" = 1'-0"
 ZAHNER REF: N/A
 ARCH REF: N/A

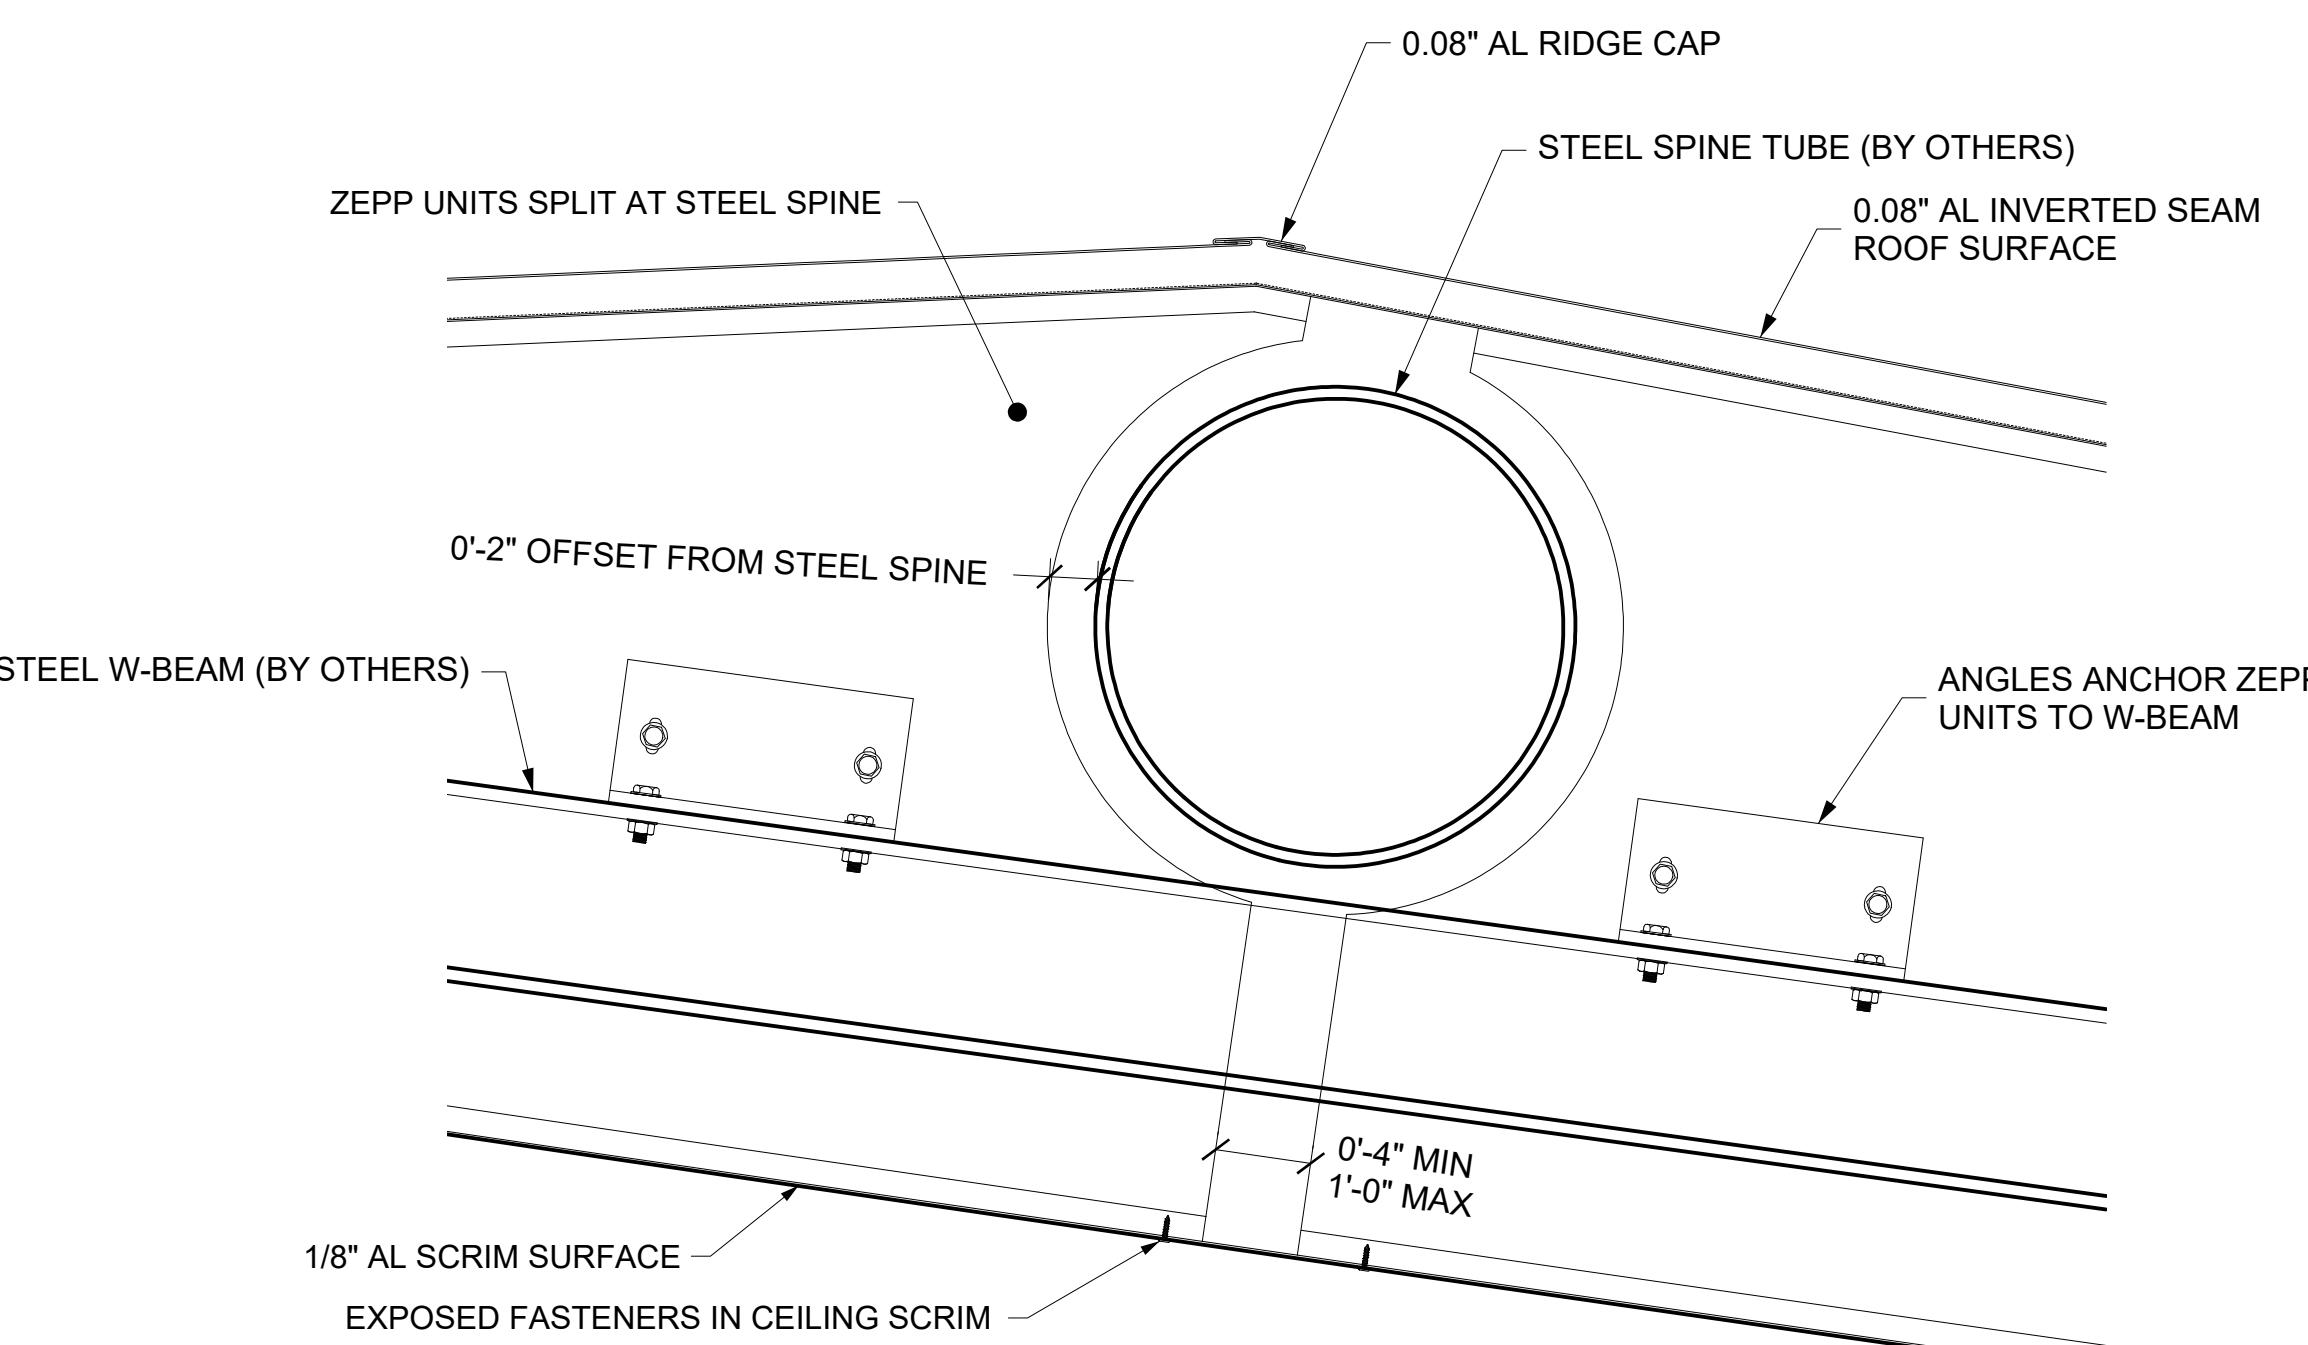

3 SECTION DETAIL @ DOWNSTAGE CANOPY

SCALE: 1 1/2" = 1'-0"
 ZAHNER REF: N/A
 ARCH REF: N/A

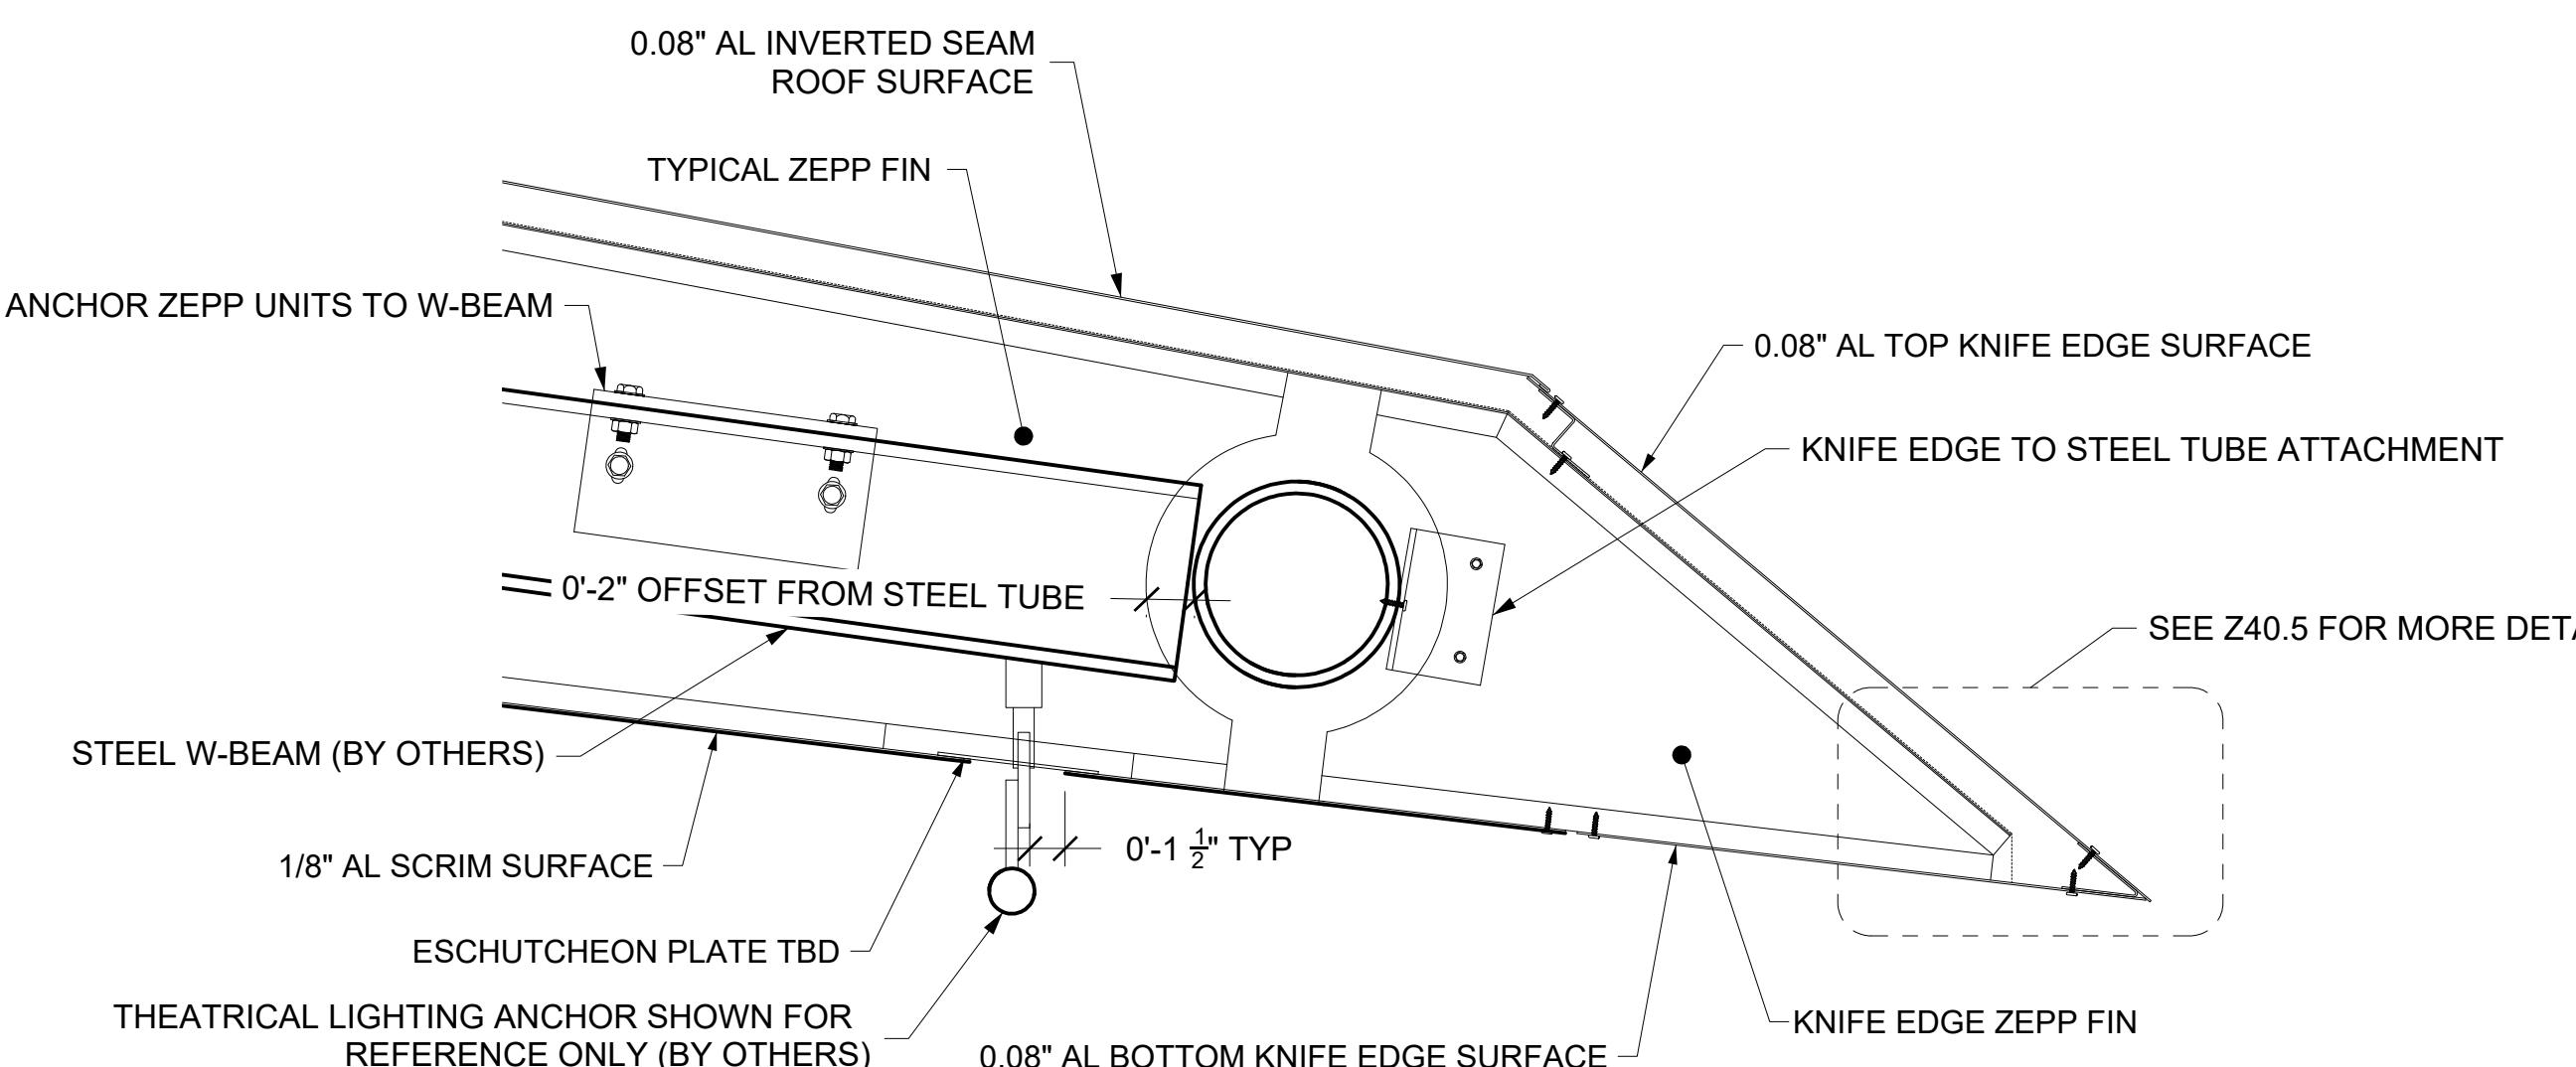

4 SECTION DETAIL @ UPSTAGE CANOPY

SCALE: 1 1/2" = 1'-0"
 ZAHNER REF: N/A
 ARCH REF: N/A

SET ISSUE DATES
 DATE: ISSUE:
 01/20/22 100% DRAWINGS

REVISIONS

| NO. | DATE | DESCRIPTION |
|-----|------|-------------|
| | | |
| | | |
| | | |
| | | |




| | | |
|---|-----------|----------------------------|
| DATE: 01/20/2022 | REVISION: | BY: |
| ENGINEER | | PUBLIC WORKS |
| | | CAPITAL PROJECT MANAGEMENT |
| 7447 E. INDIAN SCHOOL RD., SCOTTSDALE, ARIZONA 85251 | | |


EAST BOWL - SECTION & DETAILS

PROJECT TITLE: CITY OF SCOTTSDALE CIVIC CENTER PLAZA


| THIS SHEET SCALED FOR 24X36" BORDER | SCALE | DESIGNED | BID NO. | XC-A501 |
|-------------------------------------|----------|----------|----------------------|---------|
| | DRAWN DS | AS-BUILT | COS PROJECT NO. DG04 | |

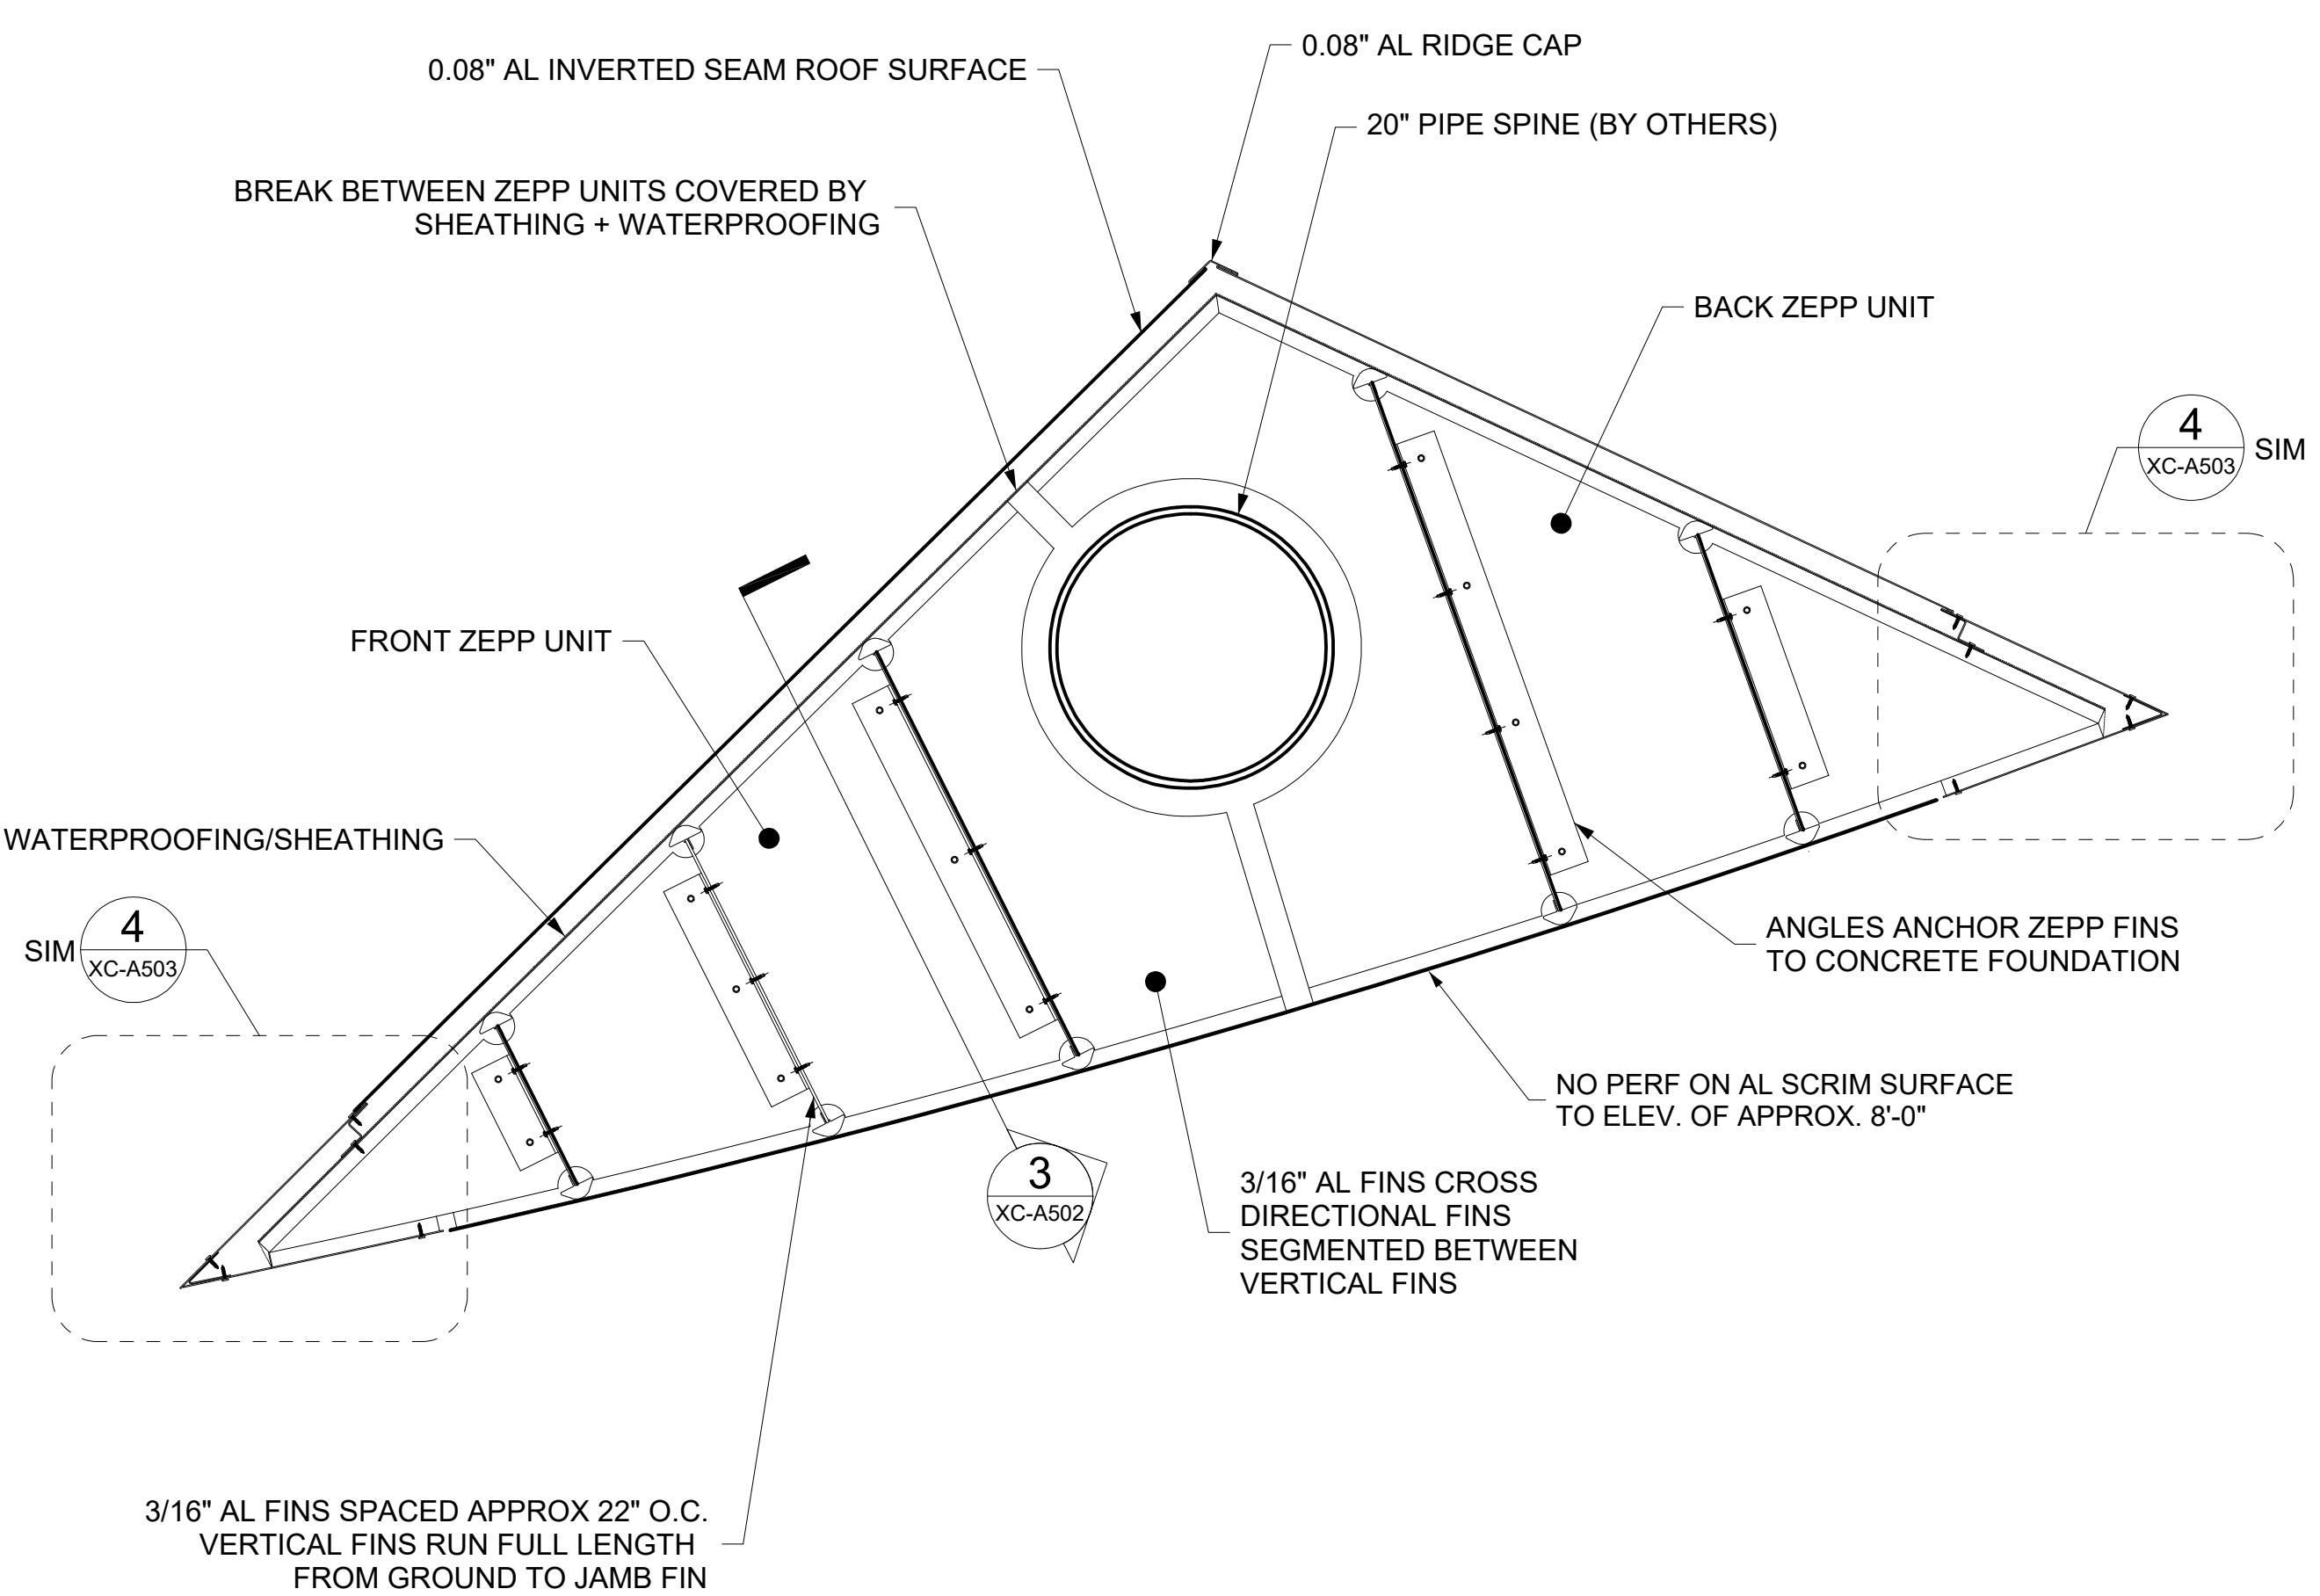

1 PLAN DETAIL @ NORTH WING WALL
SCALE: 1" = 1'-0"
ZAHNER REF: N/A
ARCH REF: N/A

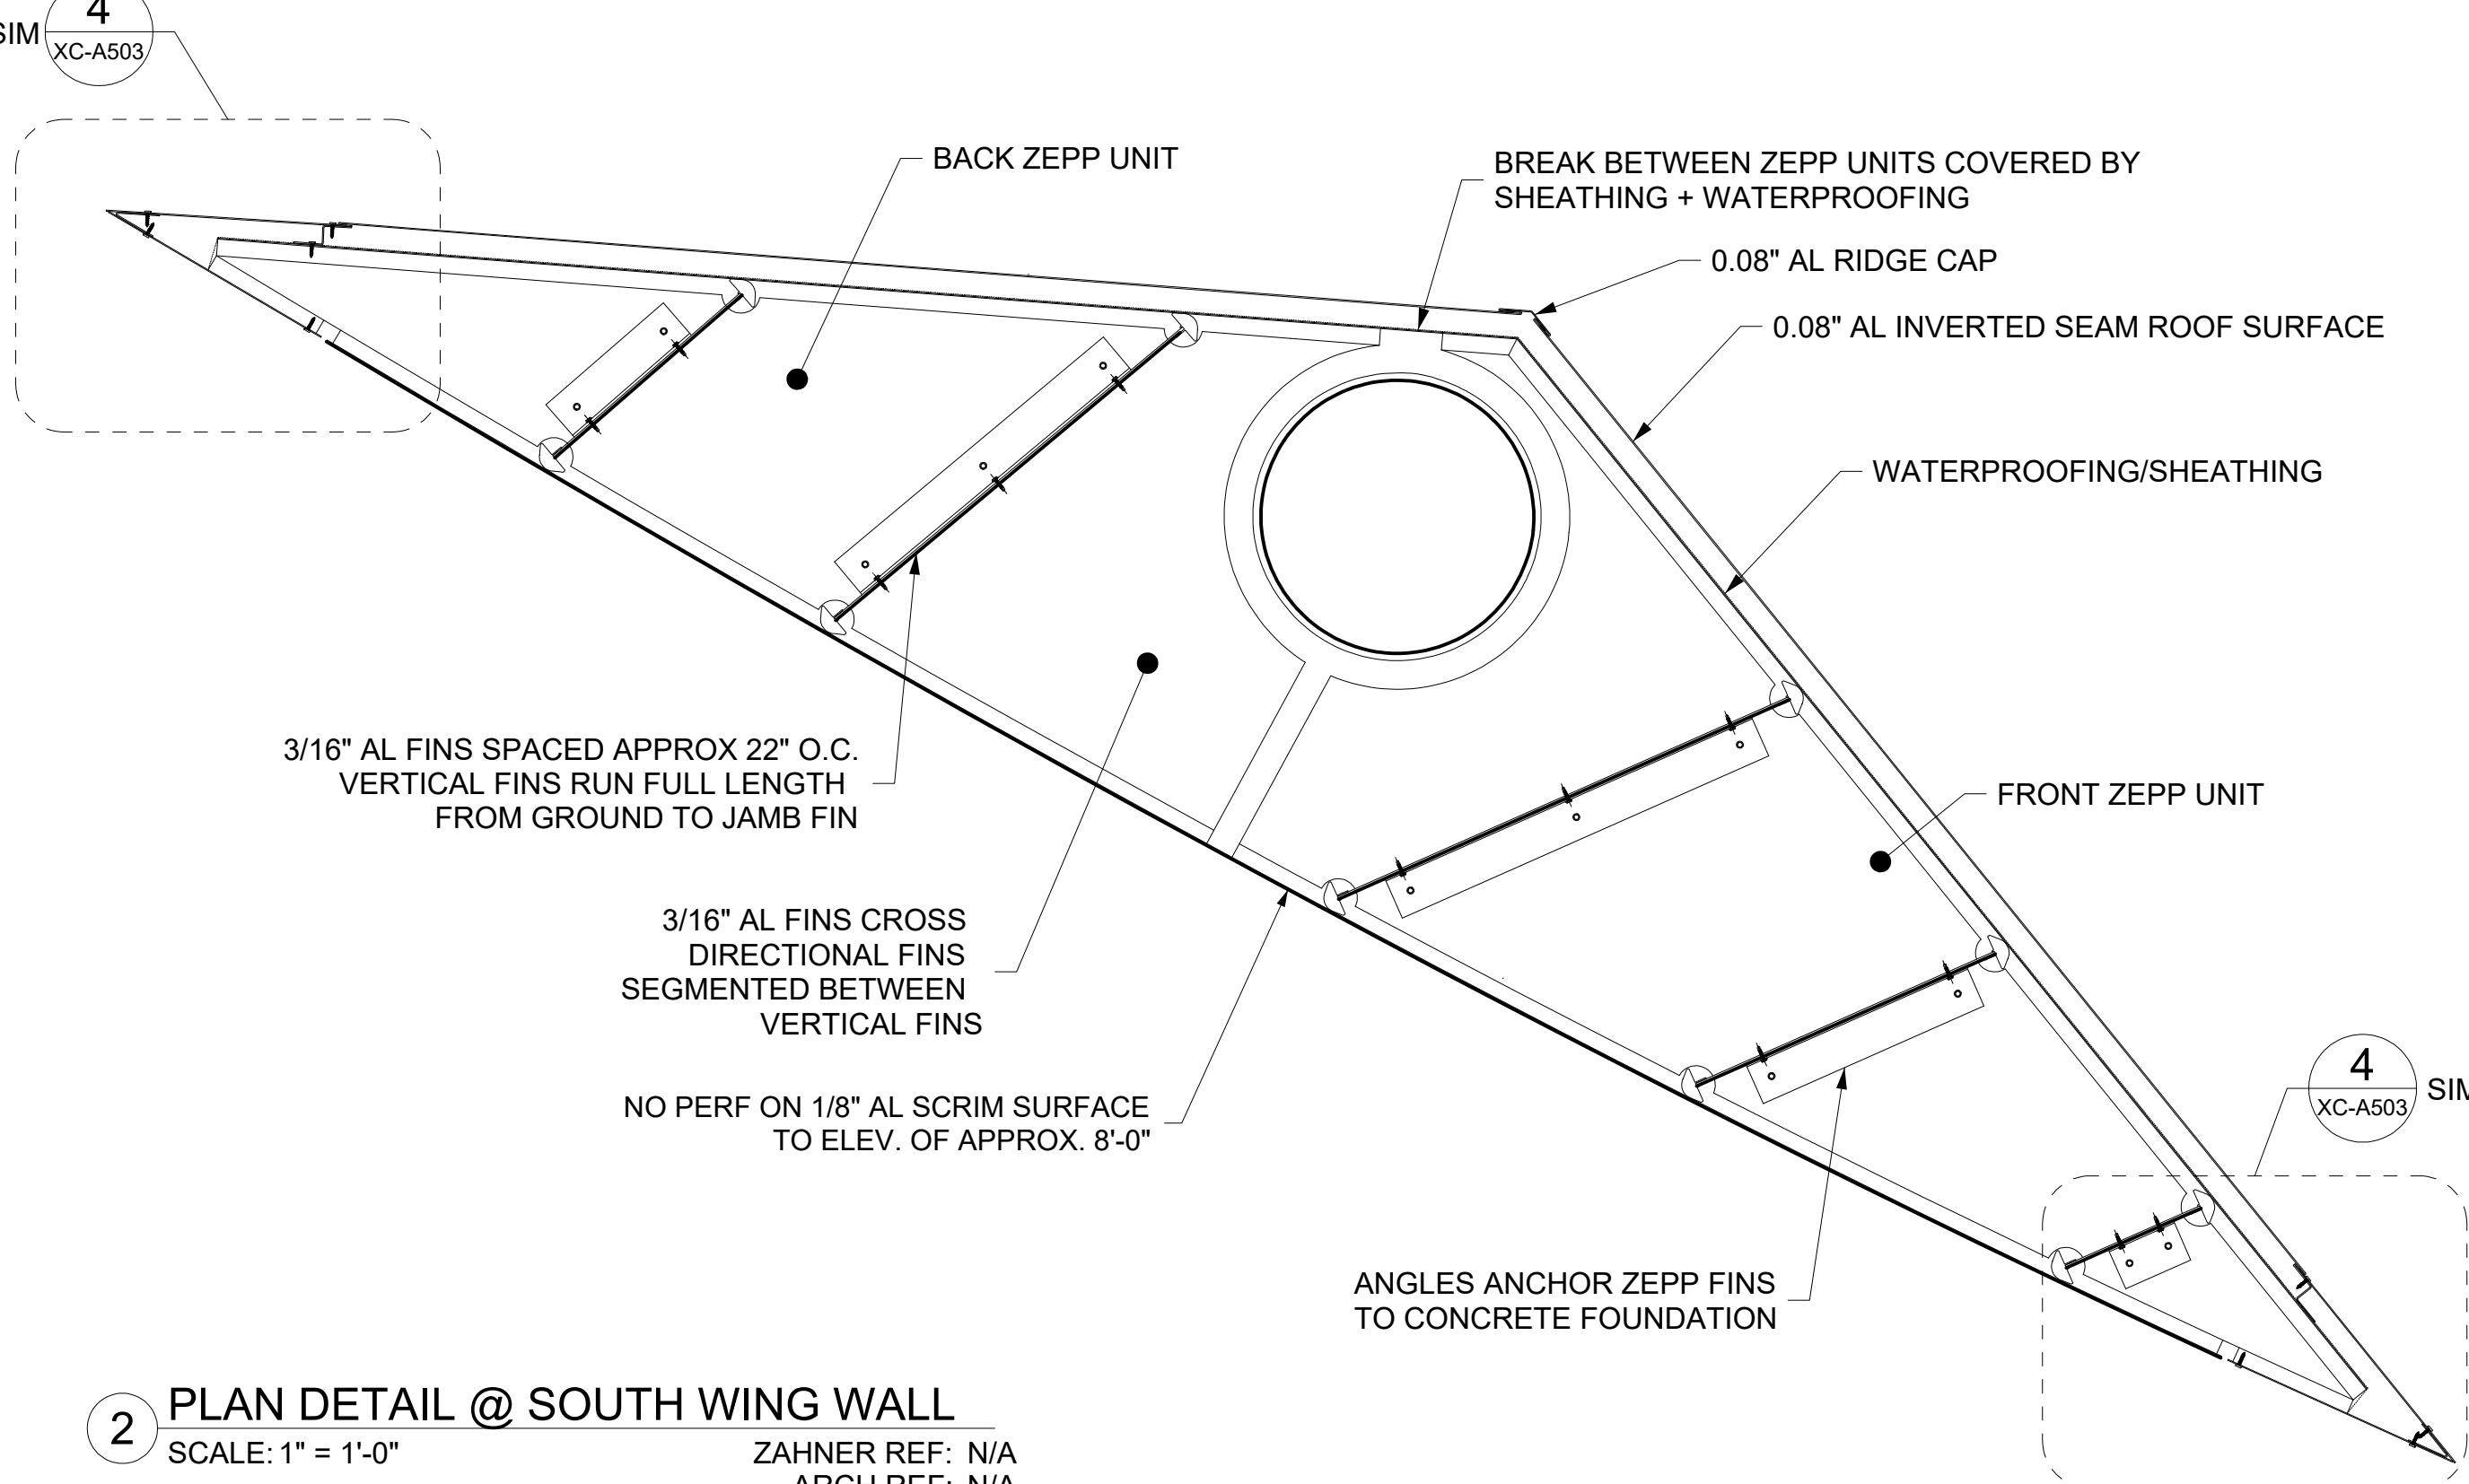


2 PLAN DETAIL @ SOUTH WING WALL
SCALE: 1" = 1'-0"
ZAHNER REF: N/A
ARCH REF: N/A

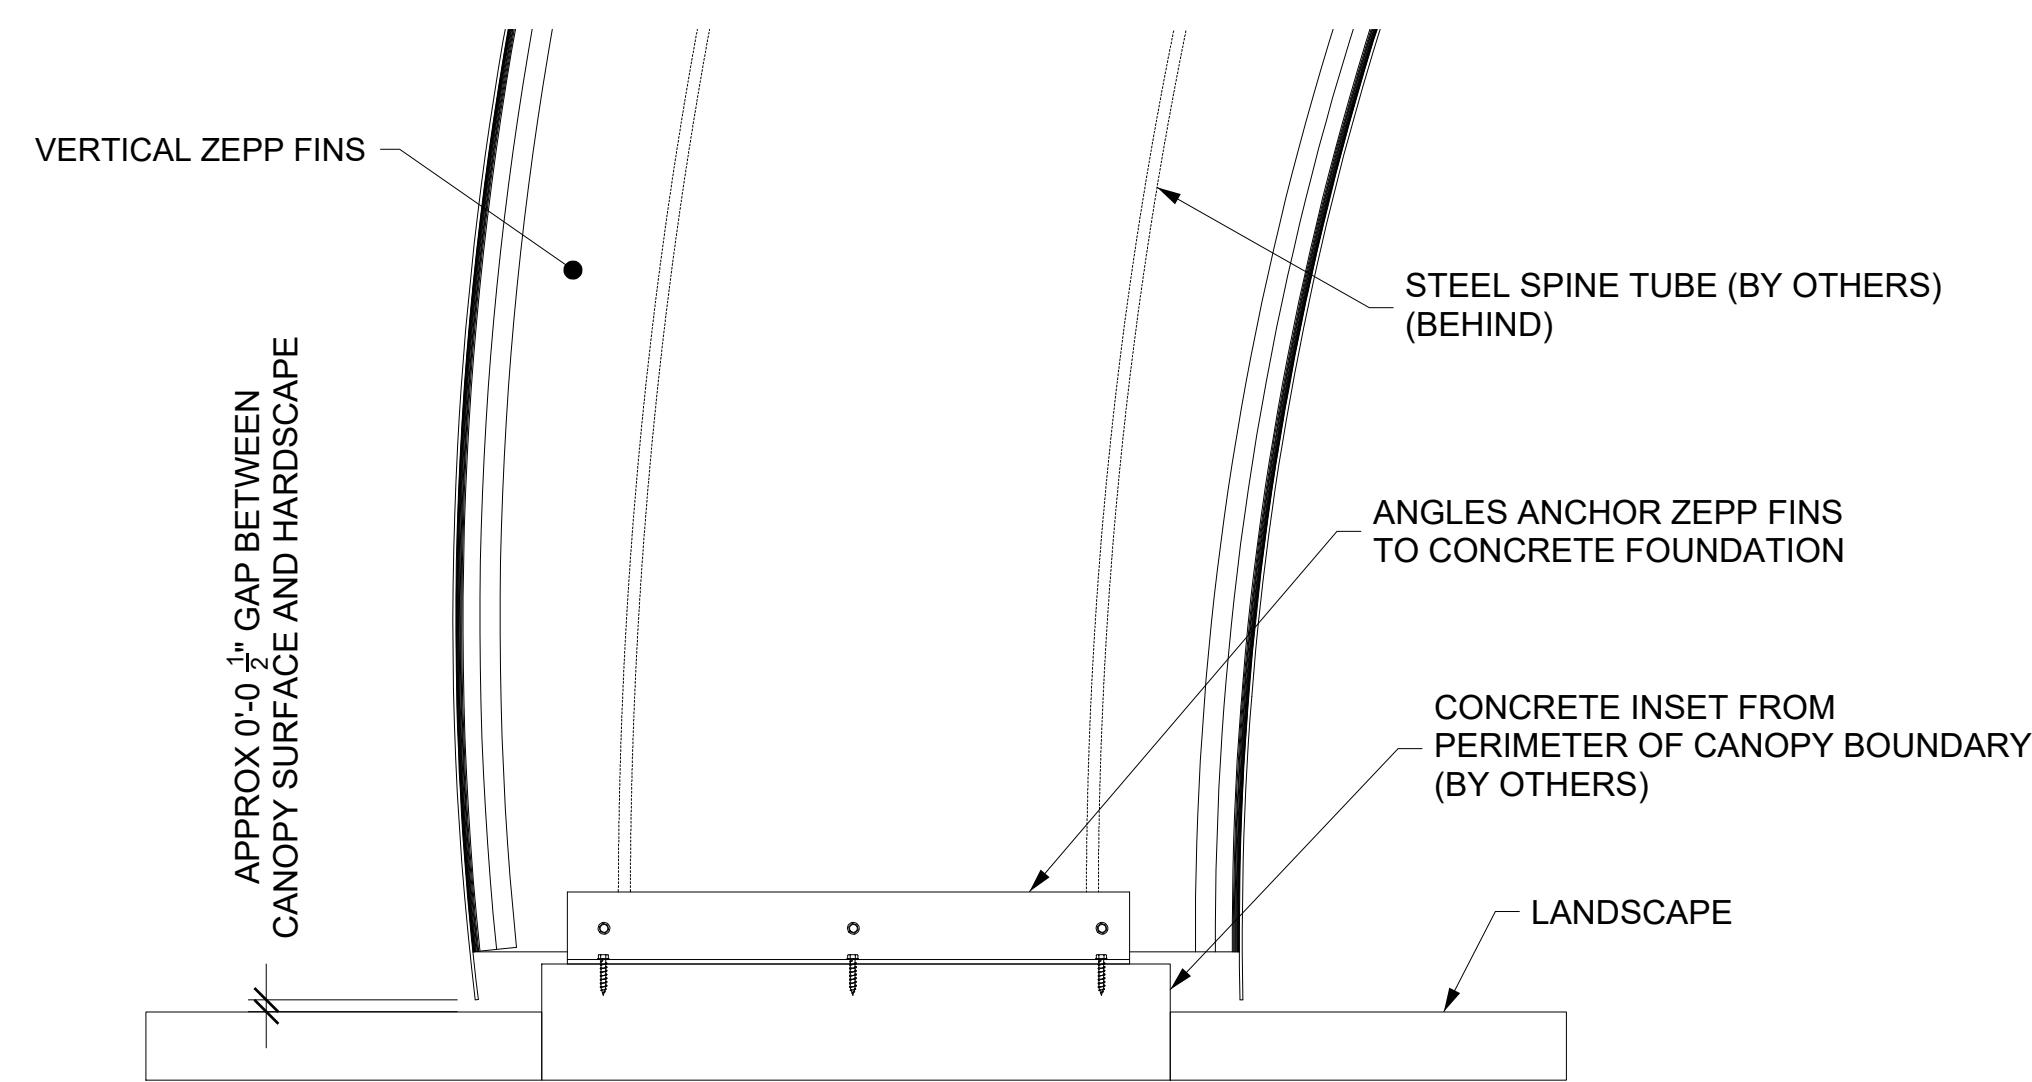

3 SECTION DETAIL @ NORTH WING WALL
SCALE: 1 1/2" = 1'-0"
ZAHNER REF: N/A
ARCH REF: N/A

| | | |
|------------------------|-------|-------------|
| SET ISSUE DATES | | |
| DATE | ISSUE | |
| 01/20/22 100% DRAWINGS | | |
| | | |
| REVISIONS | | |
| NO. | DATE | DESCRIPTION |
| | | |
| | | |

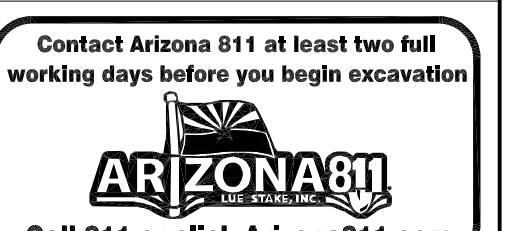


| | | |
|---|-----------|----------------------------|
| DATE: 01/20/2022 | REVISION: | BY: |
| ENGINEER | | PUBLIC WORKS |
| | | CAPITAL PROJECT MANAGEMENT |
| 7447 E. INDIAN SCHOOL RD., SCOTTSDALE, ARIZONA 85251 | | |


EAST BOWL - WING WALL PLAN DETAILS

PROJECT TITLE: CITY OF SCOTTSDALE CIVIC CENTER PLAZA


| THIS SHEET SCALED FOR 24X36" BORDER | SCALE | DESIGNED | BID NO. | XC-A502 |
|-------------------------------------|----------|----------|----------------------|---------|
| | DRAWN DS | AS-BUILT | COS PROJECT NO. DG04 | |

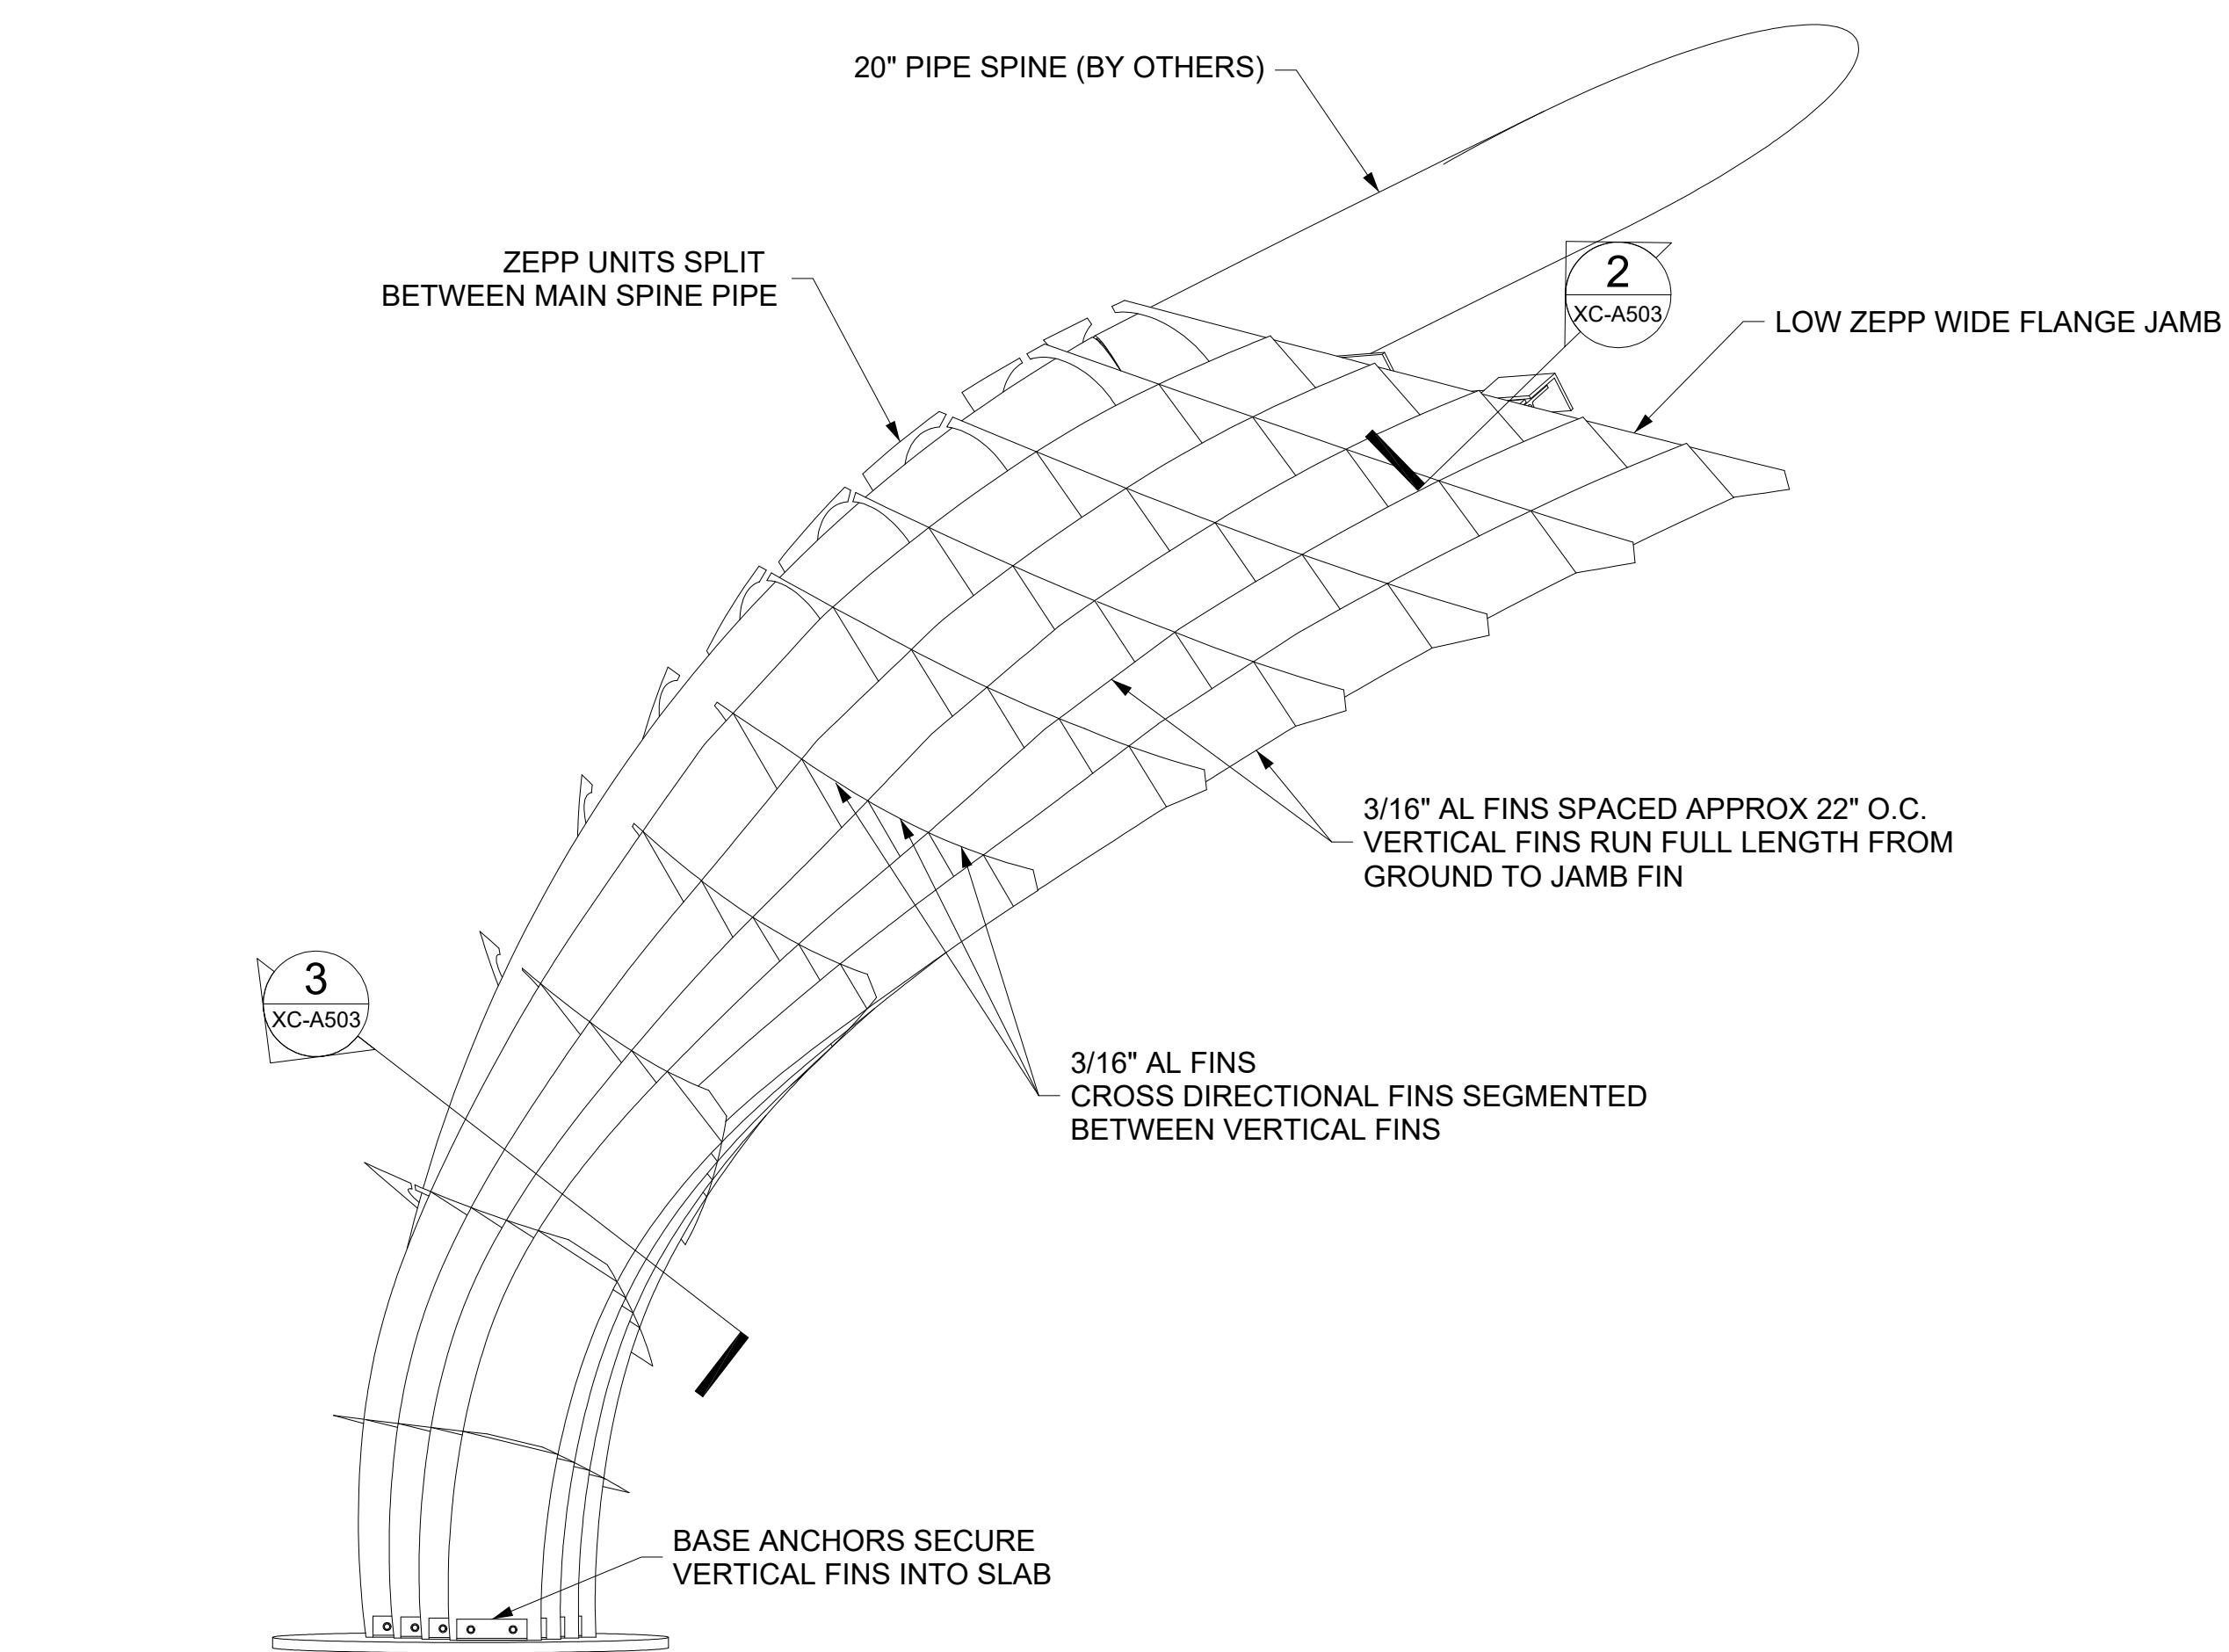


1 WING WALL ZEPP SUB STRUCTURE
 SCALE: 1/2" = 1'-0"
 ZAHNER REF: N/A
 ARCH REF: N/A

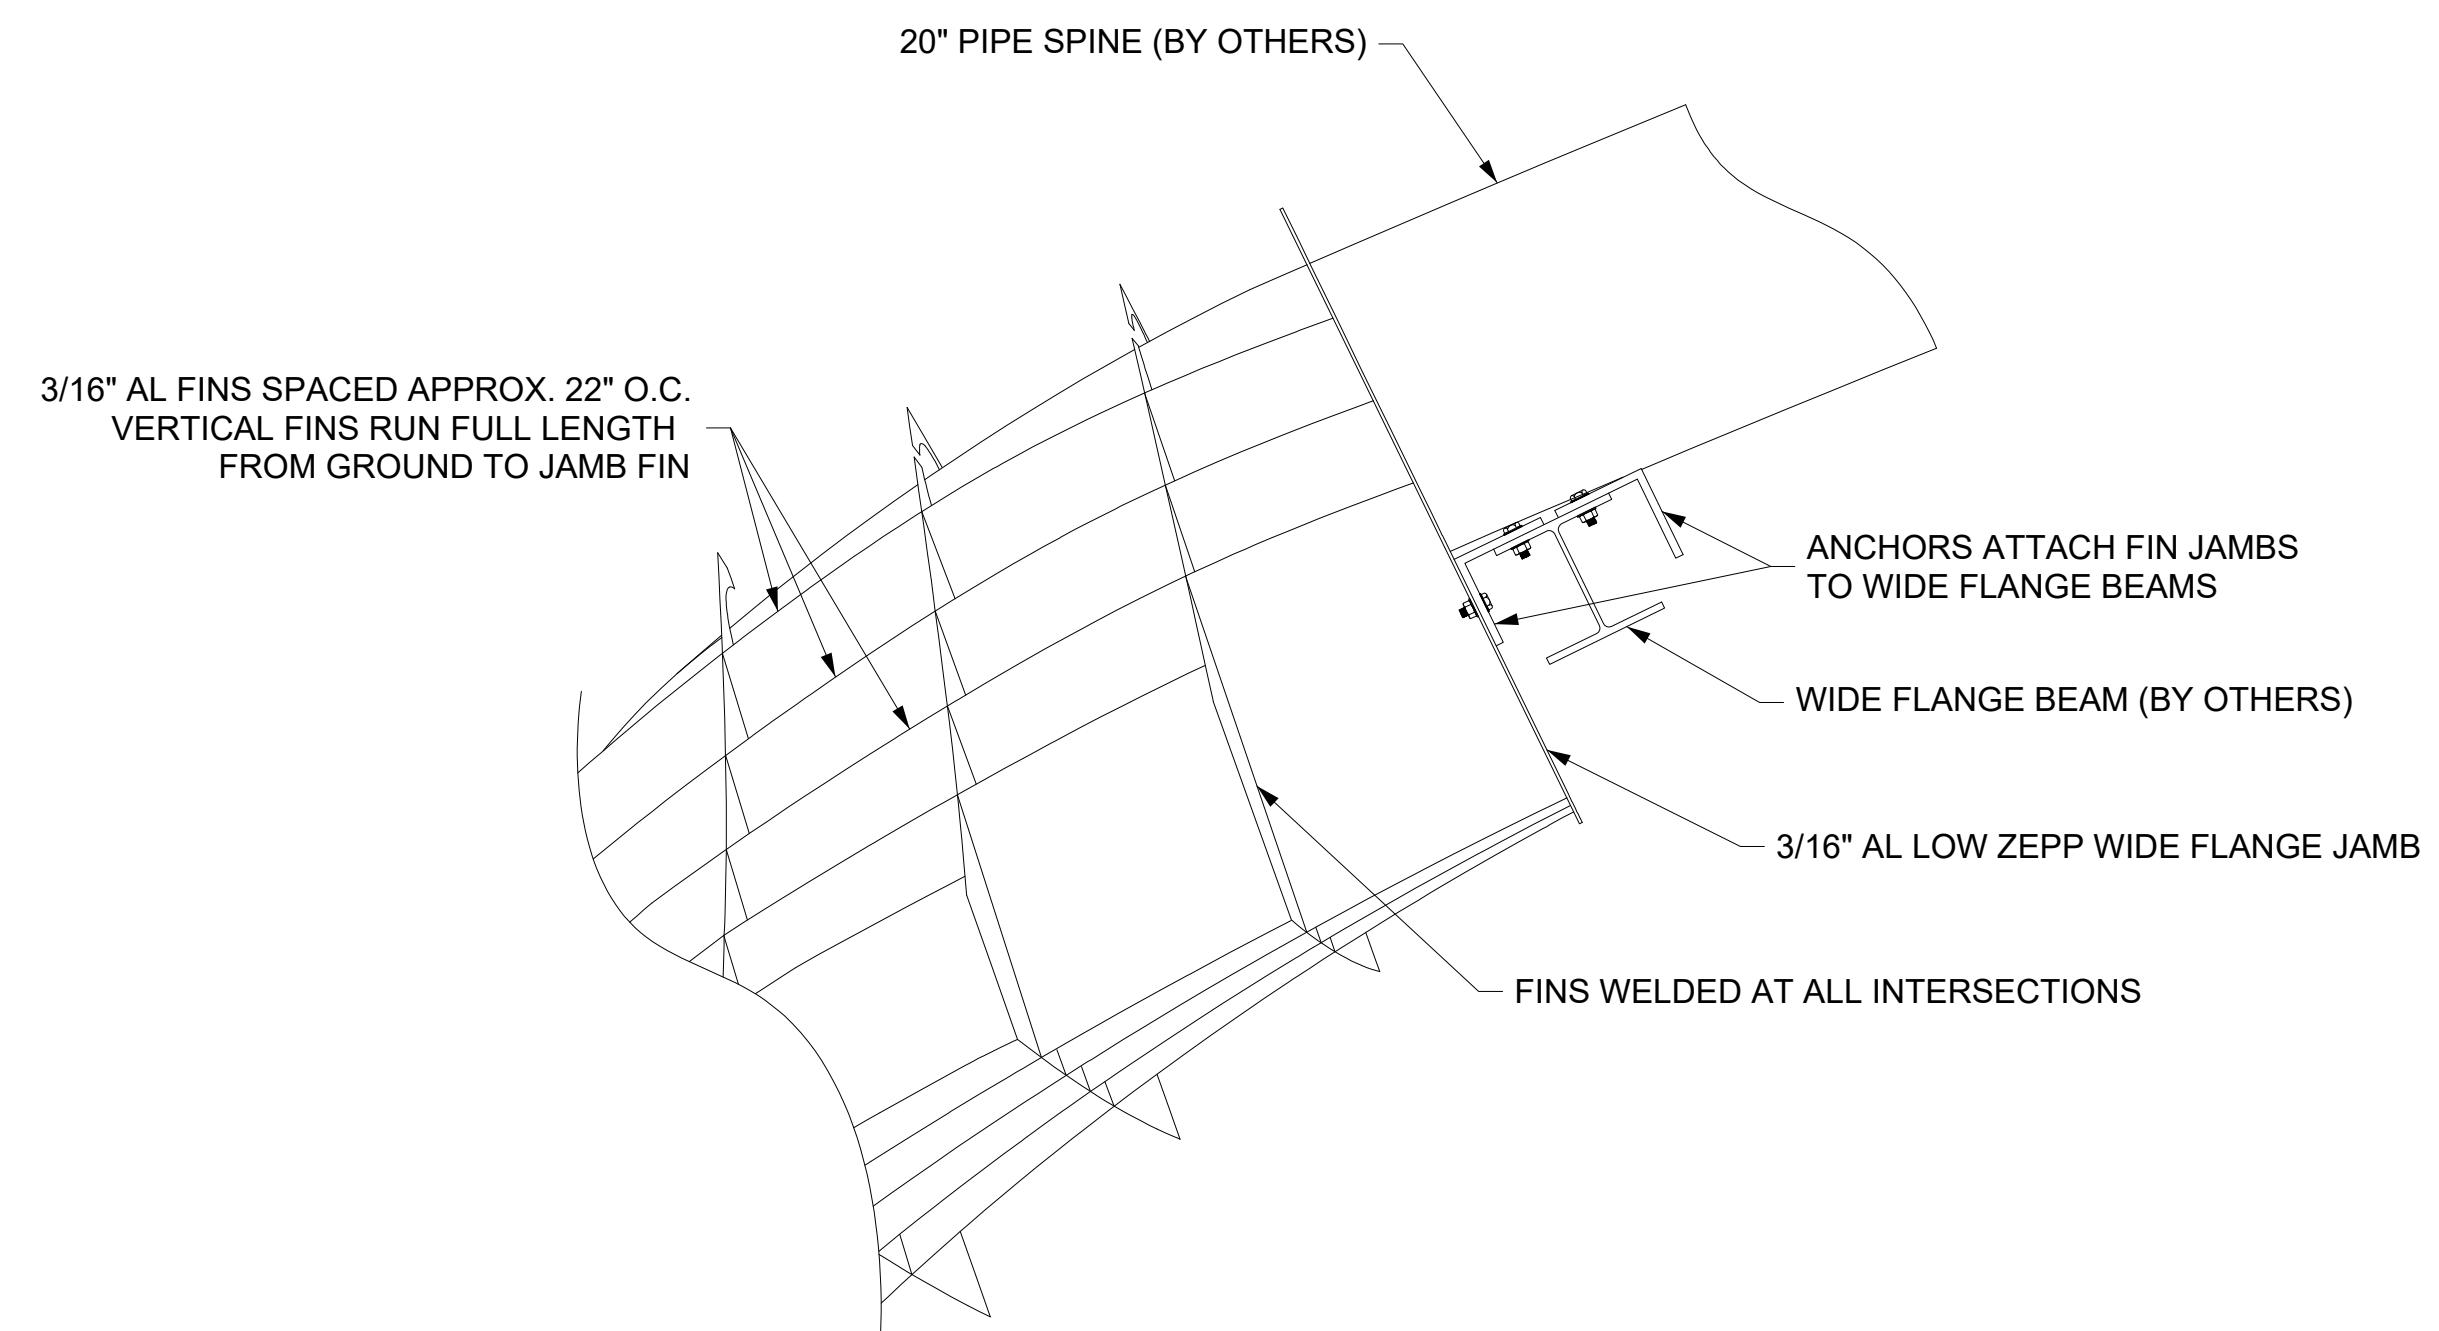

2 WING WALL ZEPP UNIT ATTACHMENT TO STEEL
 SCALE: 1" = 1'-0"
 ZAHNER REF: N/A
 ARCH REF: N/A

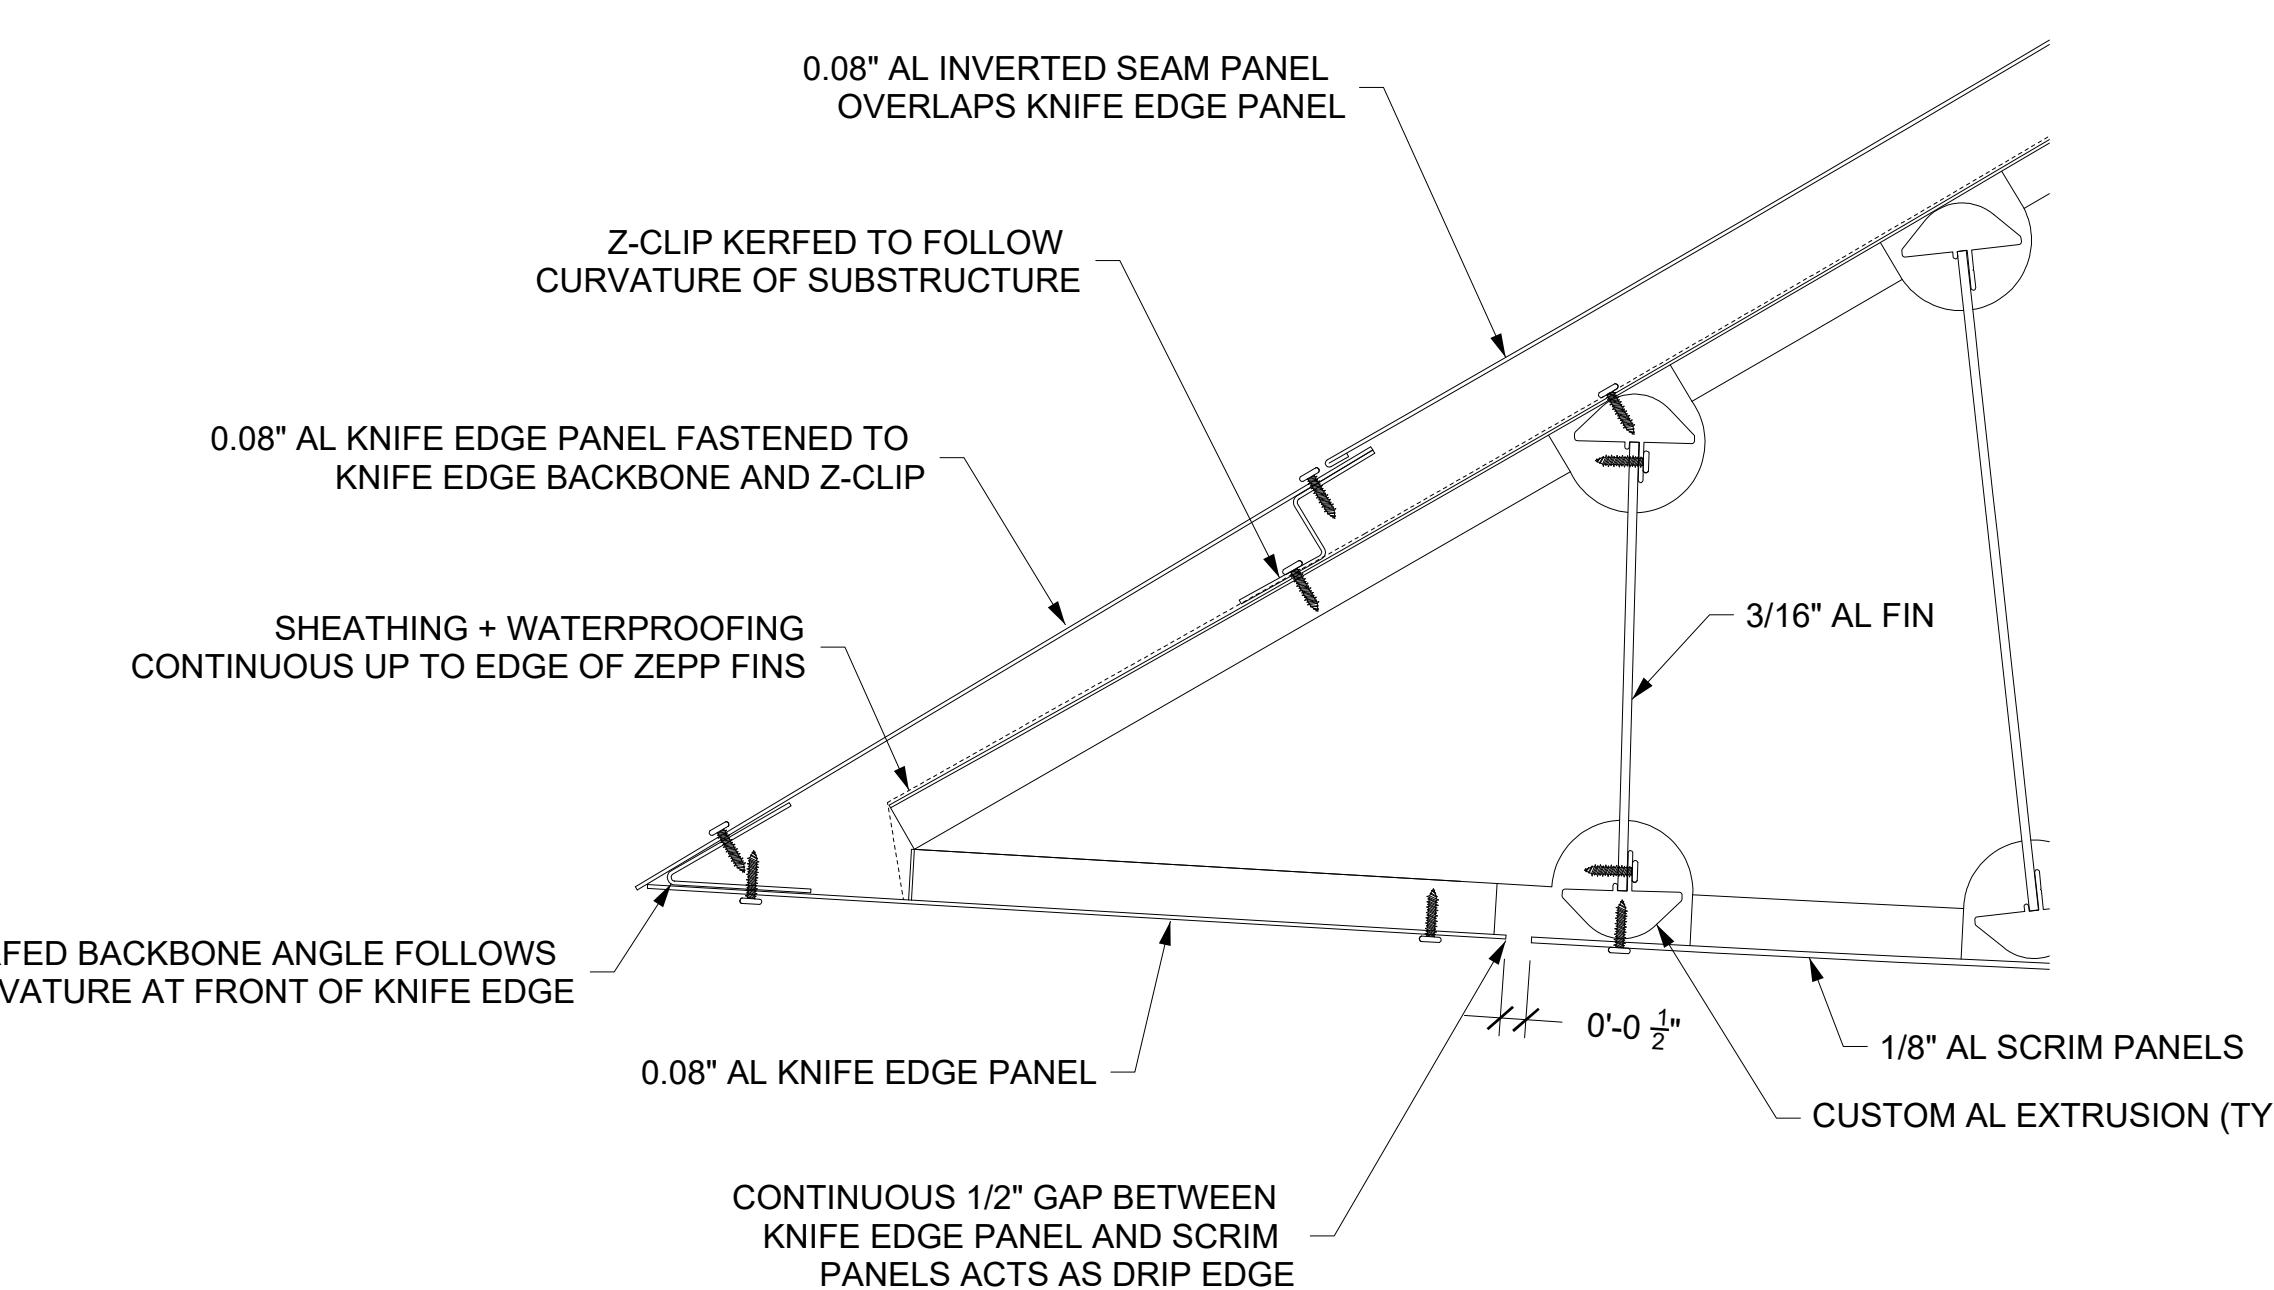


4 KNIFE EDGE DETAILS
 SCALE: 3" = 1'-0"
 ZAHNER REF: N/A
 ARCH REF: N/A

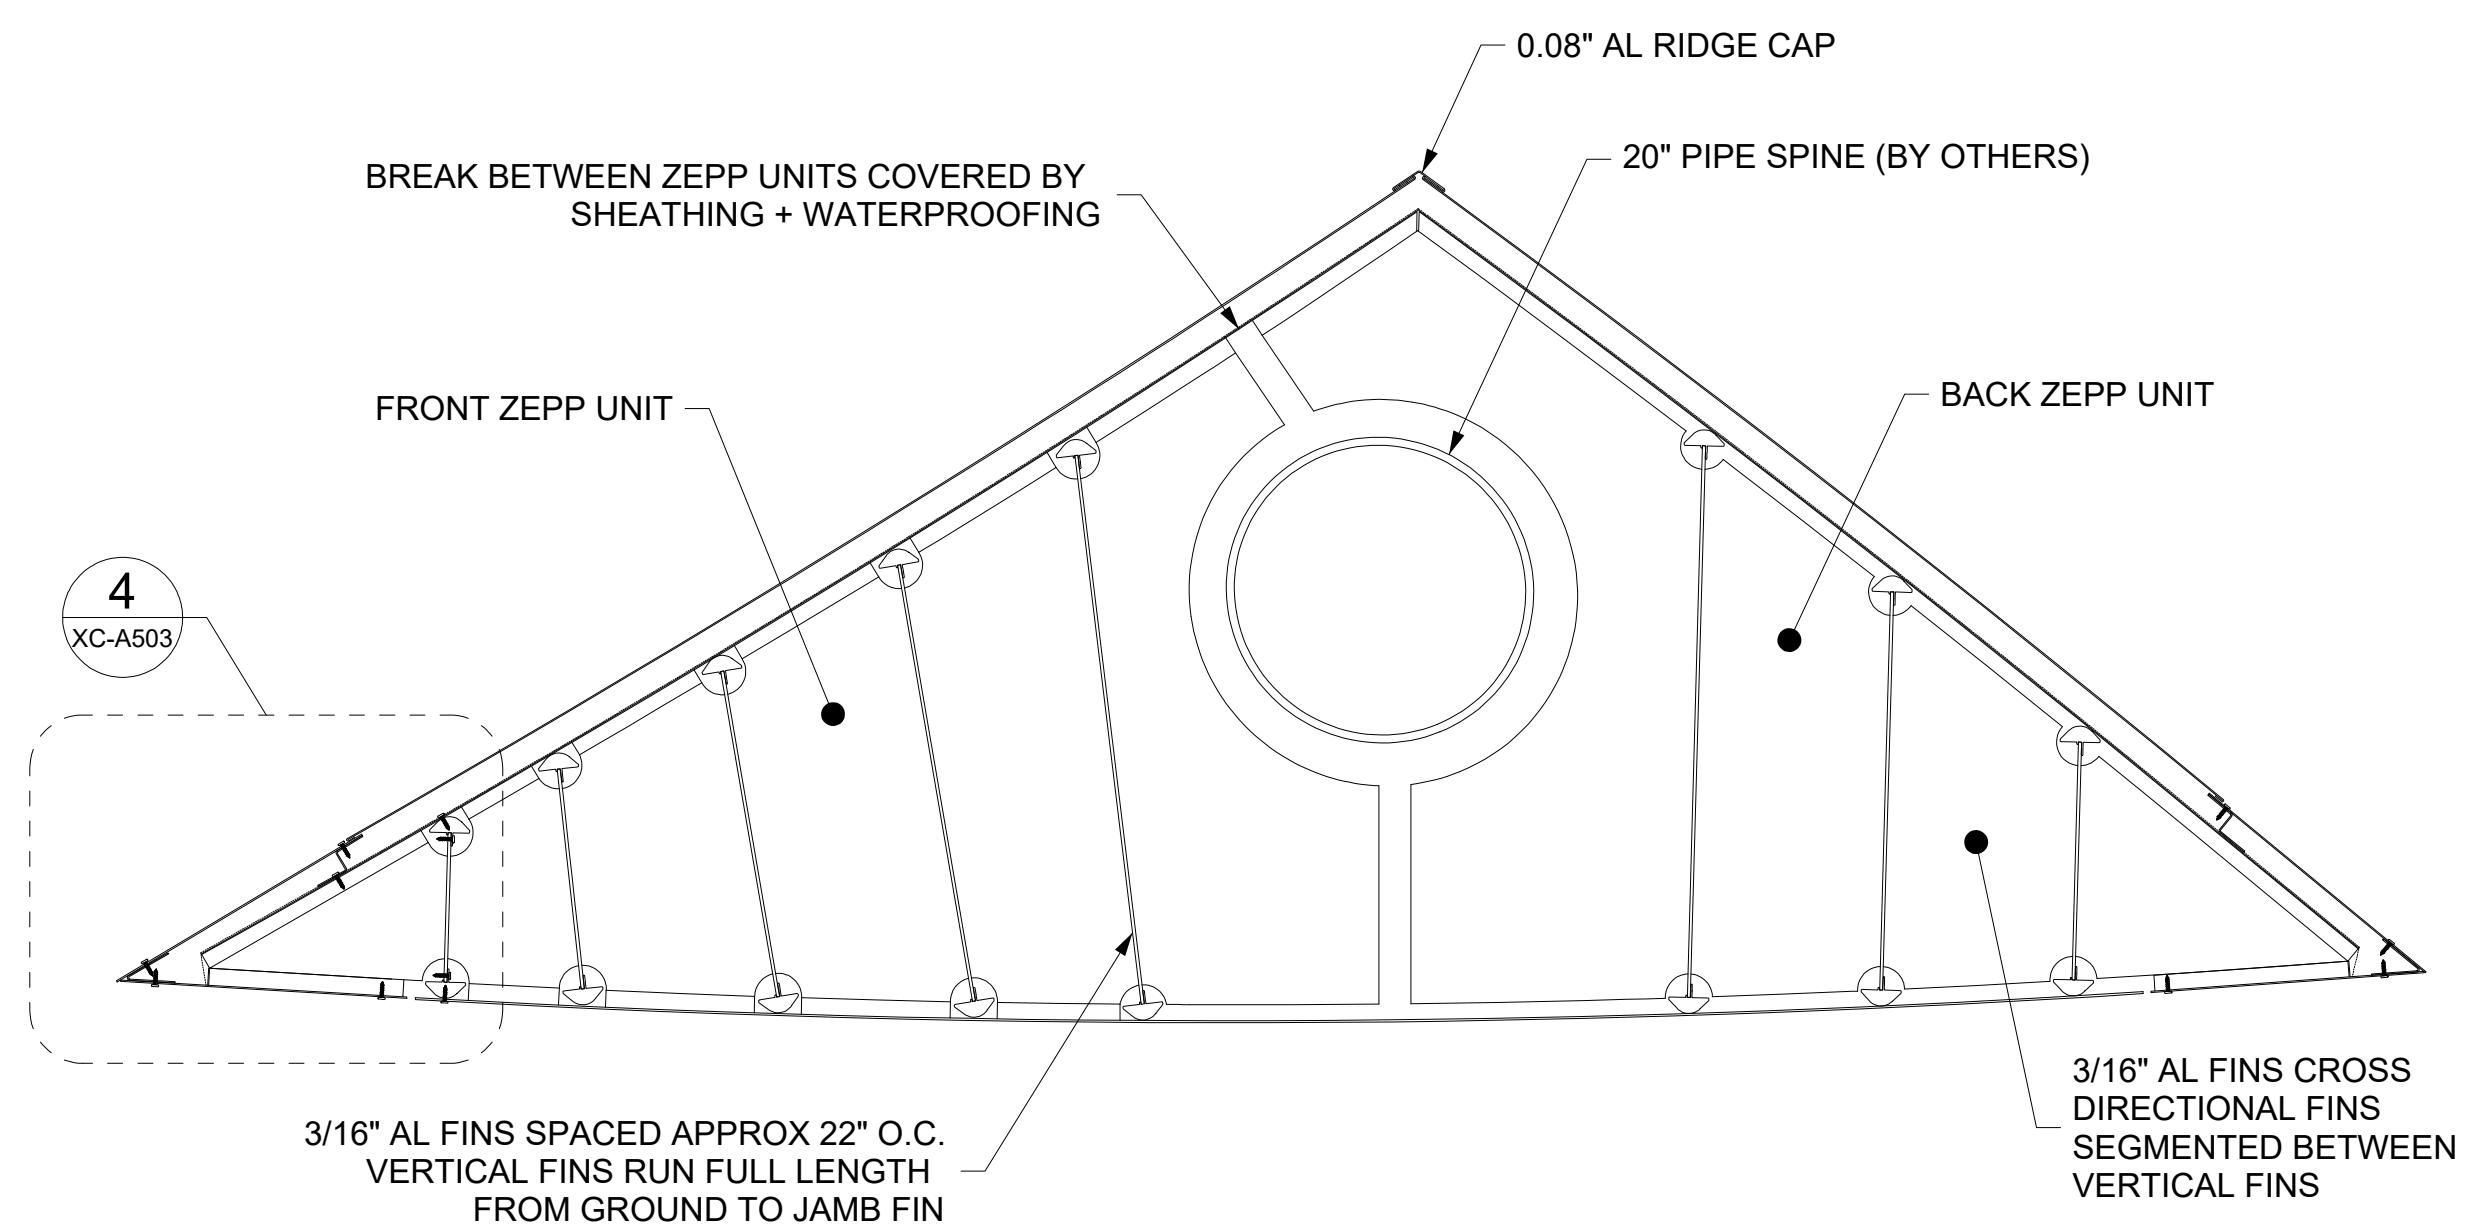

3 SECTION B-B
WING WALL ZEPP TYPICAL CROSS SECTION
 SCALE: ---
 ZAHNER REF: N/A
 ARCH REF: N/A

| SET ISSUE DATES | | |
|------------------------|-------|-------------|
| DATE | ISSUE | |
| 01/20/22 100% DRAWINGS | | |
| | | |
| | | |
| REVISIONS | | |
| NO. | DATE | DESCRIPTION |
| | | |
| | | |




| REVISIONS | | |
|-----------|------|-------------|
| NO. | DATE | DESCRIPTION |
| | | |
| | | |
| | | |

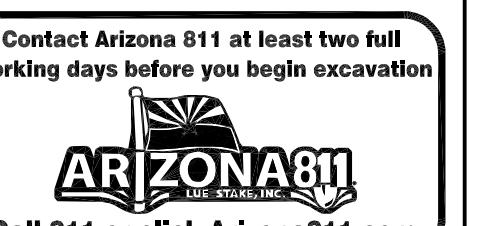


| | | |
|------------------|-----------|--|
| DATE: 01/20/2022 | REVISION: | BY: |
| ENGINEER | | PUBLIC WORKS |
| | | CAPITAL PROJECT MANAGEMENT |
| | | 7447 E. INDIAN SCHOOL RD. SCOTTSDALE, ARIZONA 85251 |
| SHEET TITLE | | |

EAST BOWL - WING WALL ZEPP DETAILS
 PROJECT TITLE: CITY OF SCOTTSDALE CIVIC CENTER PLAZA

| THIS SHEET SCALED FOR 24X36" BORDER | SCALE | DESIGNED | BID NO. | XC-A503 |
|-------------------------------------|----------|----------|-----------------|---------|
| | DRAWN DS | AS-BUILT | COS PROJECT NO. | DG04 |

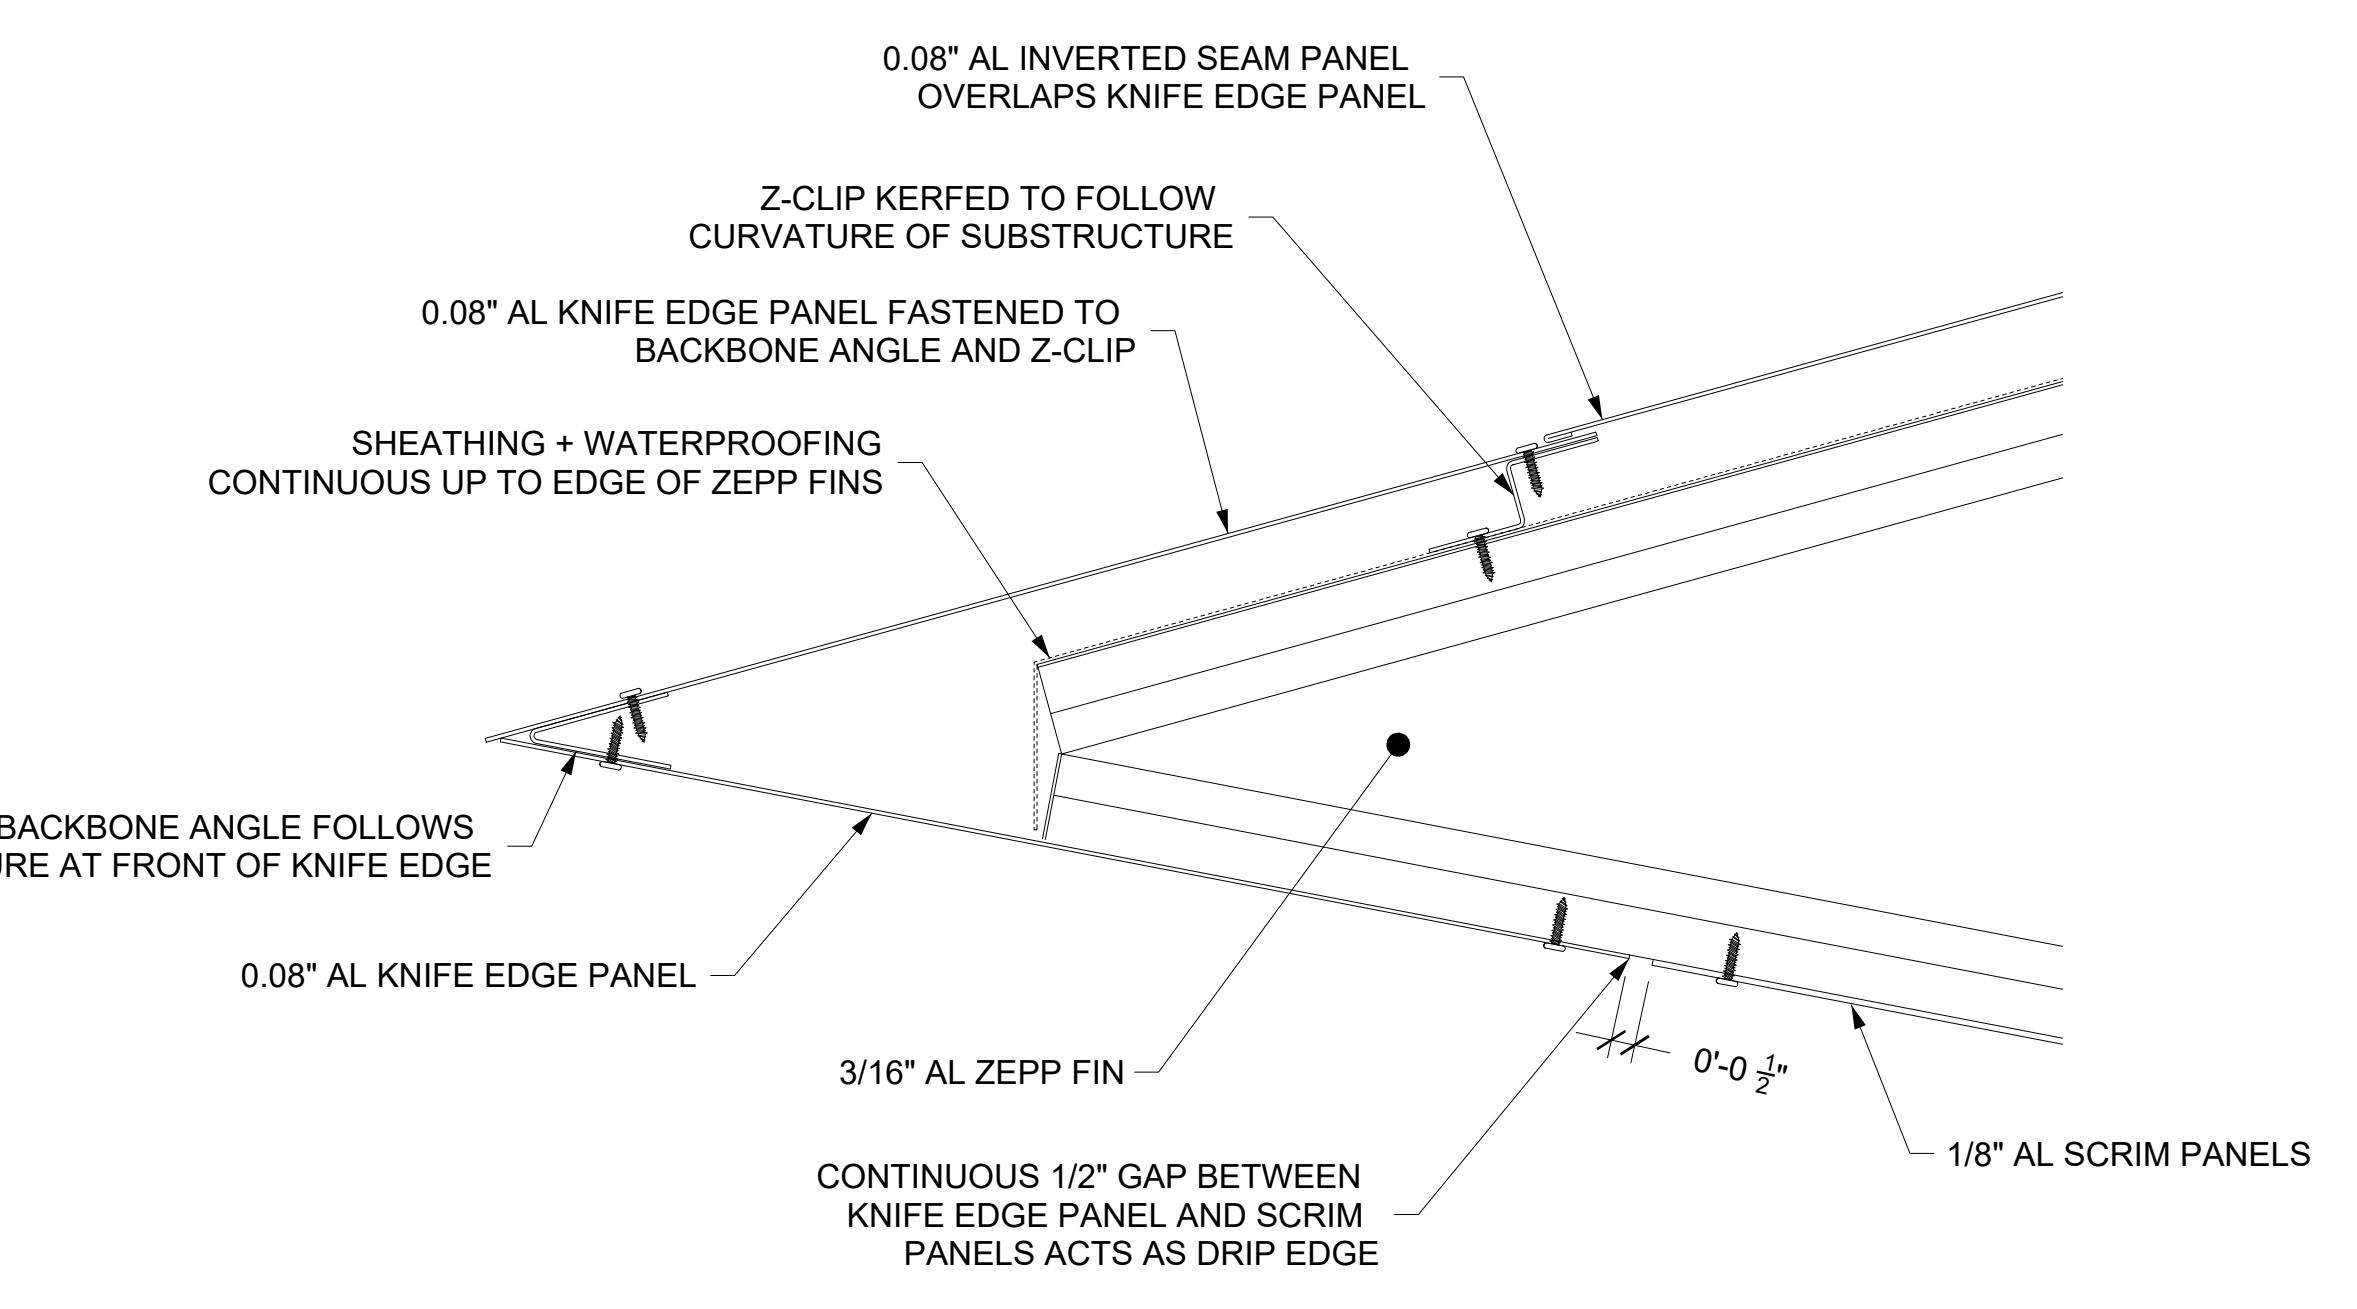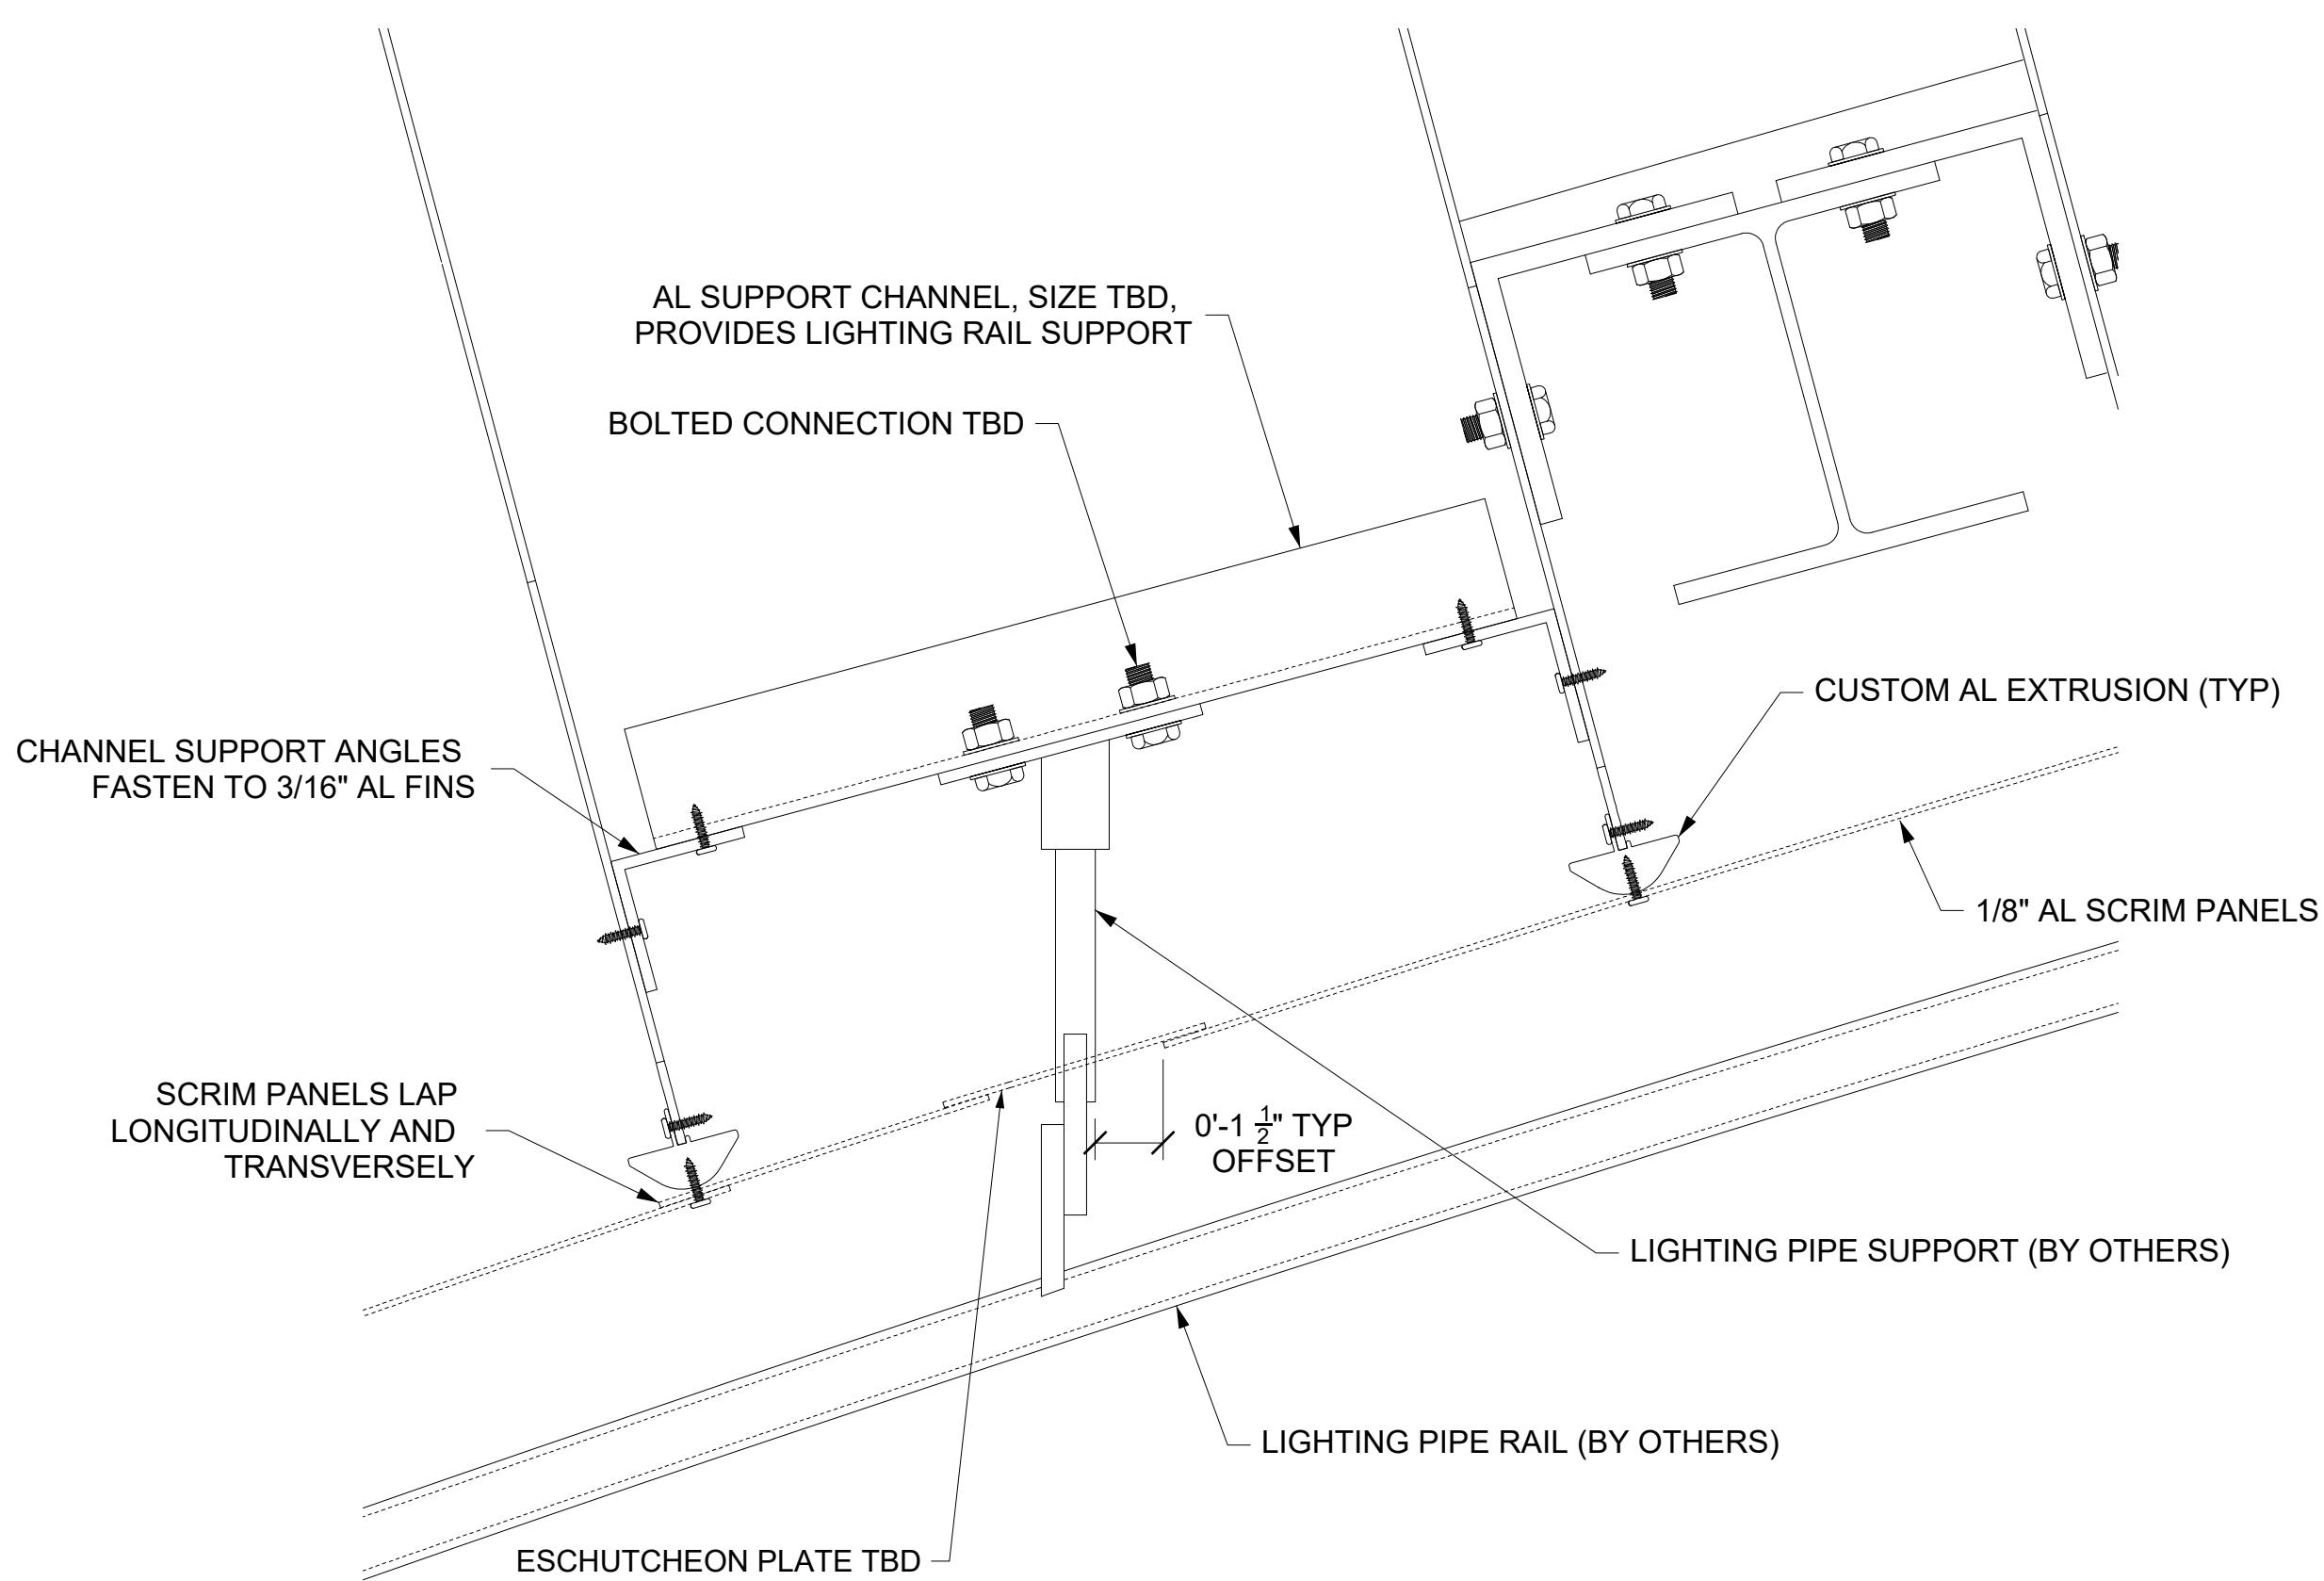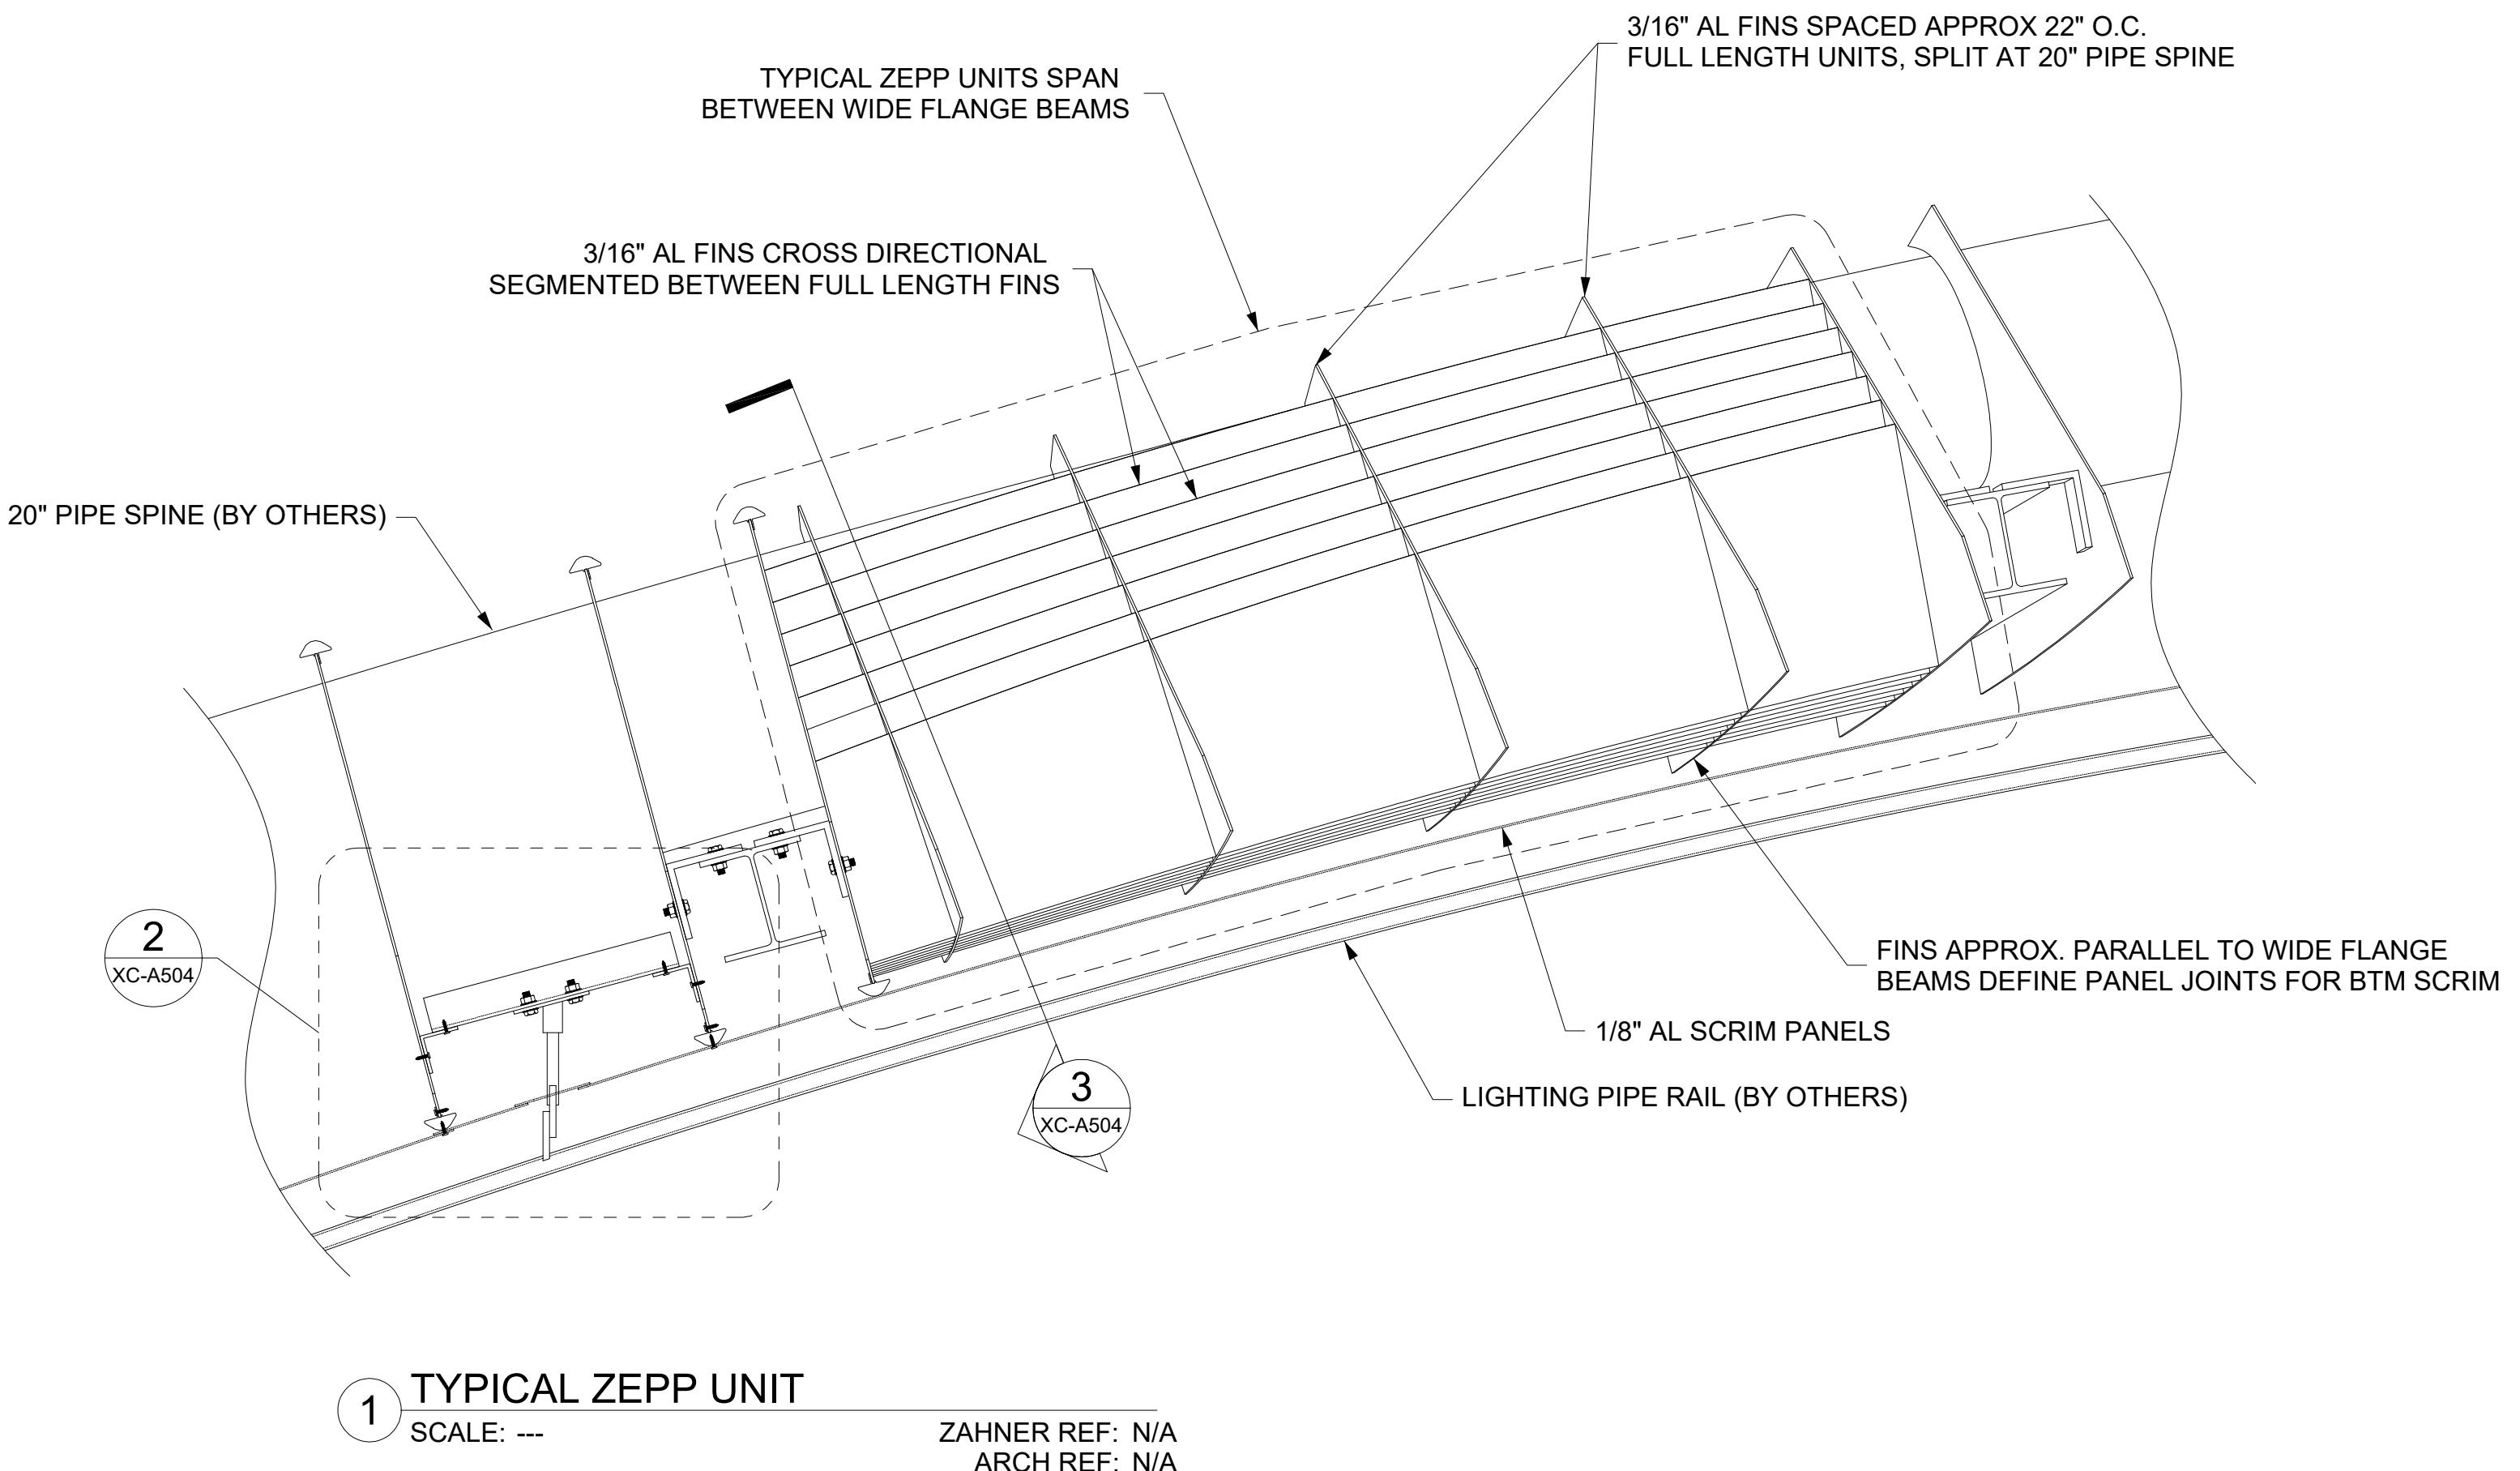


| | | |
|------------------------|-------|-------------|
| SET ISSUE DATES | | |
| DATE | ISSUE | |
| 01/20/22 100% DRAWINGS | | |
| REVISIONS | | |
| NO. | DATE | DESCRIPTION |
| | | |
| | | |

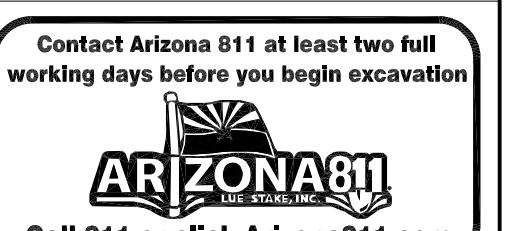

| | | |
|--|-----------|----------------------------|
| DATE: 01/20/2022 | REVISION: | BY: |
| ENGINEER | | |
| | | PUBLIC WORKS |
| | | CAPITAL PROJECT MANAGEMENT |
| 7447 E. INDIAN SCHOOL RD. SCOTTSDALE, ARIZONA 85251 | | |

EAST BOWL - TYP ZEPP DETAILS

| PROJECT TITLE | CITY OF SCOTTSDALE CIVIC CENTER PLAZA | | |
|--|--|-------------|--|
| THIS SHEET SCALED FOR 24X36" BORDER | SCALE | DESIGNED | BID NO. |
| | | DRAWN DS | XC-A504 AS-BUILT COS PROJECT NO. DG04 |

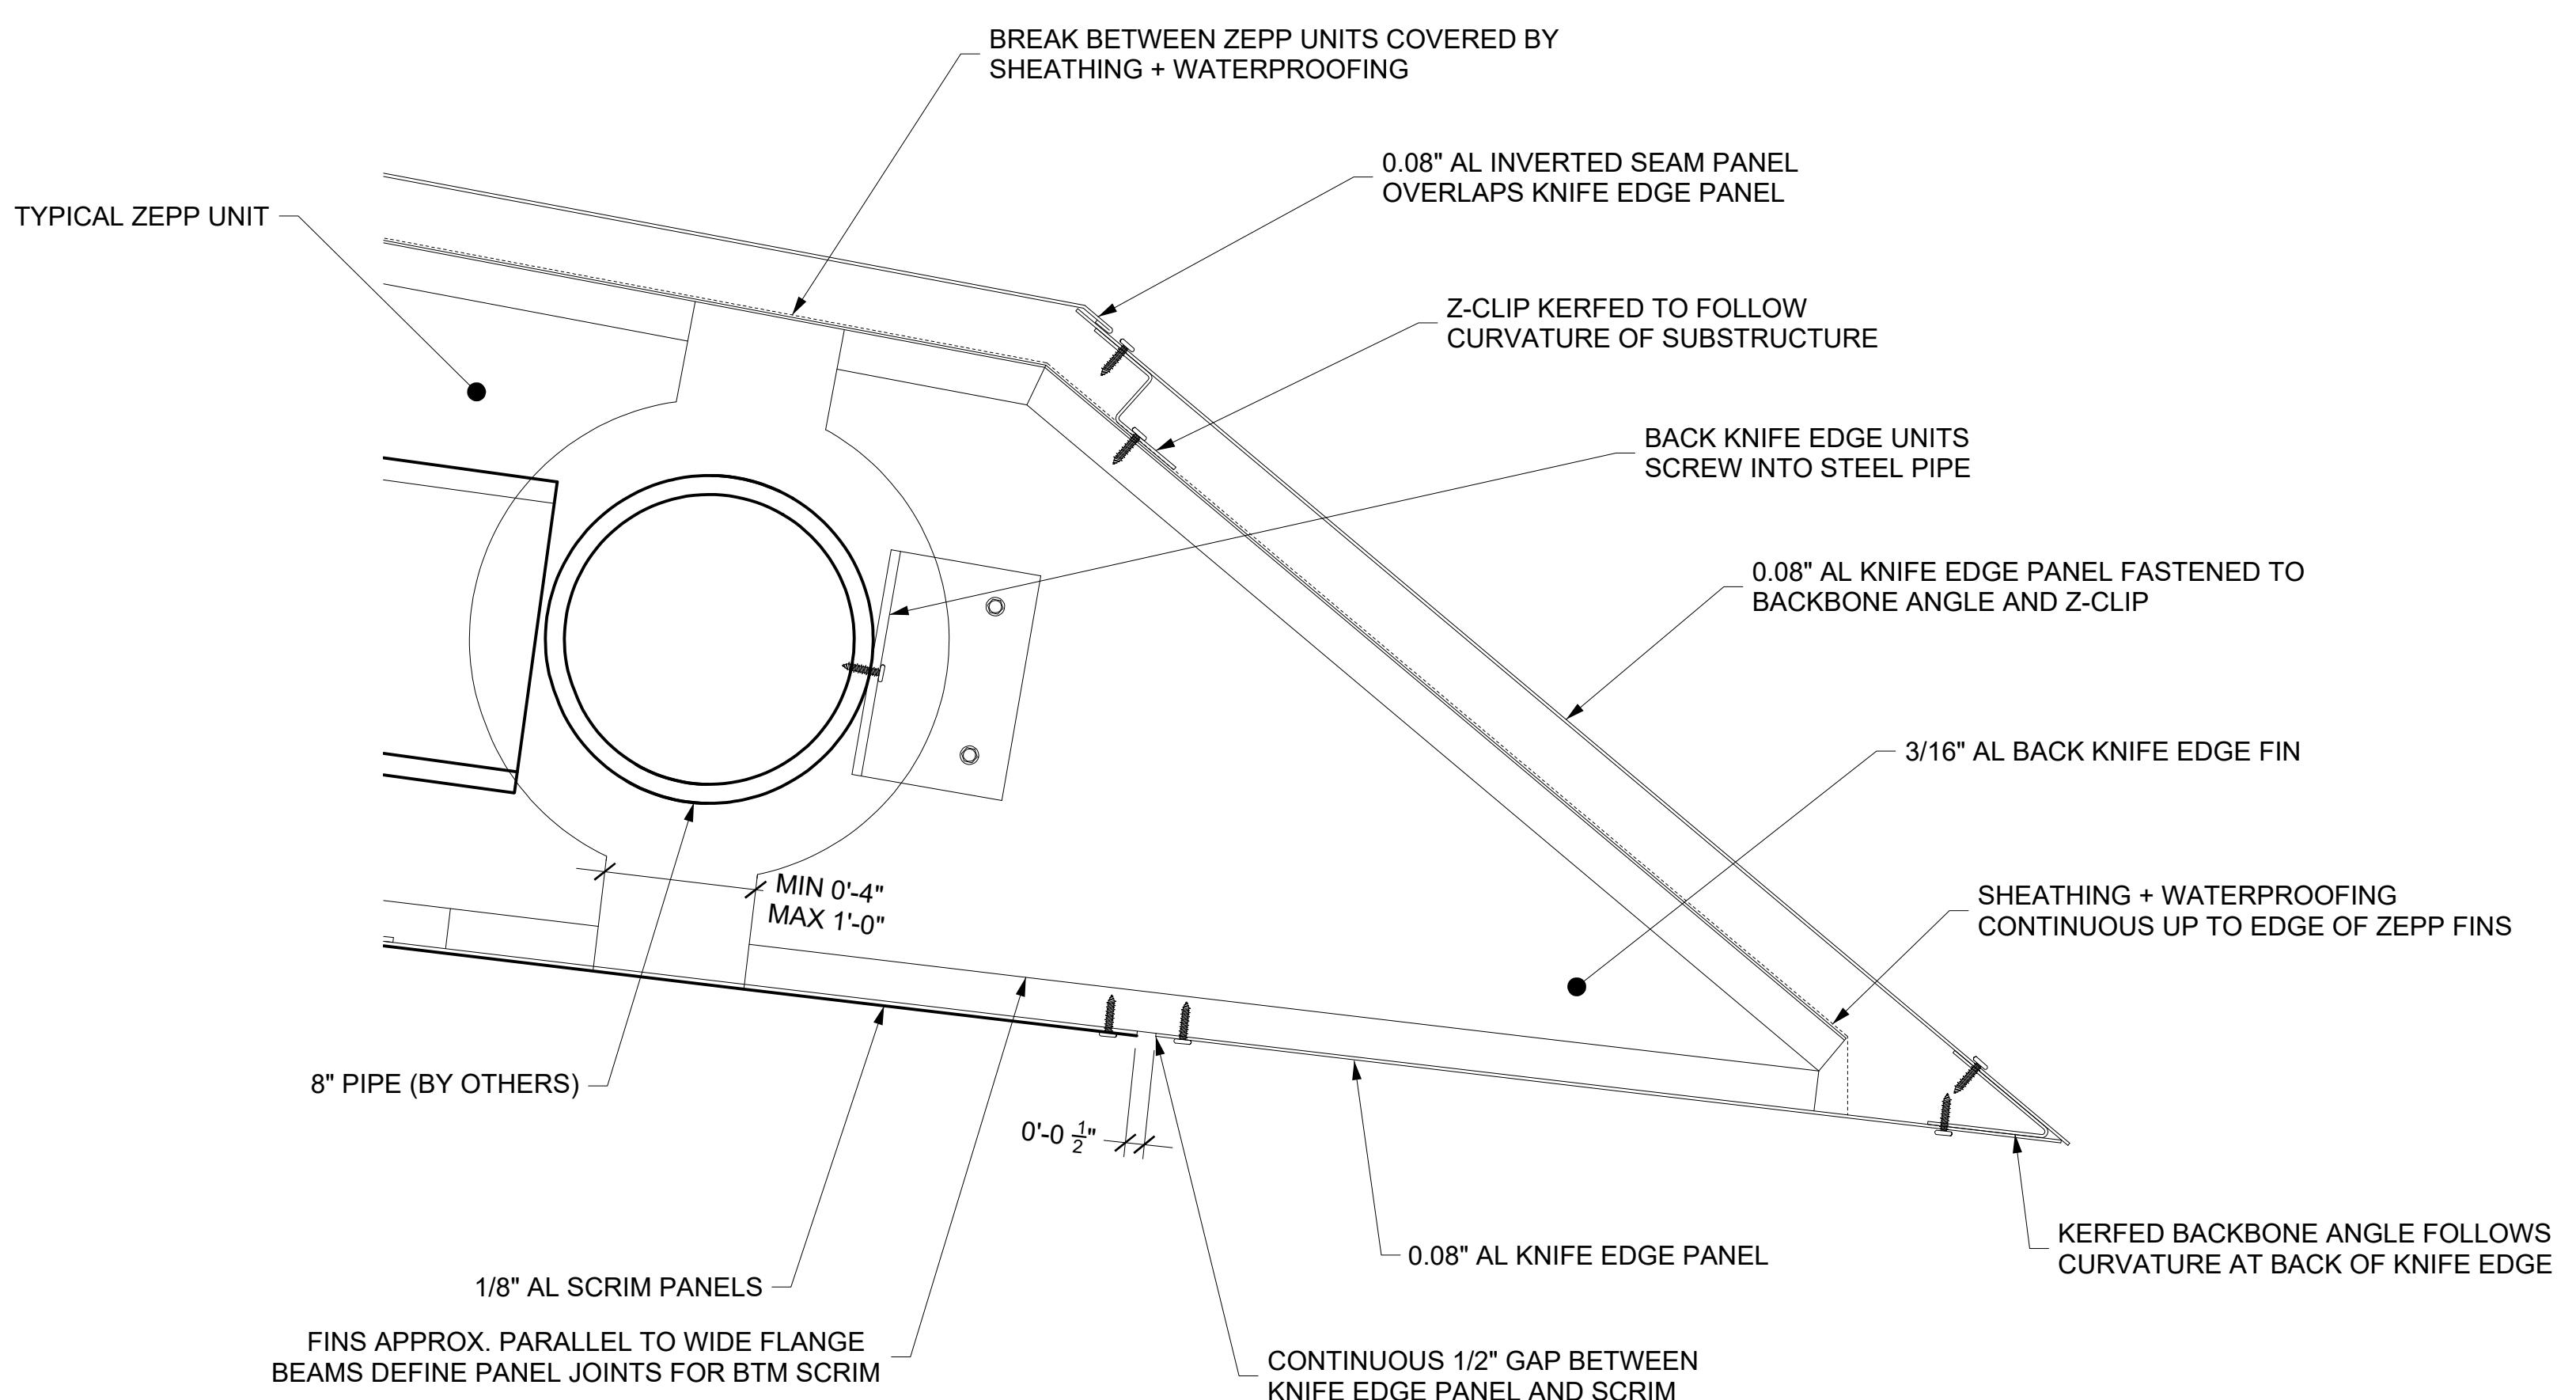

① BACK KNIFE EDGE DETAIL

SCALE: 3' = 1'-0"

ZAHNER REF: N/A
ARCH REF: N/A

| | |
|------------------------|-------|
| SET ISSUE DATES | |
| DATE | ISSUE |
| 01/20/22 100% DRAWINGS | |
| | |
| | |
| | |
| | |


| | | |
|-----------|------|-------------|
| REVISIONS | | |
| NO. | DATE | DESCRIPTION |
| | | |
| | | |
| | | |
| | | |



| | | | |
|------------------|--|--|-----|
| DATE: 01/20/2022 | | REVISION: | BY: |
| | | | |
| ENGINEER | | PUBLIC WORKS | |
| | | CAPITAL PROJECT MANAGEMENT | |
| | | 7447 E. INDIAN SCHOOL RD. SCOTTSDALE, ARIZONA 85251 | |
| SHEET TITLE | | | |

| | | | |
|--|--|--|--|
| PROJECT TITLE | | | |
| CITY OF SCOTTSDALE CIVIC CENTER PLAZA | | | |


| | | | | |
|--|-------------|----------|-------------------------|---------|
| THIS SHEET SCALED FOR 24X36" BORDER | SCALE | DESIGNED | BID NO. | XC-A505 |
| | DRAWN DS | AS-BUILT | COS PROJECT NO. DG04 | |

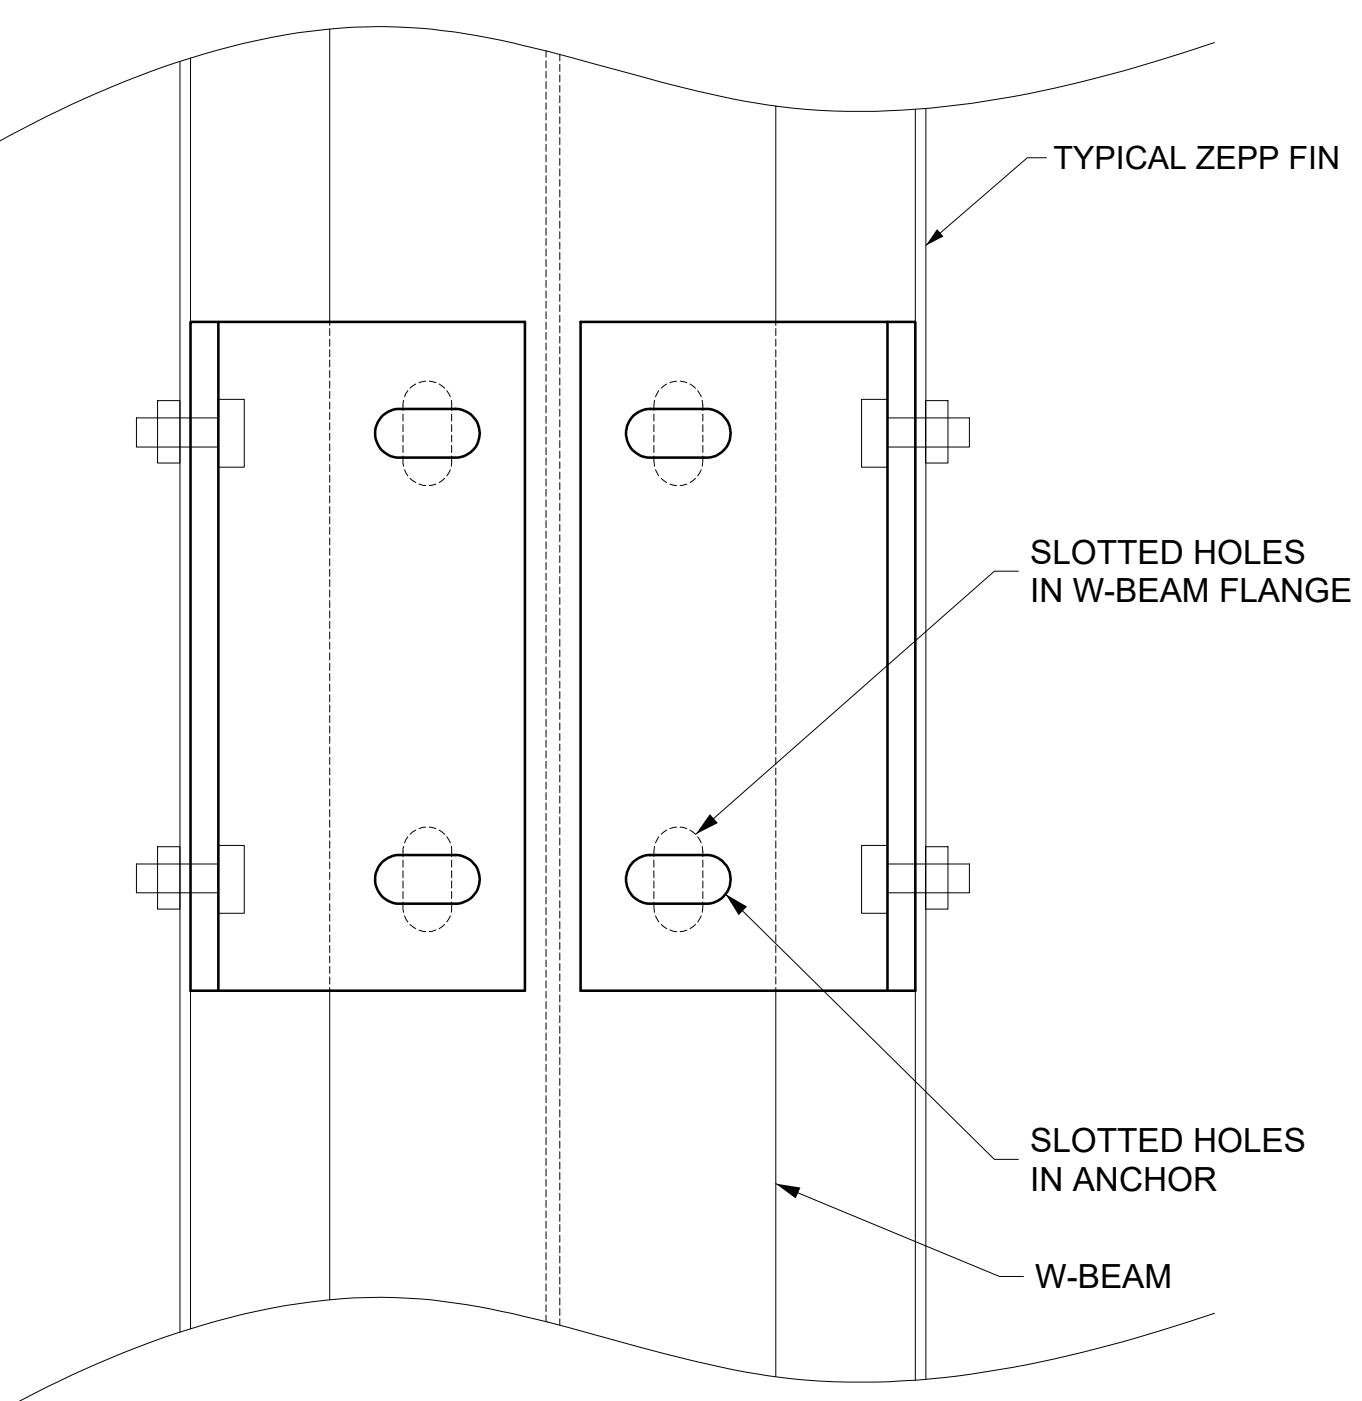

SECTION A-A

SCALE: --


ZAHNER REF: N/A
ARCH REF: N/A

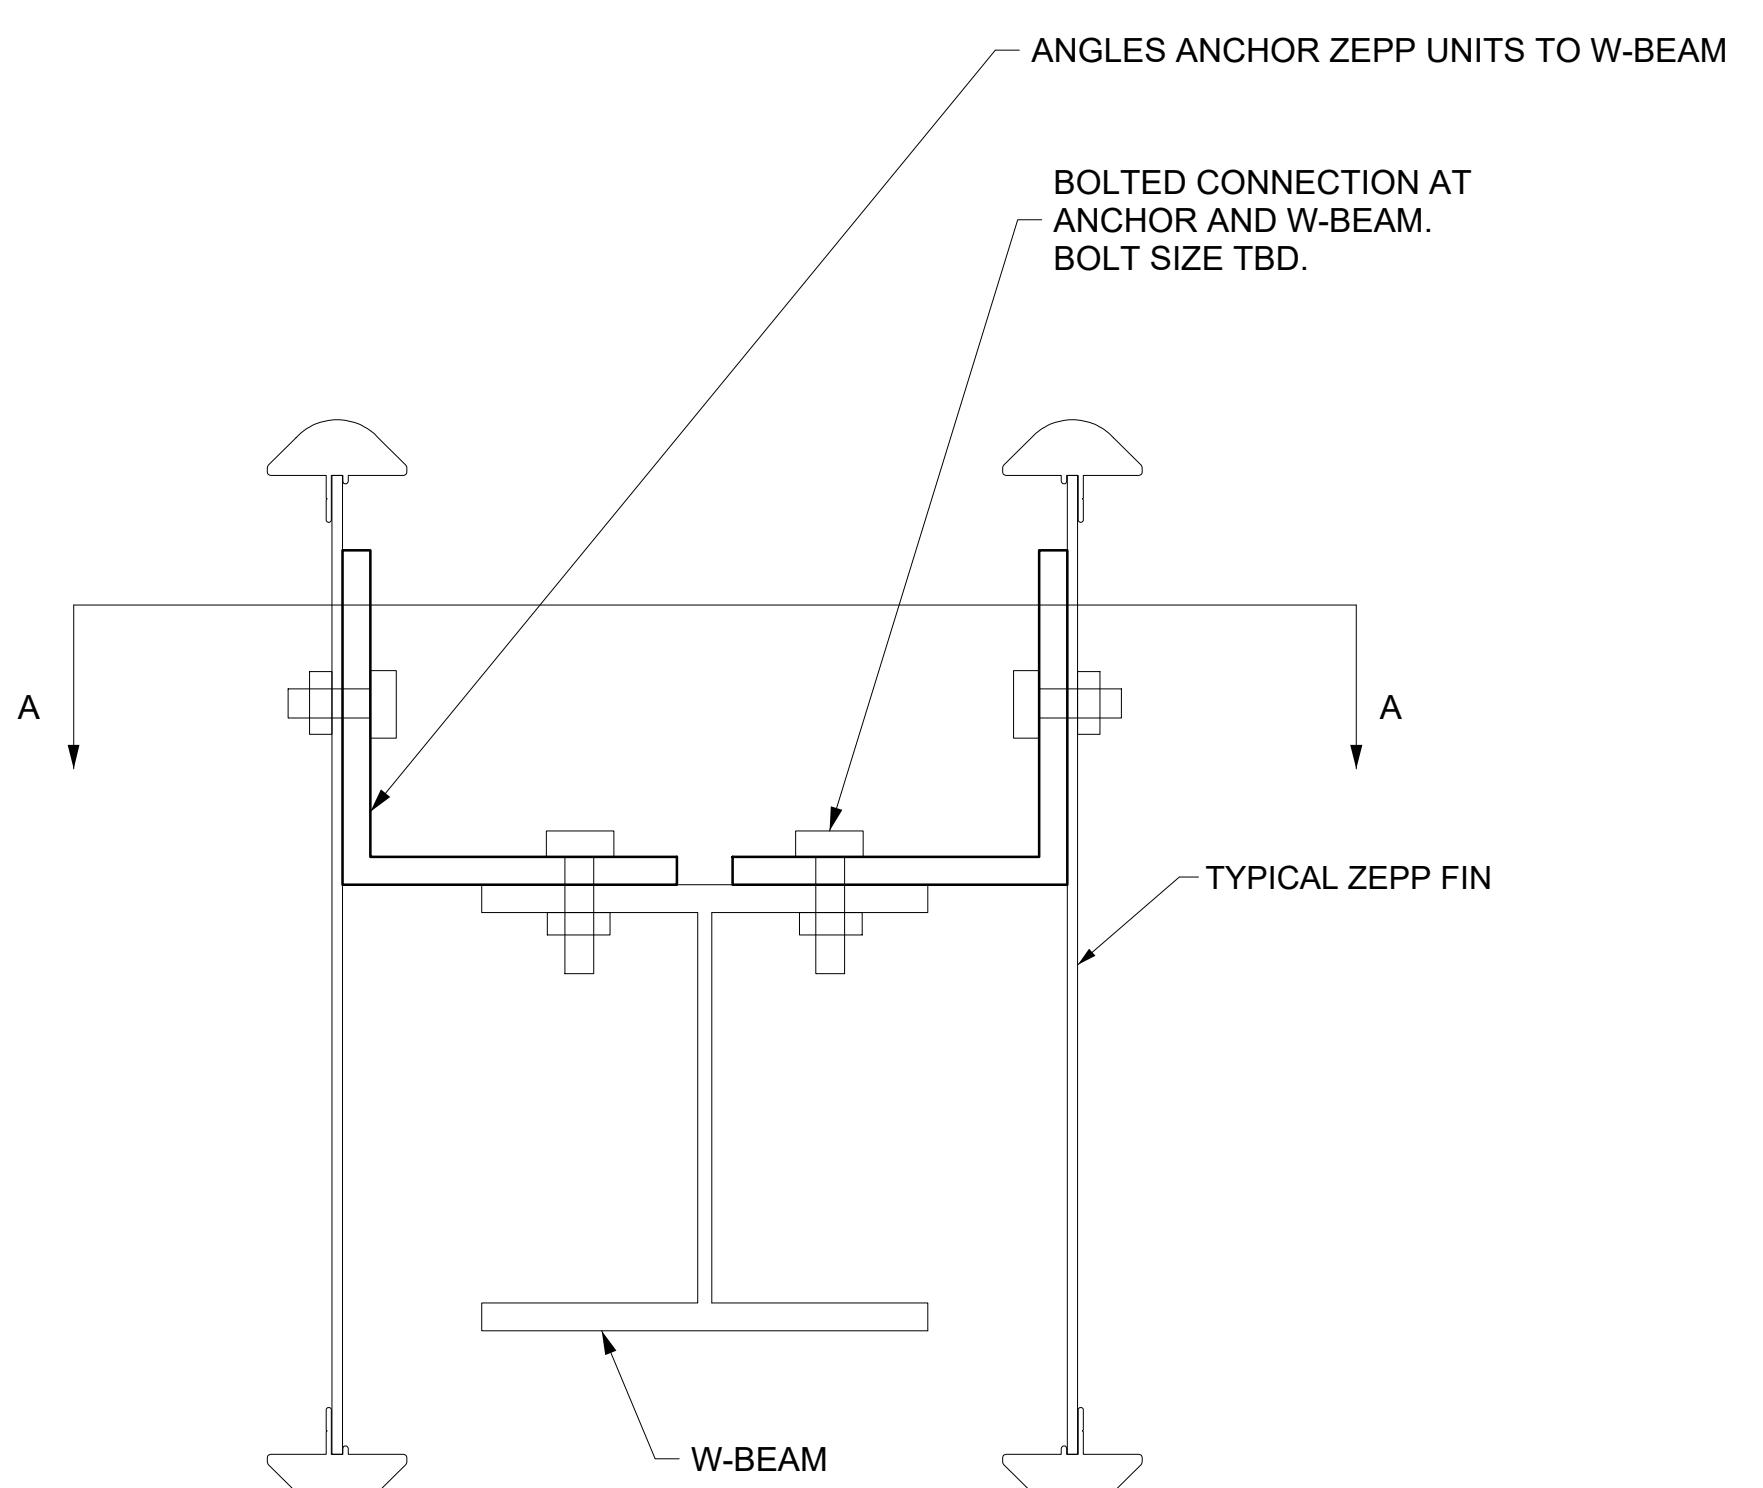


ANCHOR DETAIL SCALE: ---

2 SCALE

ZAHNER REF: N/A
ARCH REF: N/A
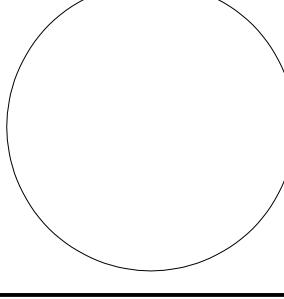
| SET ISSUE DATES | | | | |
|--|----------|---|-------------------------|---------|
| DATE | ISSUE | | | |
| 01/20/22 100% DRAWINGS | | | | |
| <hr/> <hr/> <hr/> <hr/> <hr/> | | | | |
| REVISIONS | | | | |
| NO. | DATE | DESCRIPTION | | |
| | | <hr/> <hr/> <hr/> <hr/> <hr/> | | |
| <div style="text-align: right; padding: 10px;"> <p>Contact Arizona 811 at least two full working days before you begin excavation</p>  <p>Call 811 or click Arizona811.com</p> </div> | | | | |
| DATE: 01/20/2022 | | REVISION: | | BY: |
| ENGINEER  | | PUBLIC WORKS  CAPITAL PROJECT MANAGEMENT <small>7447 E. INDIAN SCHOOL RD. SCOTTSDALE, ARIZONA 85251</small> | | |
| SHEET TITLE | | | | |
| <h1>EAST BOWL - ANCHOR DETAILS</h1> | | | | |
| PROJECT TITLE | | CITY OF SCOTTSDALE CIVIC CENTER PLAZA | | |
| D R | SCALE | DESIGNED | BID NO. | |
| | DRAWN DS | AS-BUILT | COS PROJECT NO. DG04 | |
| | | | | XC-A506 |

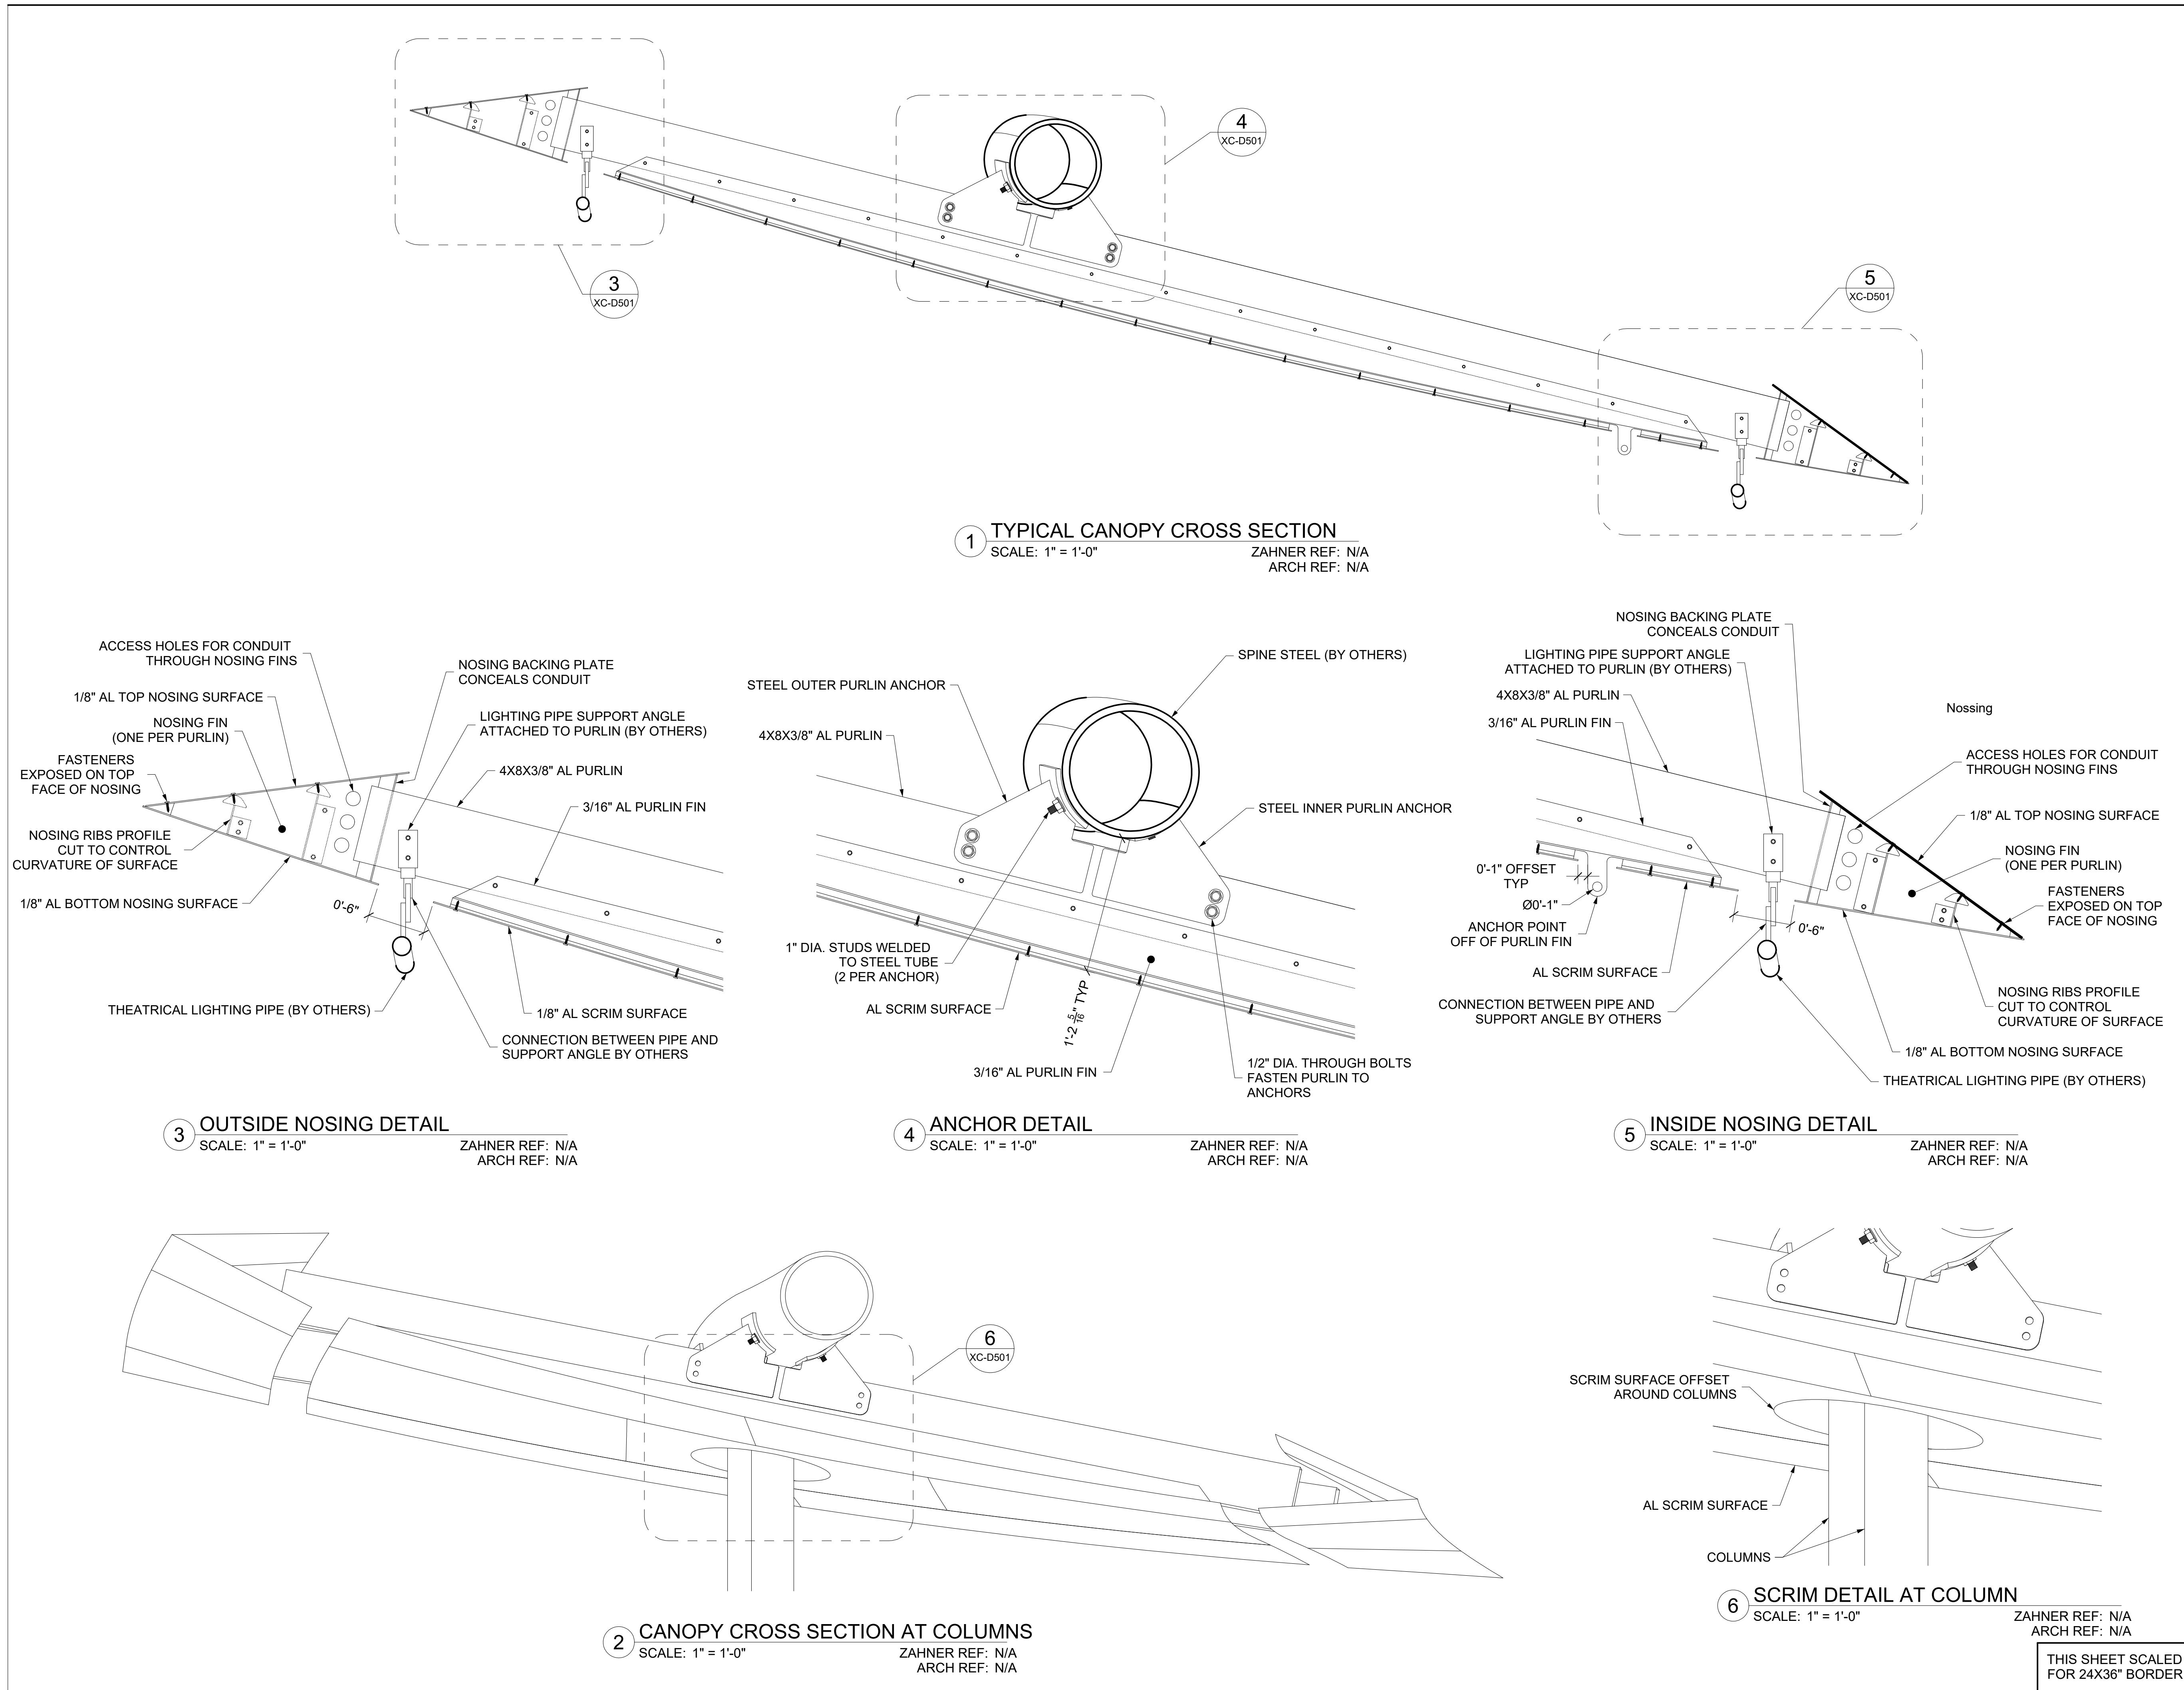

The logo features a stylized graphic on the left composed of three horizontal bars of increasing height from top to bottom, with a vertical bar to their left. To the right of this graphic, the company name "RITOCH-POWELL" is written in a large, bold, black sans-serif font. Below it, "& Associates" is written in a slightly smaller, bold, black sans-serif font. At the bottom, the phone number "602-263-1177" and website "WWW.RPAENG.COM" are displayed in a smaller, bold, black sans-serif font.


L A K E | F L A T O


© 2021 Lake|Flato Architects, Inc.


311 THIRD STREET
SAN ANTONIO, TEXAS 78205
P 210.227.3335 F 210.224.9515
www.lakeflato.com

ZAHNER

ARCHITECTURAL METAL

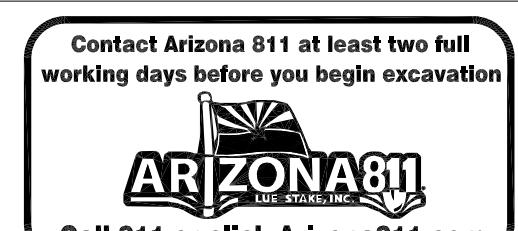

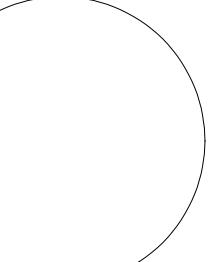
| | | | |
|---|--|--|-------------------------|
| DATE: 01/20/2022 | REVISION: | BY: | |
| ENGINEER  |  <p>PUBLIC WORKS CAPITAL PROJECT MANAGEMENT</p> <p>7447 E. INDIAN SCHOOL RD. SCOTTSDALE, ARIZONA 85251</p> | | |
| SHEET TITLE | | | |
| 360 CANOPY - TYPICAL CANOPY SECTION DETAILS | | | |
| PROJECT TITLE | | CITY OF SCOTTSDALE CIVIC CENTER PLAZA | |
| SCALE | DESIGNED | BID NO. | XC-D501 |
| | DRAWN DS | AS-BUILT | COS PROJECT NO. DG04 |

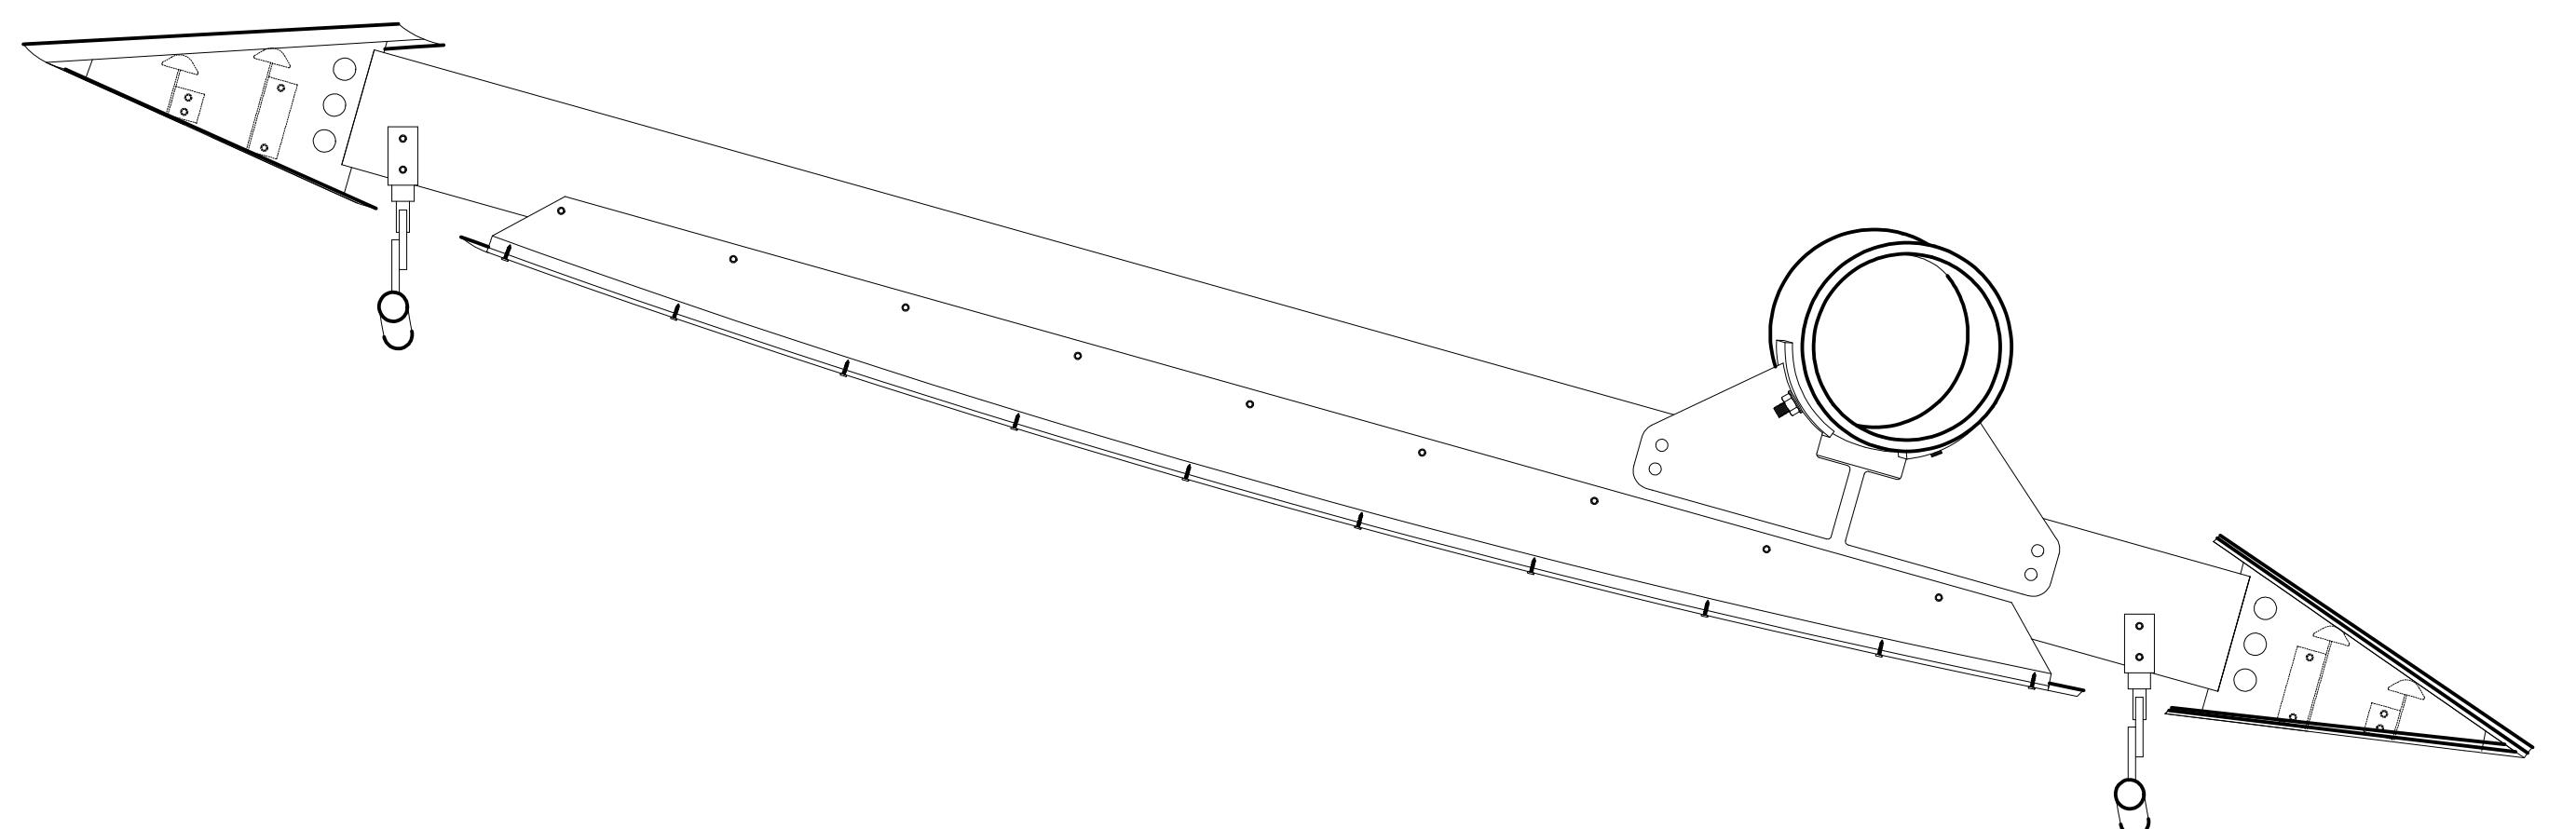

① CANOPY CROSS SECTION AT WALKING PATH


SCALE: 1" = 1'-0"
ZAHNER REF: N/A
ARCH REF: N/A

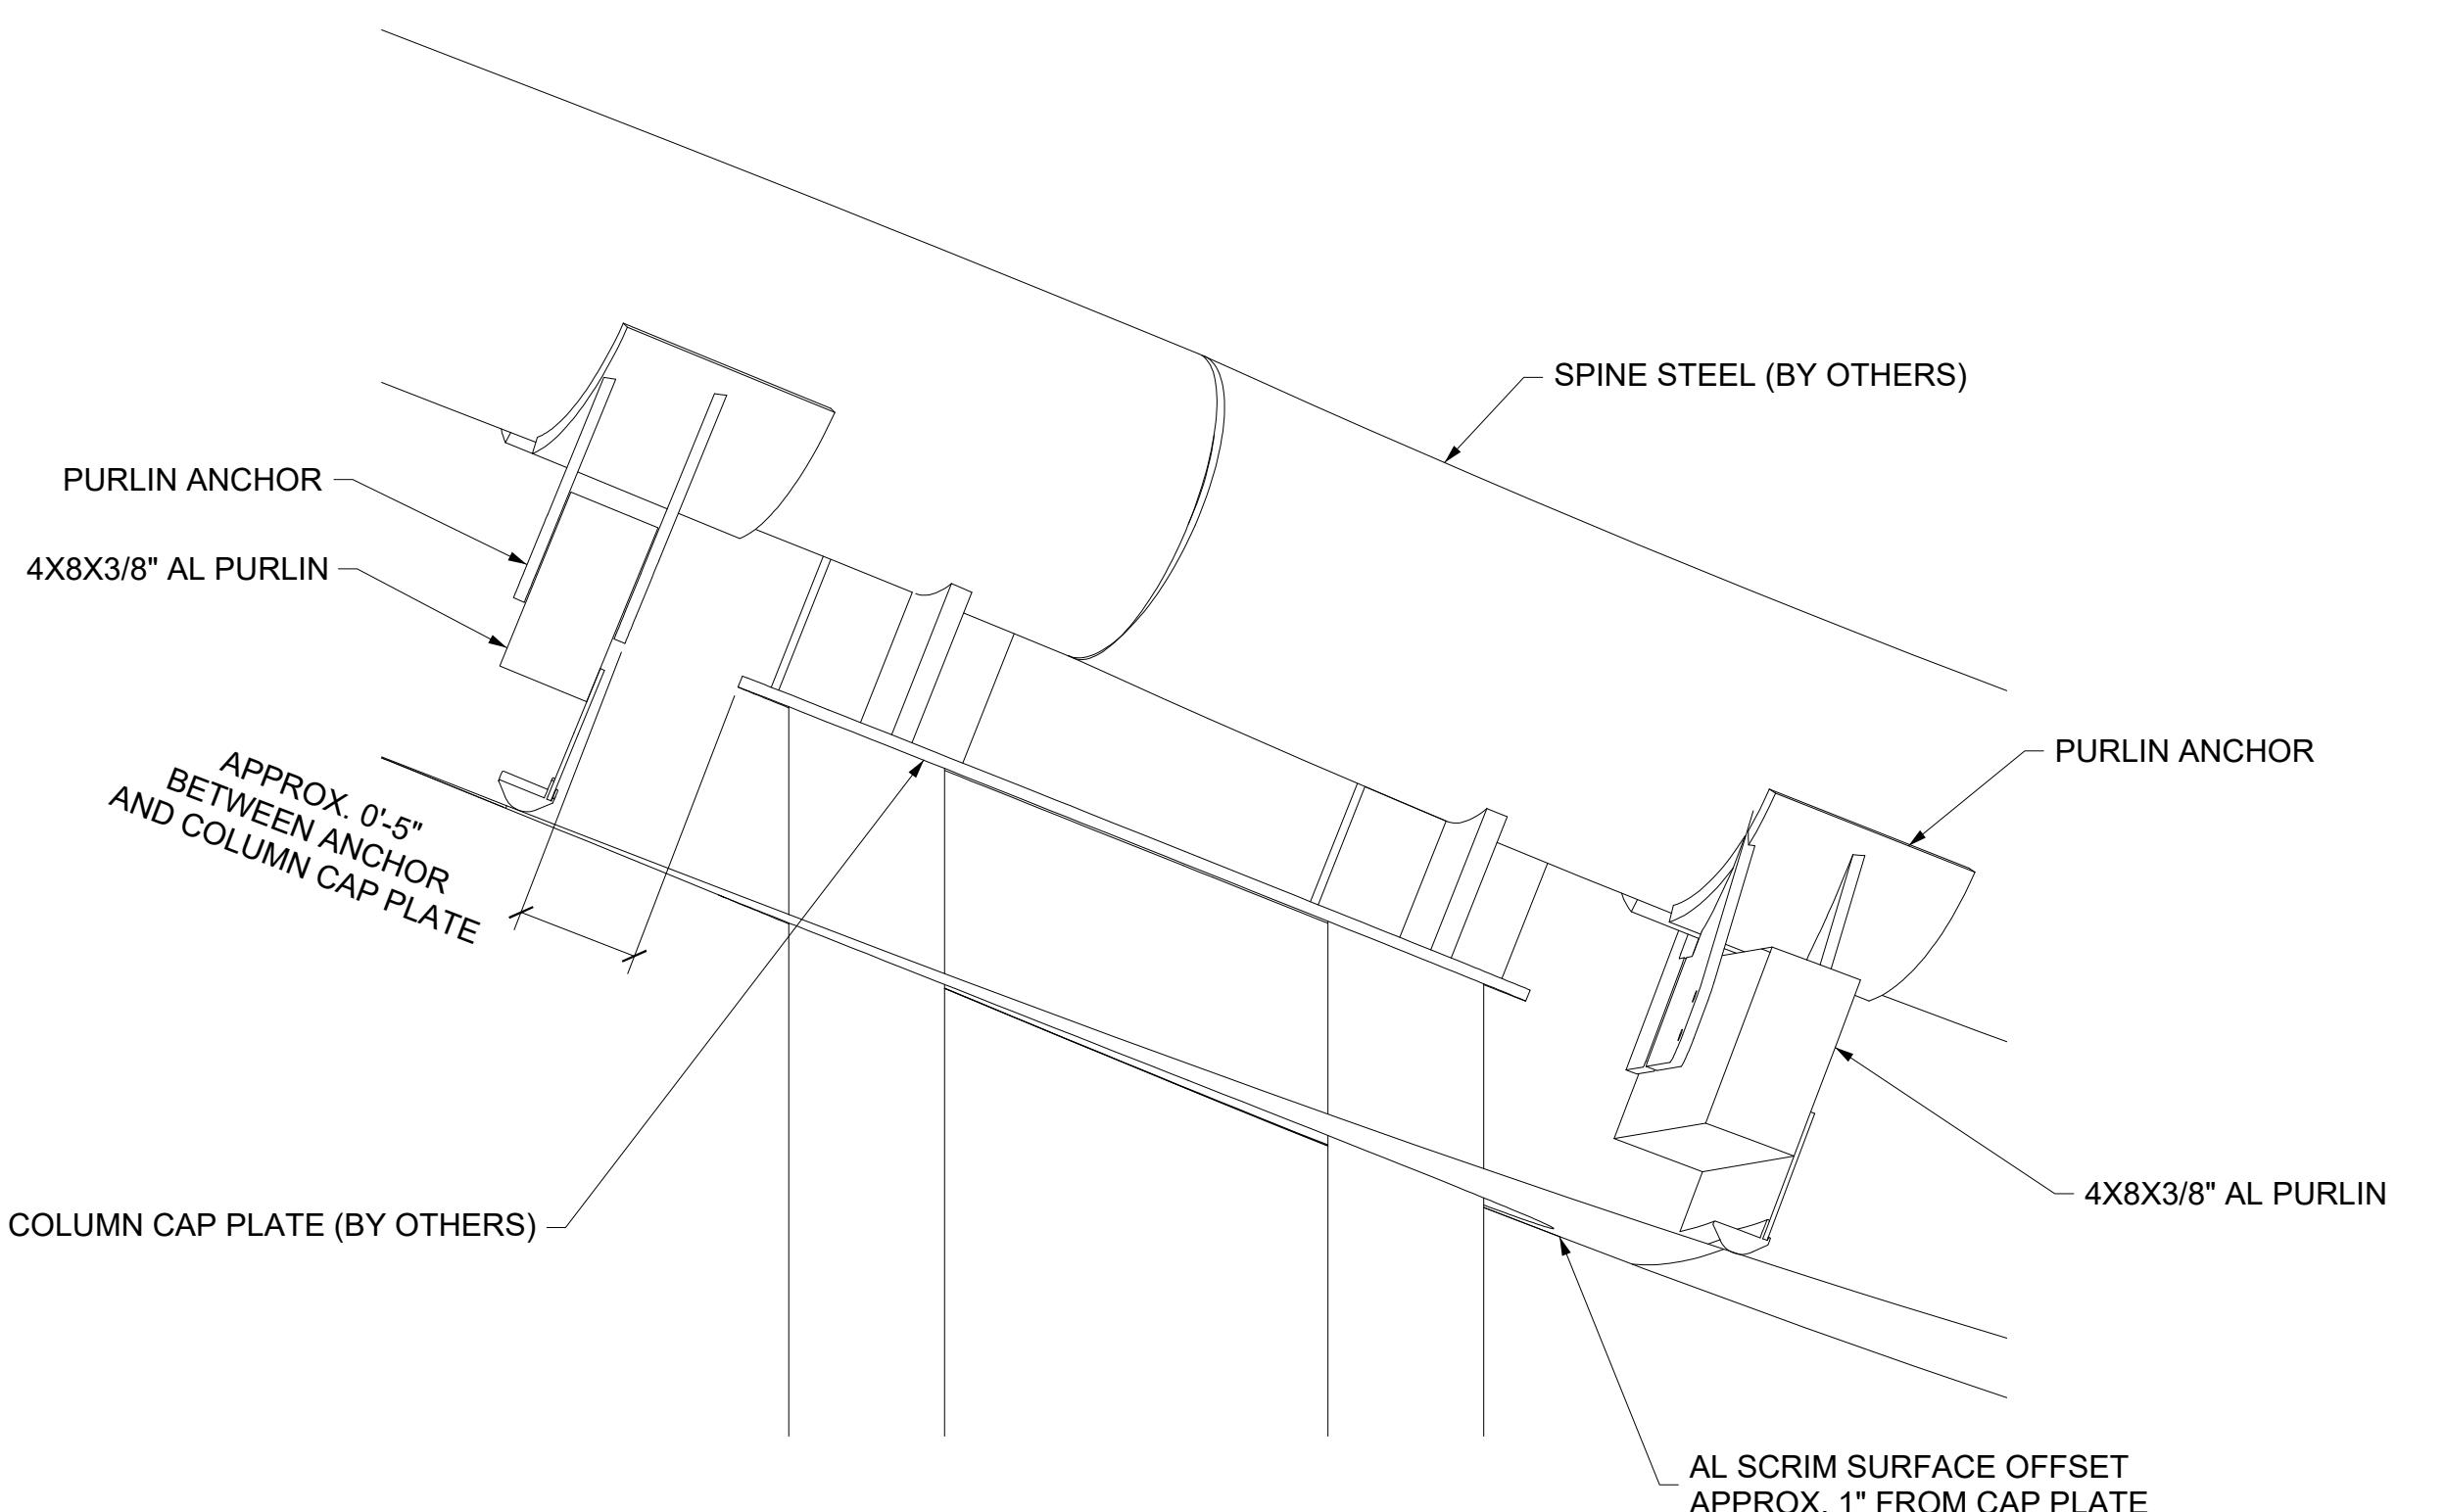

② CANOPY CROSS SECTION AT COLUMNS

SCALE: 1 1/2" = 1'-0"
ZAHNER REF: N/A
ARCH REF: N/A

| | | |
|------------------------|-------|-------------|
| SET ISSUE DATES | | |
| DATE | ISSUE | |
| 01/20/22 100% DRAWINGS | | |
| | | |
| REVISIONS | | |
| NO. | DATE | DESCRIPTION |
| | | |
| | | |
| | | |

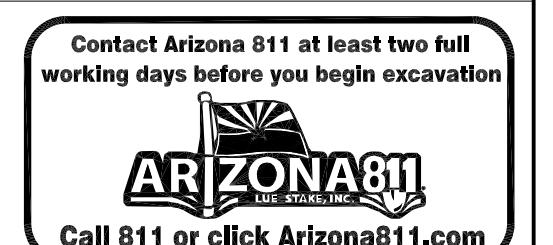

| | | | |
|------------------|--|--|-----|
| DATE: 01/20/2022 | | REVISION: | BY: |
| ENGINEER | | PUBLIC WORKS | |
| | | CITY OF SCOTTSDALE CAPITAL PROJECT MANAGEMENT | |
| SHEET TITLE | | 7447 E. INDIAN SCHOOL RD. SCOTTSDALE, ARIZONA 85251 | |

360 CANOPY - CROSS SECTION AT WALKING PATH

PROJECT TITLE

CITY OF SCOTTSDALE
CIVIC CENTER PLAZA

| THIS SHEET SCALED FOR 24X36" BORDER | SCALE | DESIGNED | BID NO. | XC-D502 |
|--|-------------|----------|-------------------------|---------|
| | DRAWN DS | AS-BUILT | COS PROJECT NO. DG04 | |